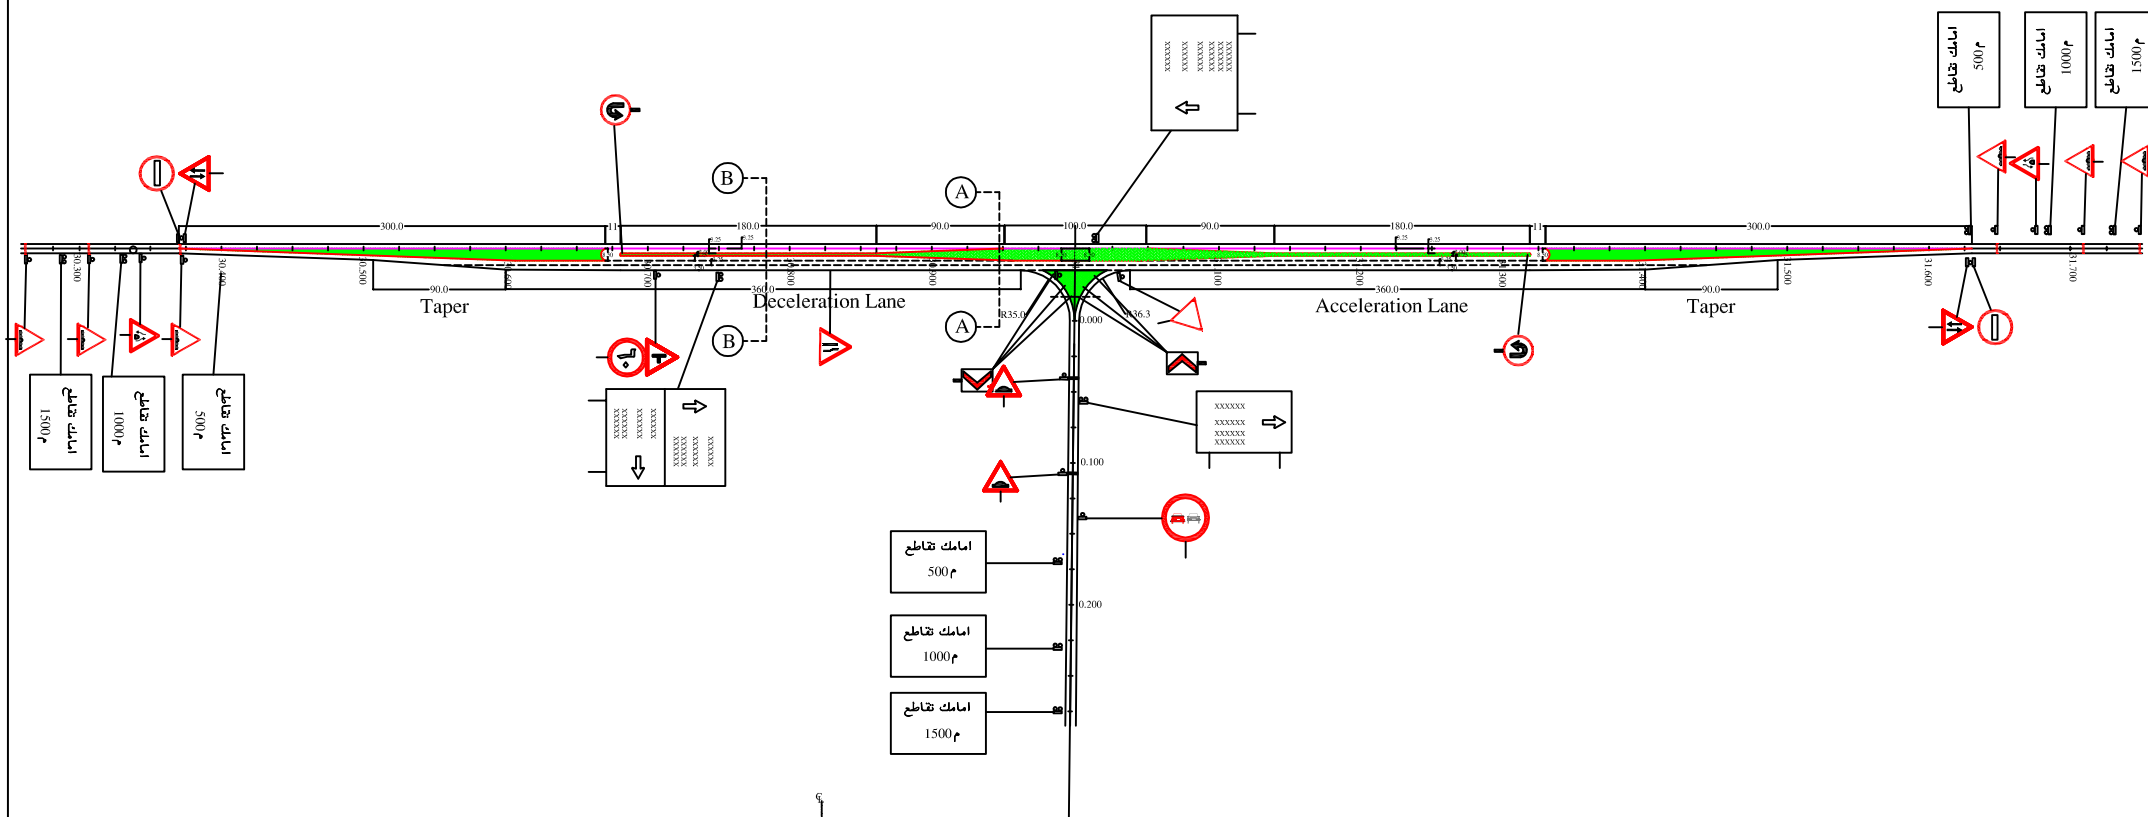


NOTE:
LOCATION OF SIGNS AND DISTANCES IN KILOMETERS ARE THE
RESPONSIBILITY OF THE CONSULTANT.

SECTION AT B-B

APPROVED AND DONE ACCORDING TO
SPECIFICATION OF M.O.T.