

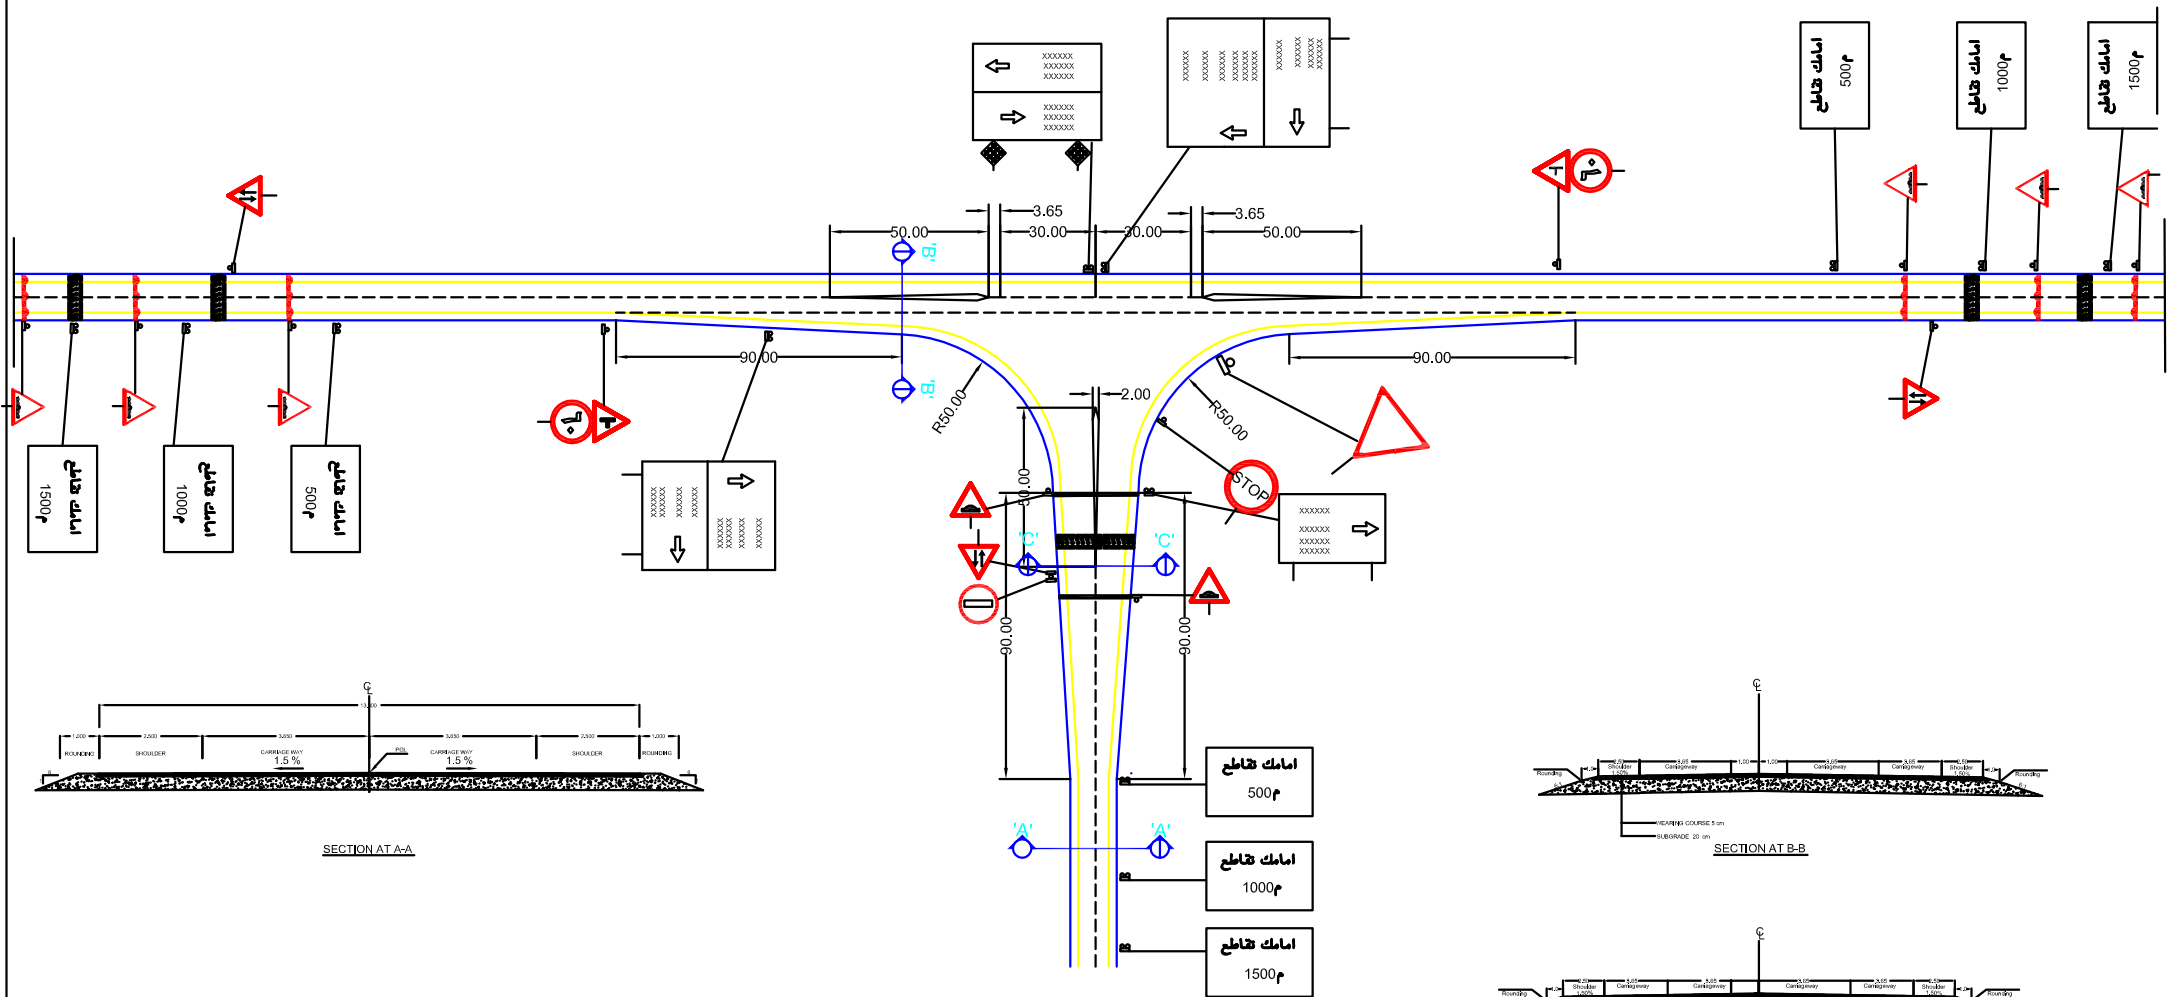


SECTION AT A-A

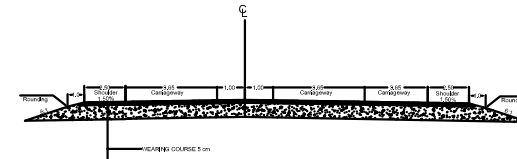

SECTION AT B-B

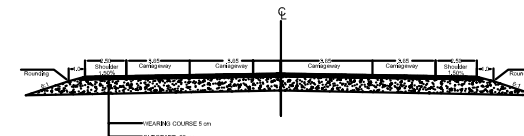

SECTION AT C-C

NOTE:
LOCATION OF SIGNS AND DISTANCES IN KILOMETERS ARE THE RESPONSIBILITY OF THE CONSULTANT.

APPROVED AND DONE ACCORDING TO
SPECIFICATION OF M.O.T.