




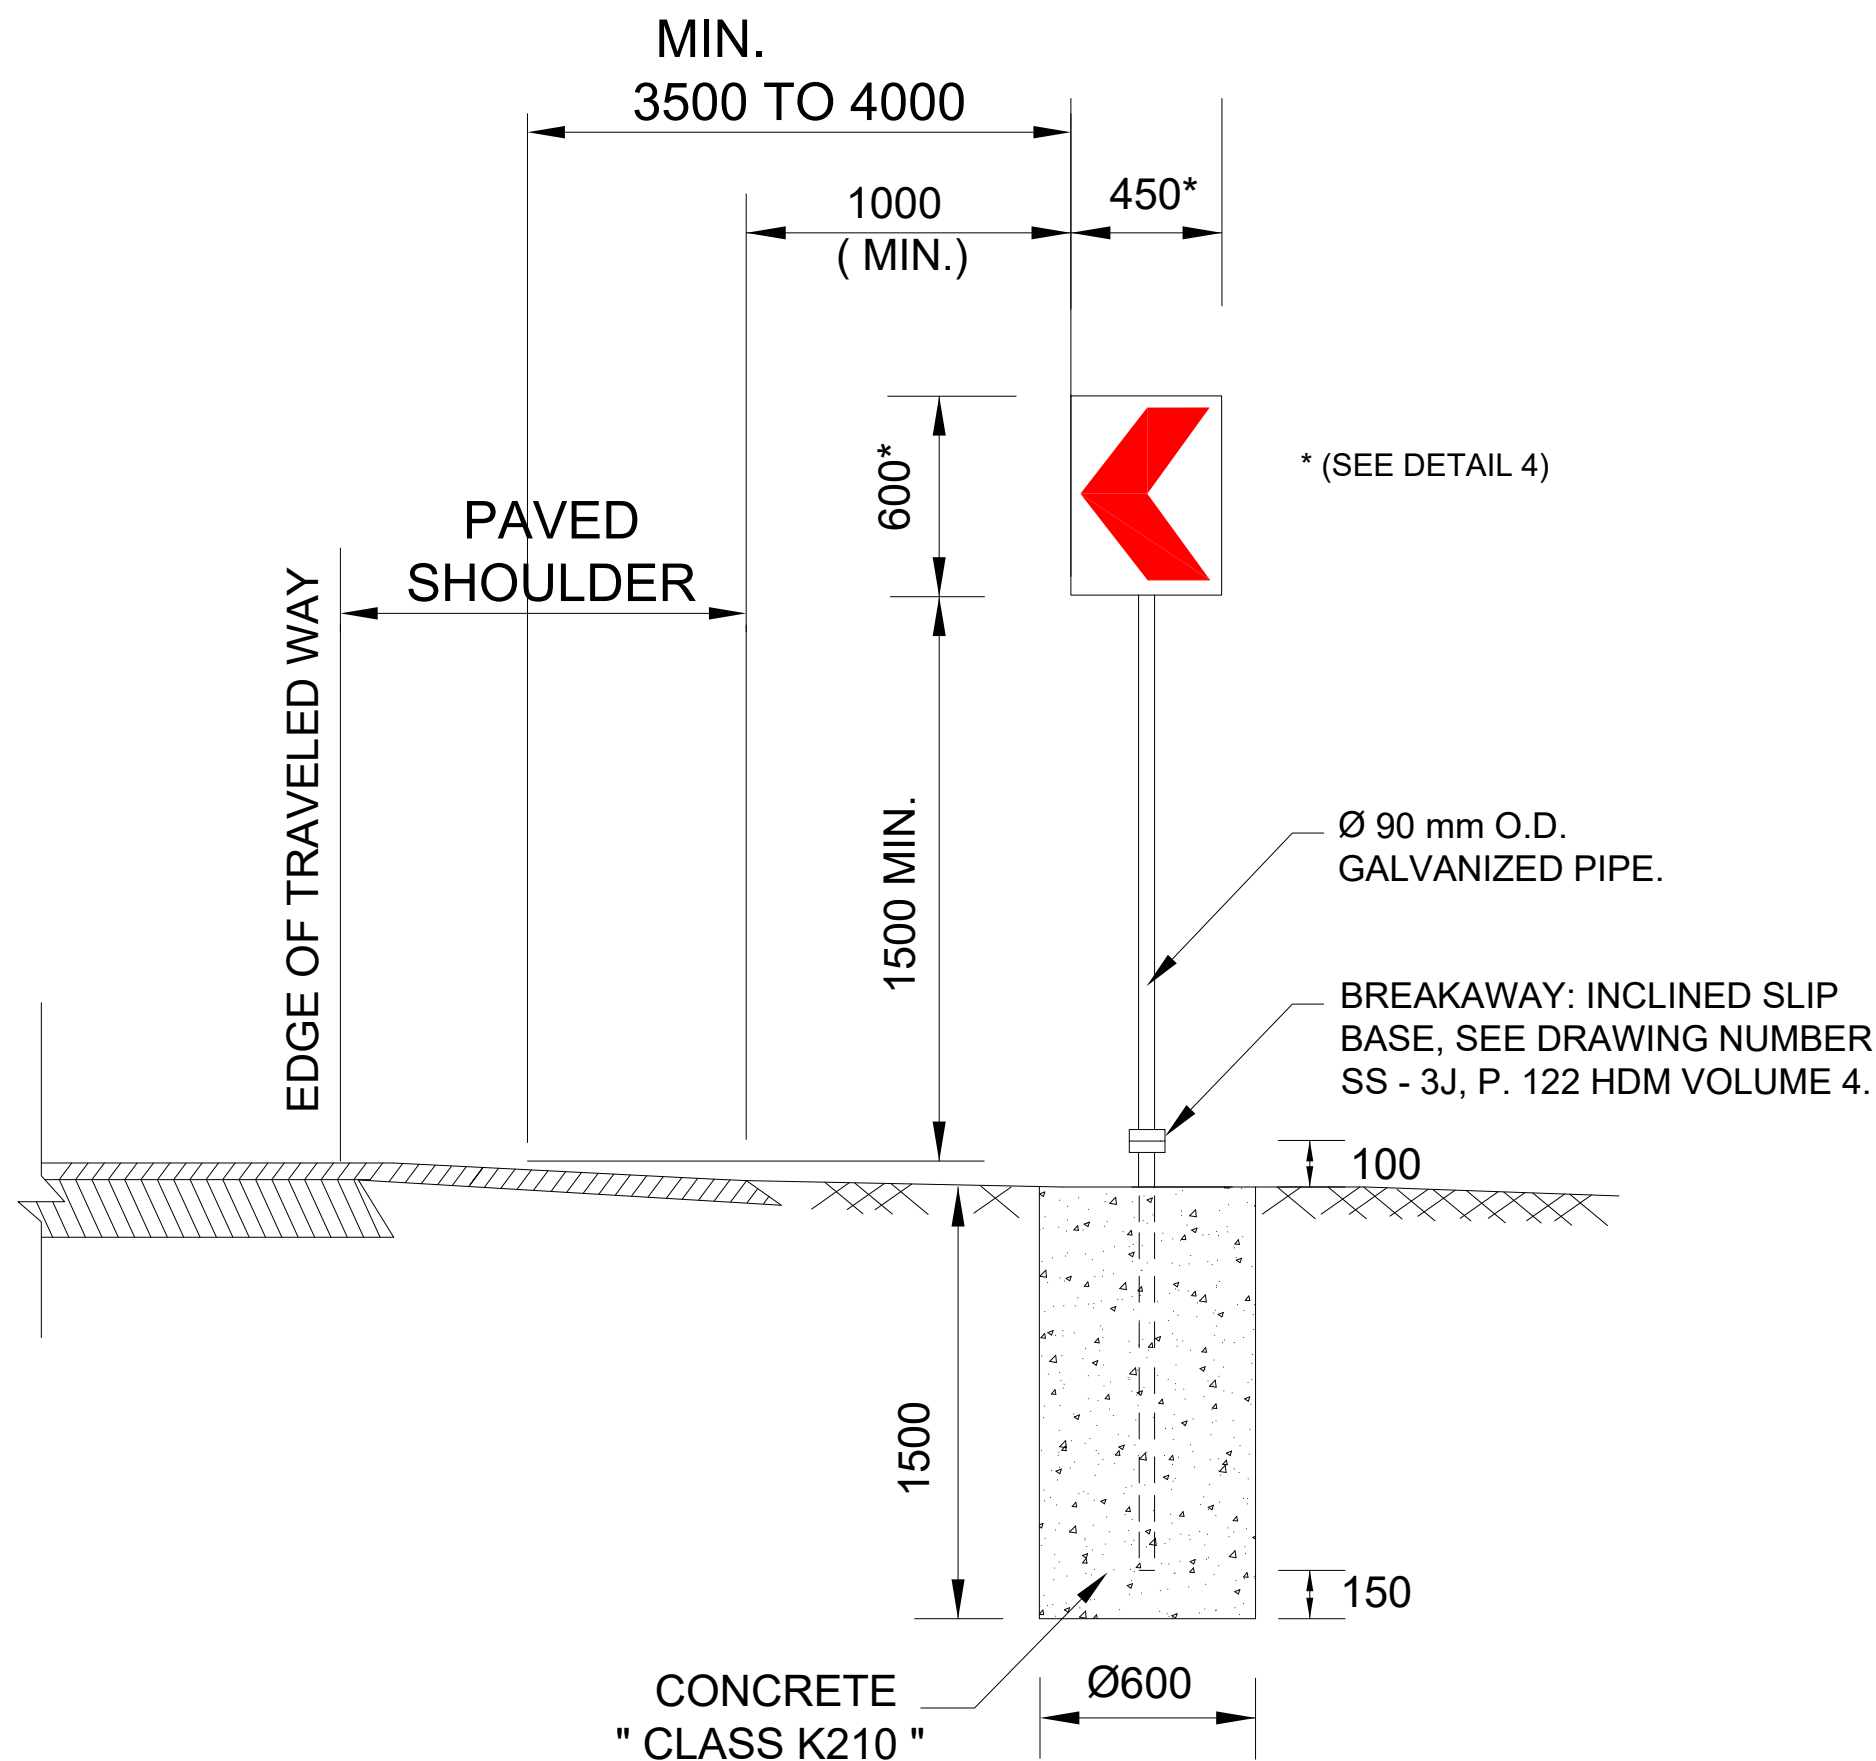


1 TYPICAL INSTALLATION DETAILS
IN RURAL AREA ROADWAYS

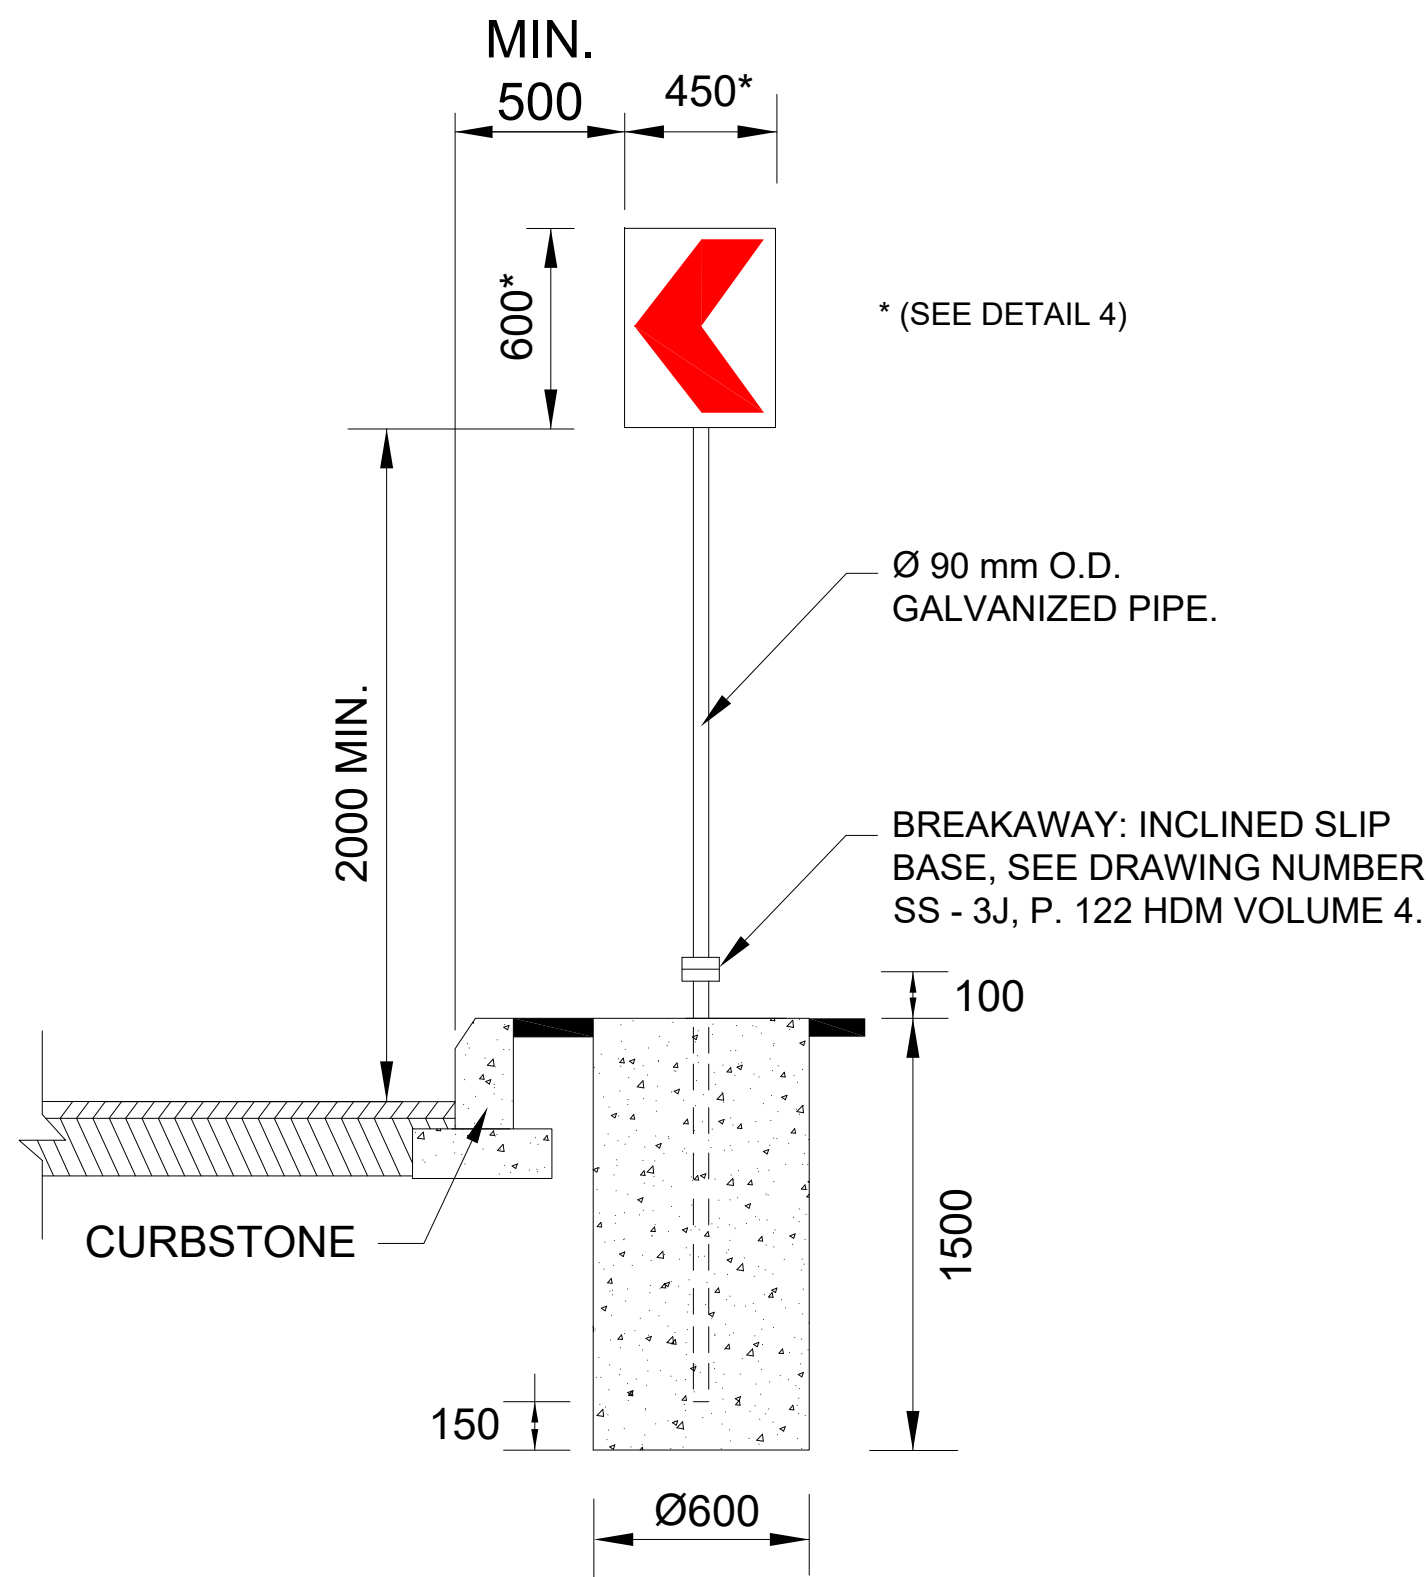


3 TYPICAL INSTALLATION DETAILS
IN URBAN AREA ROADWAYS

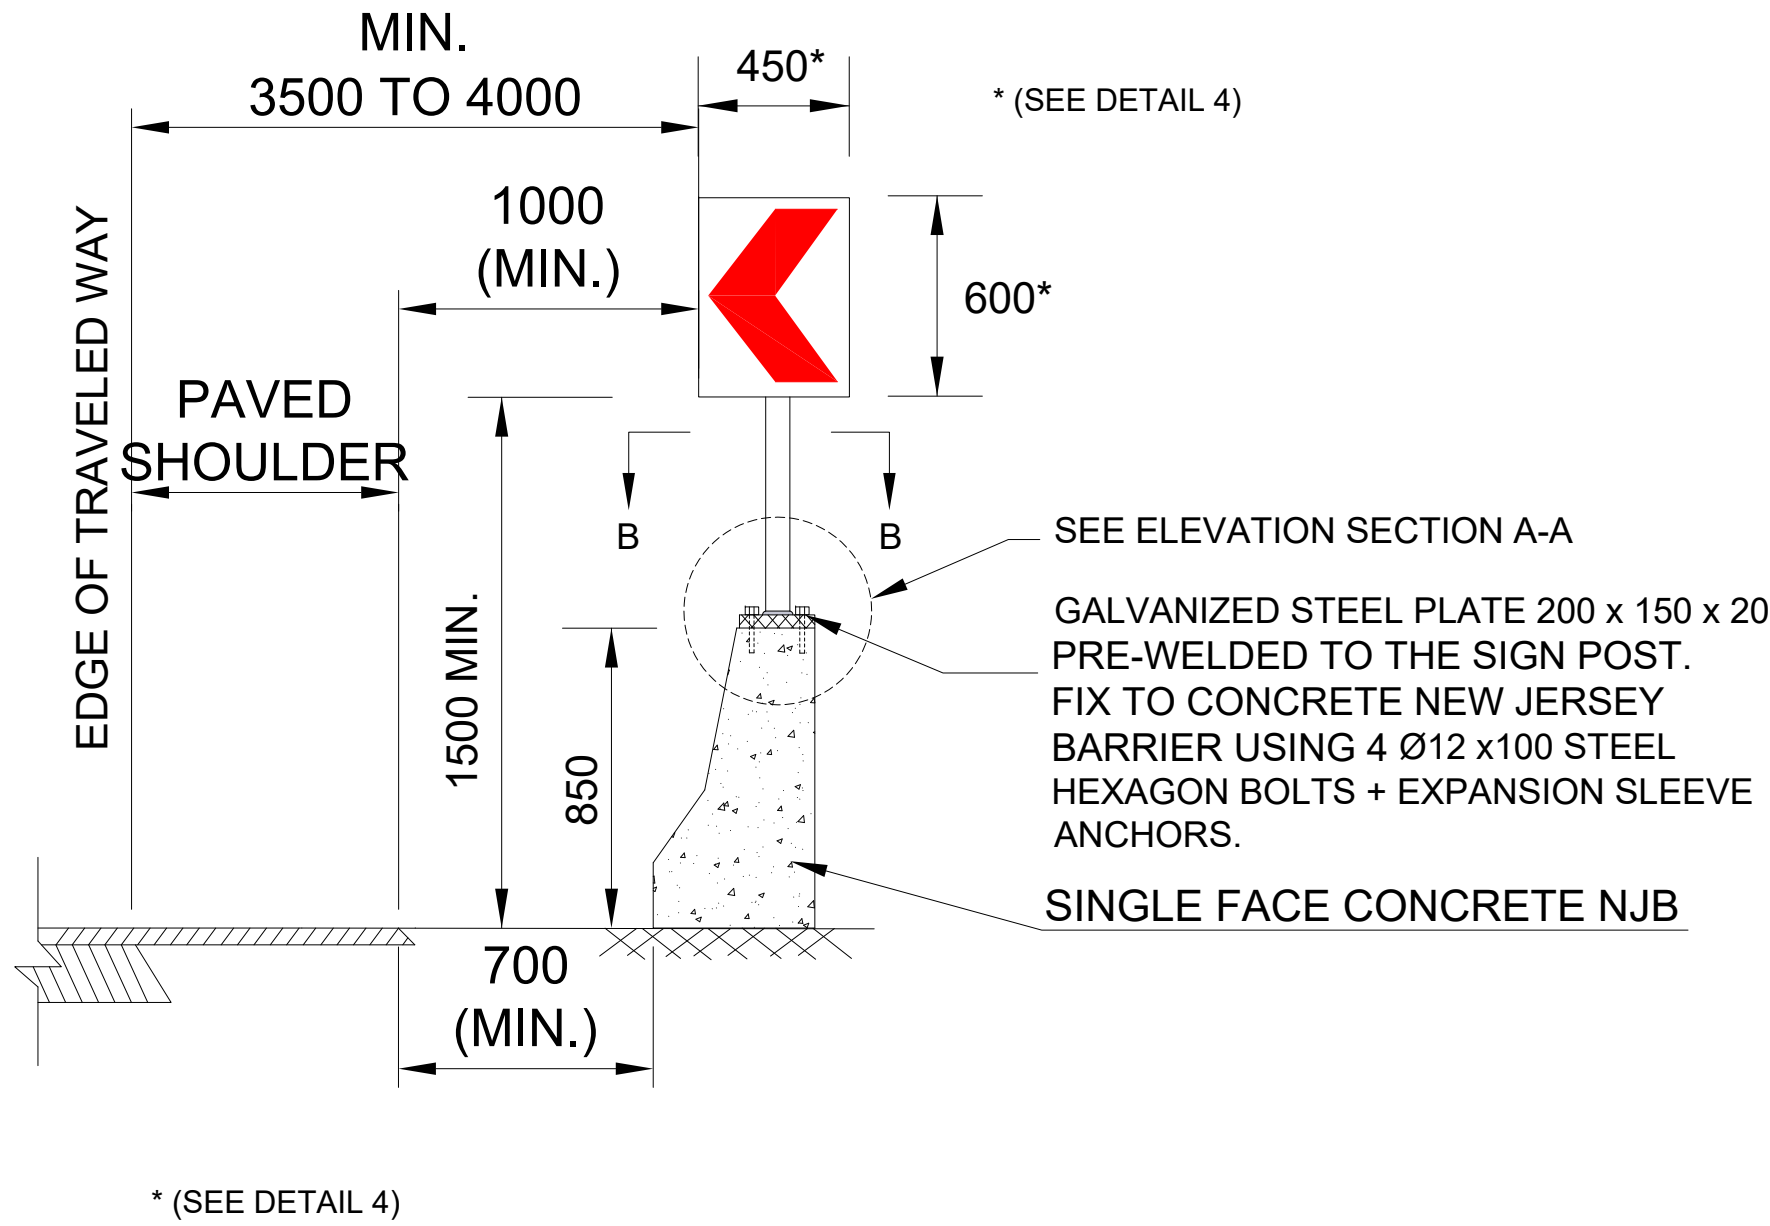


2 TYPICAL INSTALLATION DETAILS
ON CONCRETE NEW JERSEY BARRIER
(NJB) IN RURAL AREA ROADWAYS

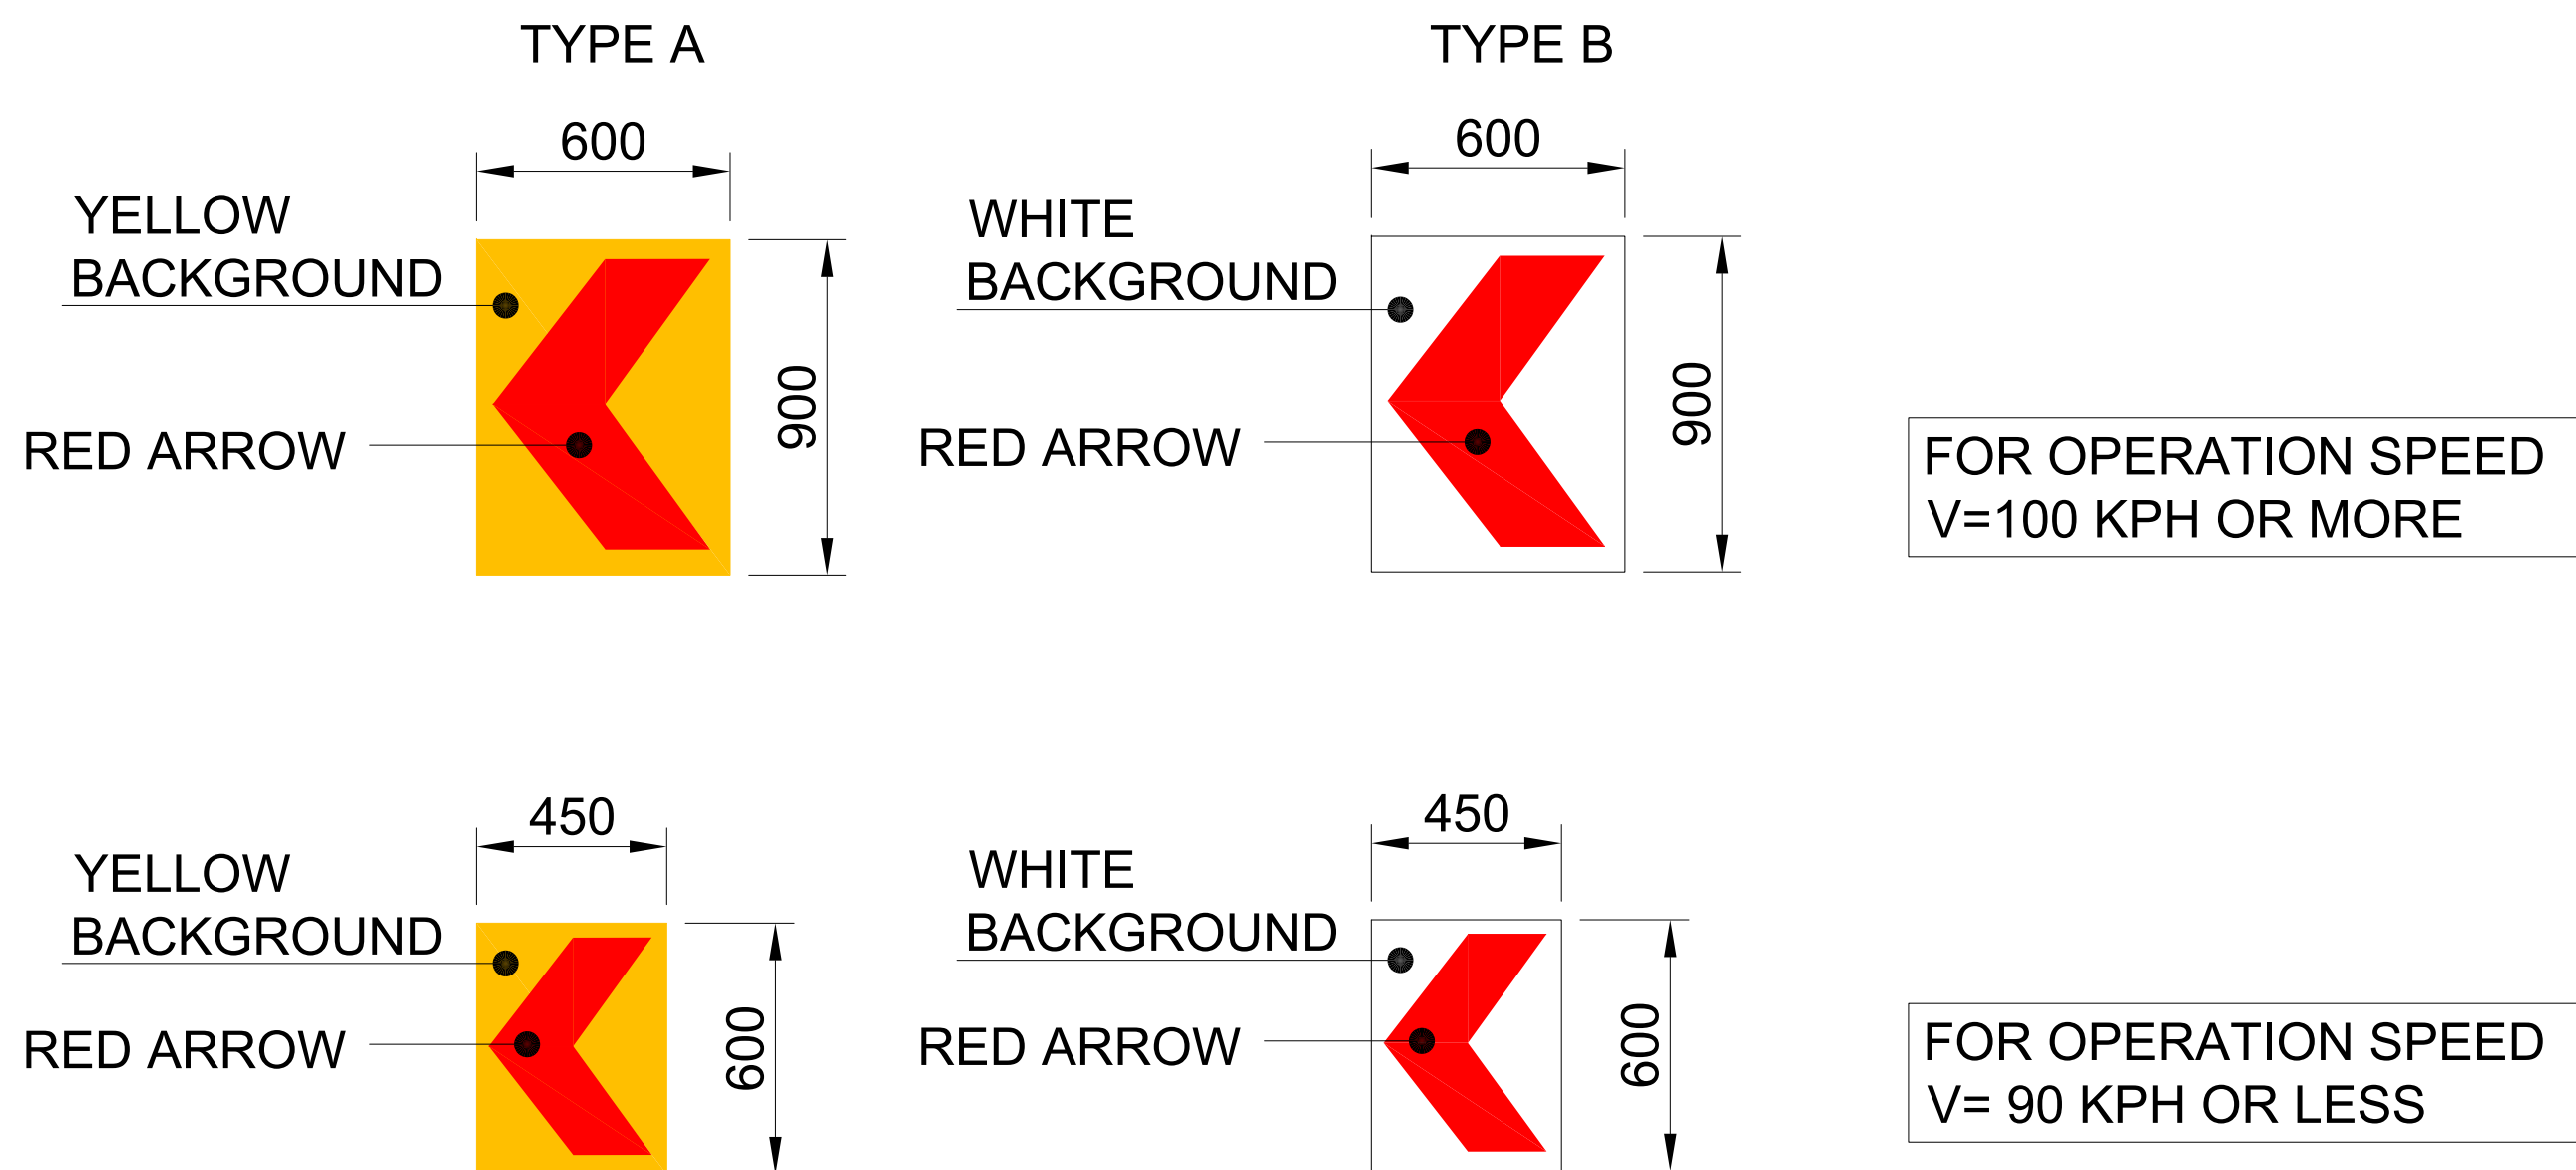

4 CHEVRON ALIGNMENT SIGN DETAILS
(W 37-1)

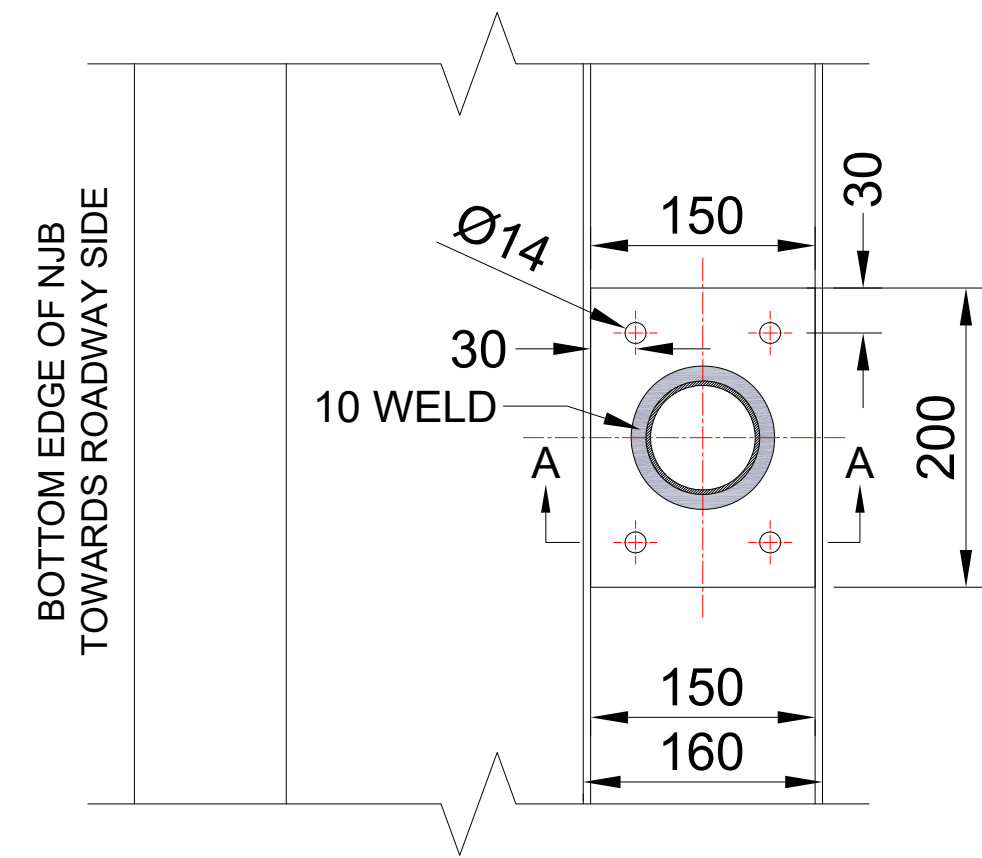

PLAN SECTION B-B
SIGN POST FIXATION DETAILS ON
CONCRETE NEW JERSEY BARRIER

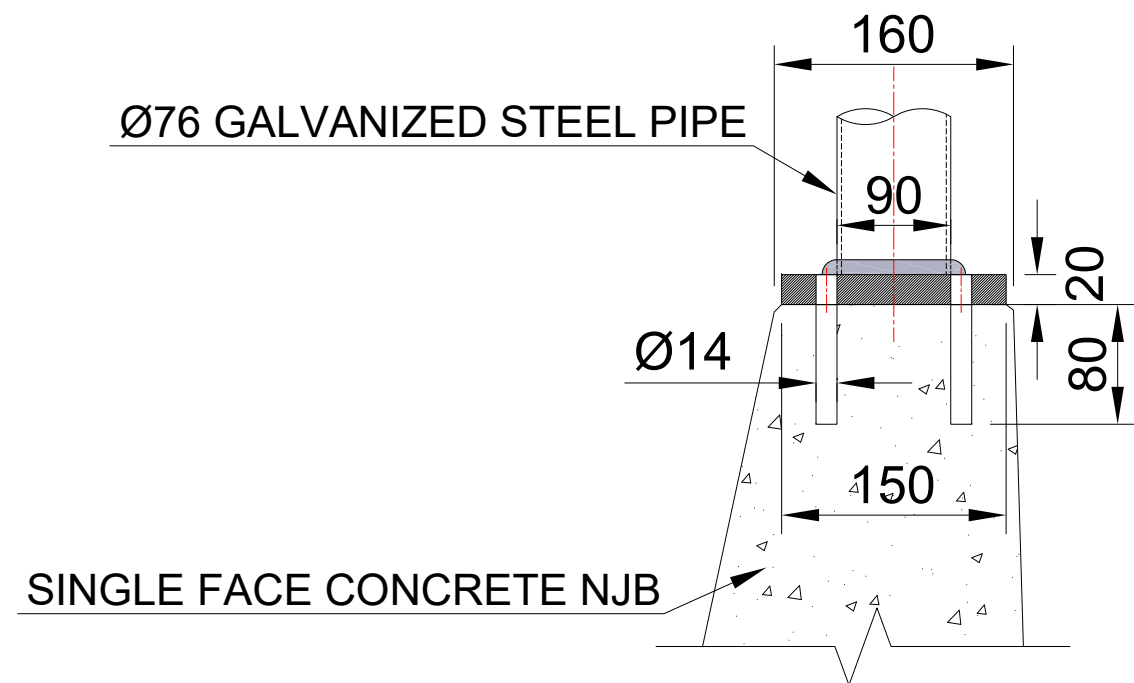

ELEVATION SECTION A-A
SIGN POST FIXATION DETAILS ON
CONCRETE NEW JERSEY BARRIER

NOTES :

1. DIMENSIONS SHOWN ARE IN MILLIMETERS AND NOT TO SCALE.

2. CHEVRON SIGN IS USED AS GUIDANCE FOR THE DRIVERS TO CHANGES IN THE HORIZONTAL ALIGNMENT OF THE ROADWAY.

3. TYPE A IS USED IN DETOUR WORK AREAS OR ROAD UNDER CONSTRUCTION OR MAINTENANCE OPERATIONS, WHILE TYPE B IS USED IN NORMAL ROADWAY OPERATION CONDITIONS.

4. SIGN INSTALLATION ON CONCRETE NEW JERSEY BARRIER SHOULD BE USED ONLY IF INSTALLATION OF REGULAR SIGN POST IS NOT POSSIBLE AT ALL BEHIND THE BARRIER.

5. PLATE TO POST WELDING PROCESS SHOULD OCCUR DURING MANUFACTURING PROCESS AND BEFORE GALVANIZATION PROCESS.

6. REFER TO MUTCD, PART 2, SECTION 2.01 AND SECTION 2.02 FOR GENERAL STANDARDS OF SIGN POSITIONING AND INSTALLATION.

7. TWO (600X450) CHEVRON SIGNS COULD BE USED ON THE SAME POST WITH 0.10 M VERTICAL GAP IN INSTALLATION LOCATIONS RECORDED FOR SIGN VISIBILITY ISSUES, KEEPING MIN. VERTICAL CLEARANCE OF 1.50 M

CHEVRON ALIGNMENT SIGN SPACING

POSTED SPEED (KM/HR)	CURVE RADIUS (M)	SIGN SPACING (M)
30 OR LESS	60 OR LESS	12
31 - 50	61 - 120	24
51 - 70	120 - 215	36
71 - 90	215 - 380	48
OVER 90	380 - 1000	60

KINGDOM OF SAUDI ARABIA
MINISTRY OF TRANSPORT



TITLE:

التفاصيل النموذجية الخاصة بلافتات
أسهم المنحنيات على الطرق

CHEVRON ALIGNMENT SIGN
TYPES & INSTALLATION DETAILS

DRAWING NUMBER:

JANUARY 2020

RD1-MOT-RSD-DWG-2001-016

SHEET SIZE: A1