




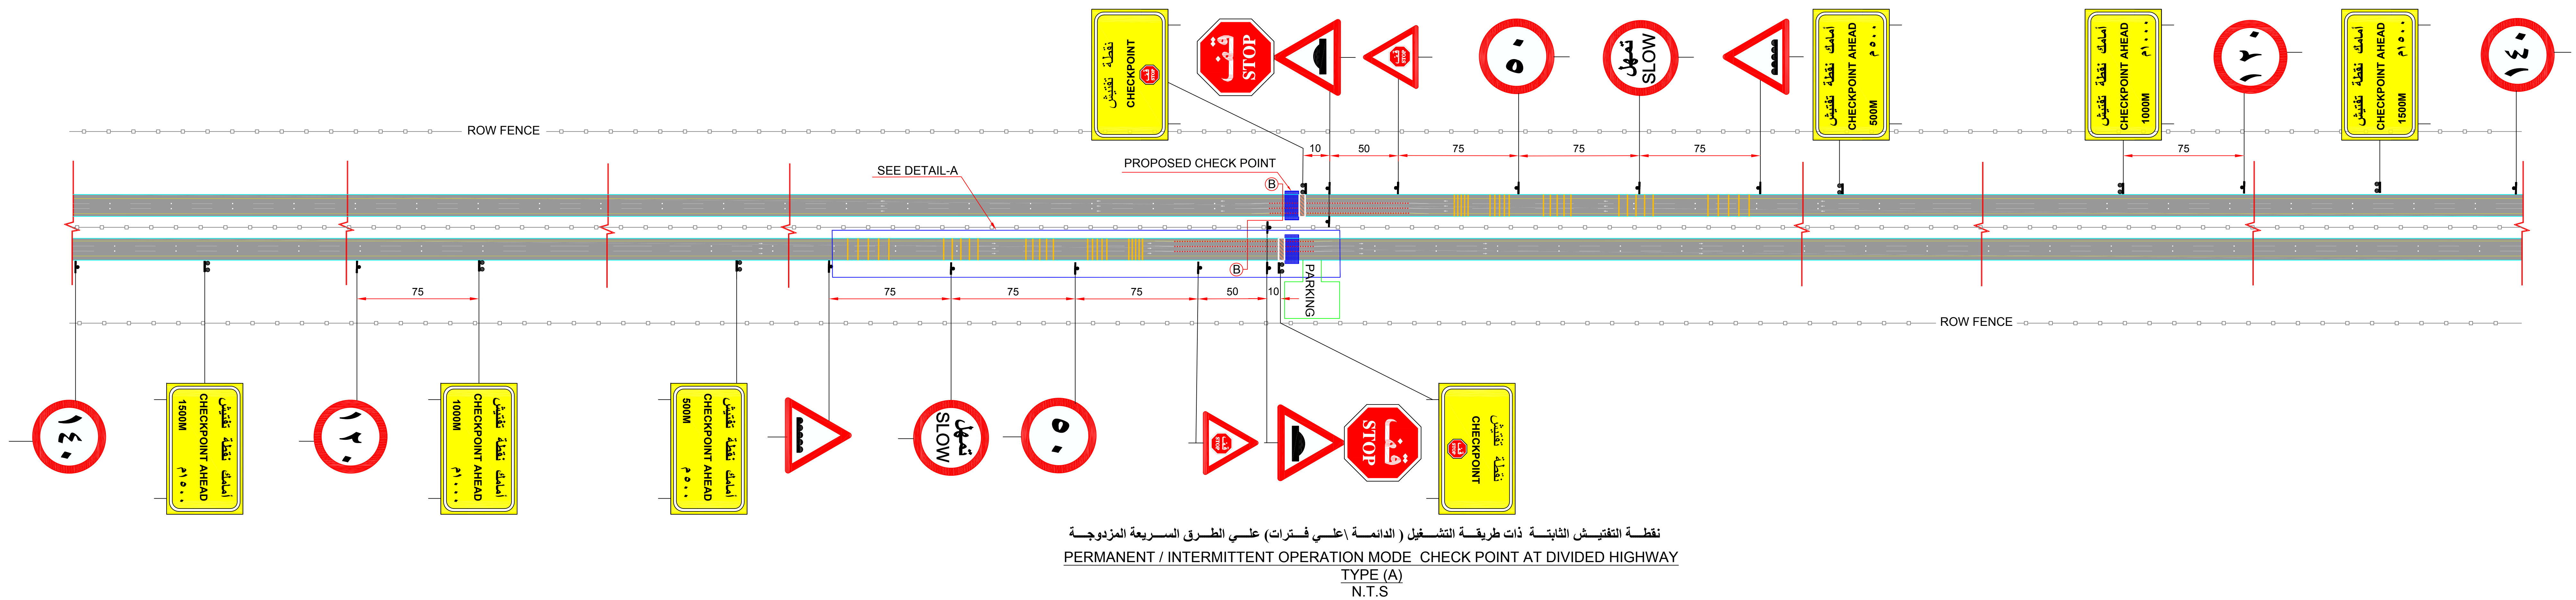


نقطة التفتيش الثابتة ذات طريقة التشغيل (الدائمة \عطي فترات) على الطرق السريعة المزدوجة
PERMANENT / INTERMITTENT OPERATION MODE CHECK POINT AT DIVIDED HIGHWAY
TYPE (A)
N.T.S

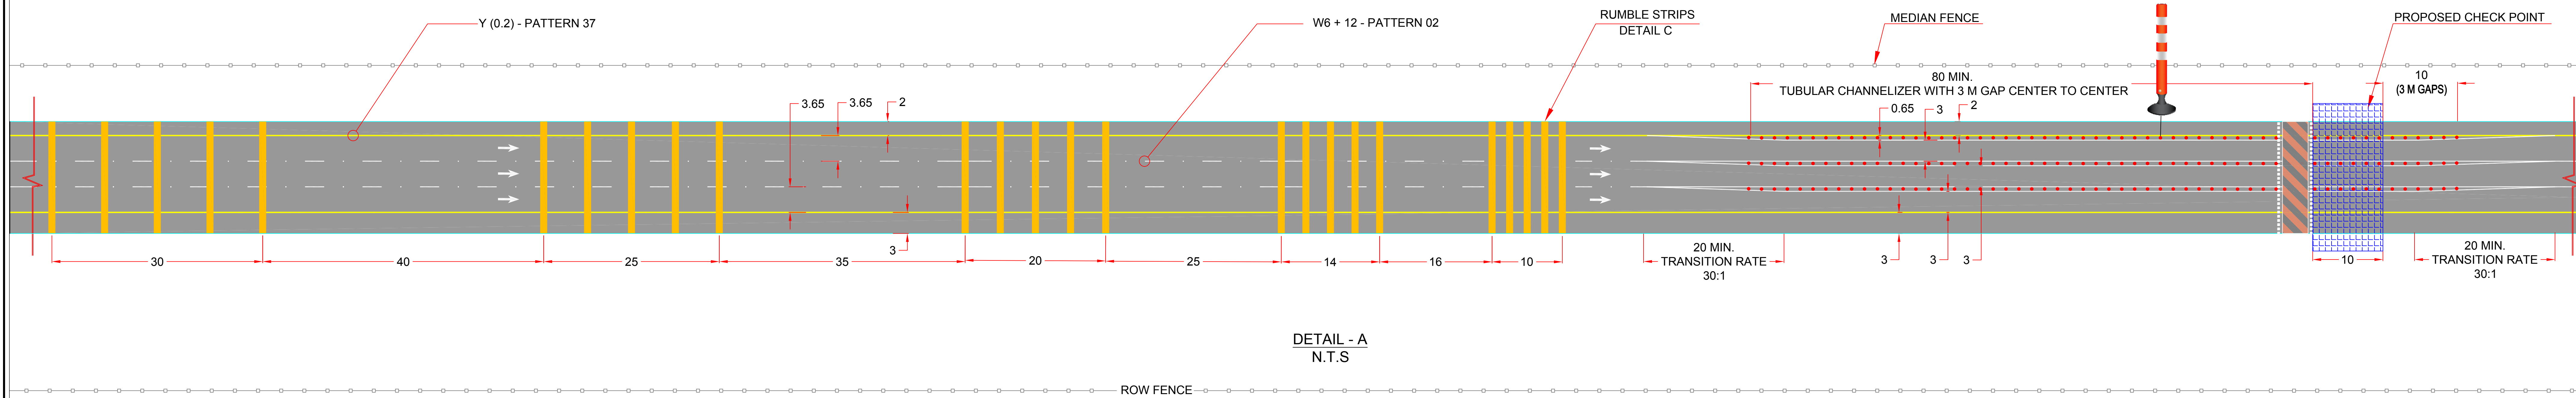


DETAIL - A
N.T.S

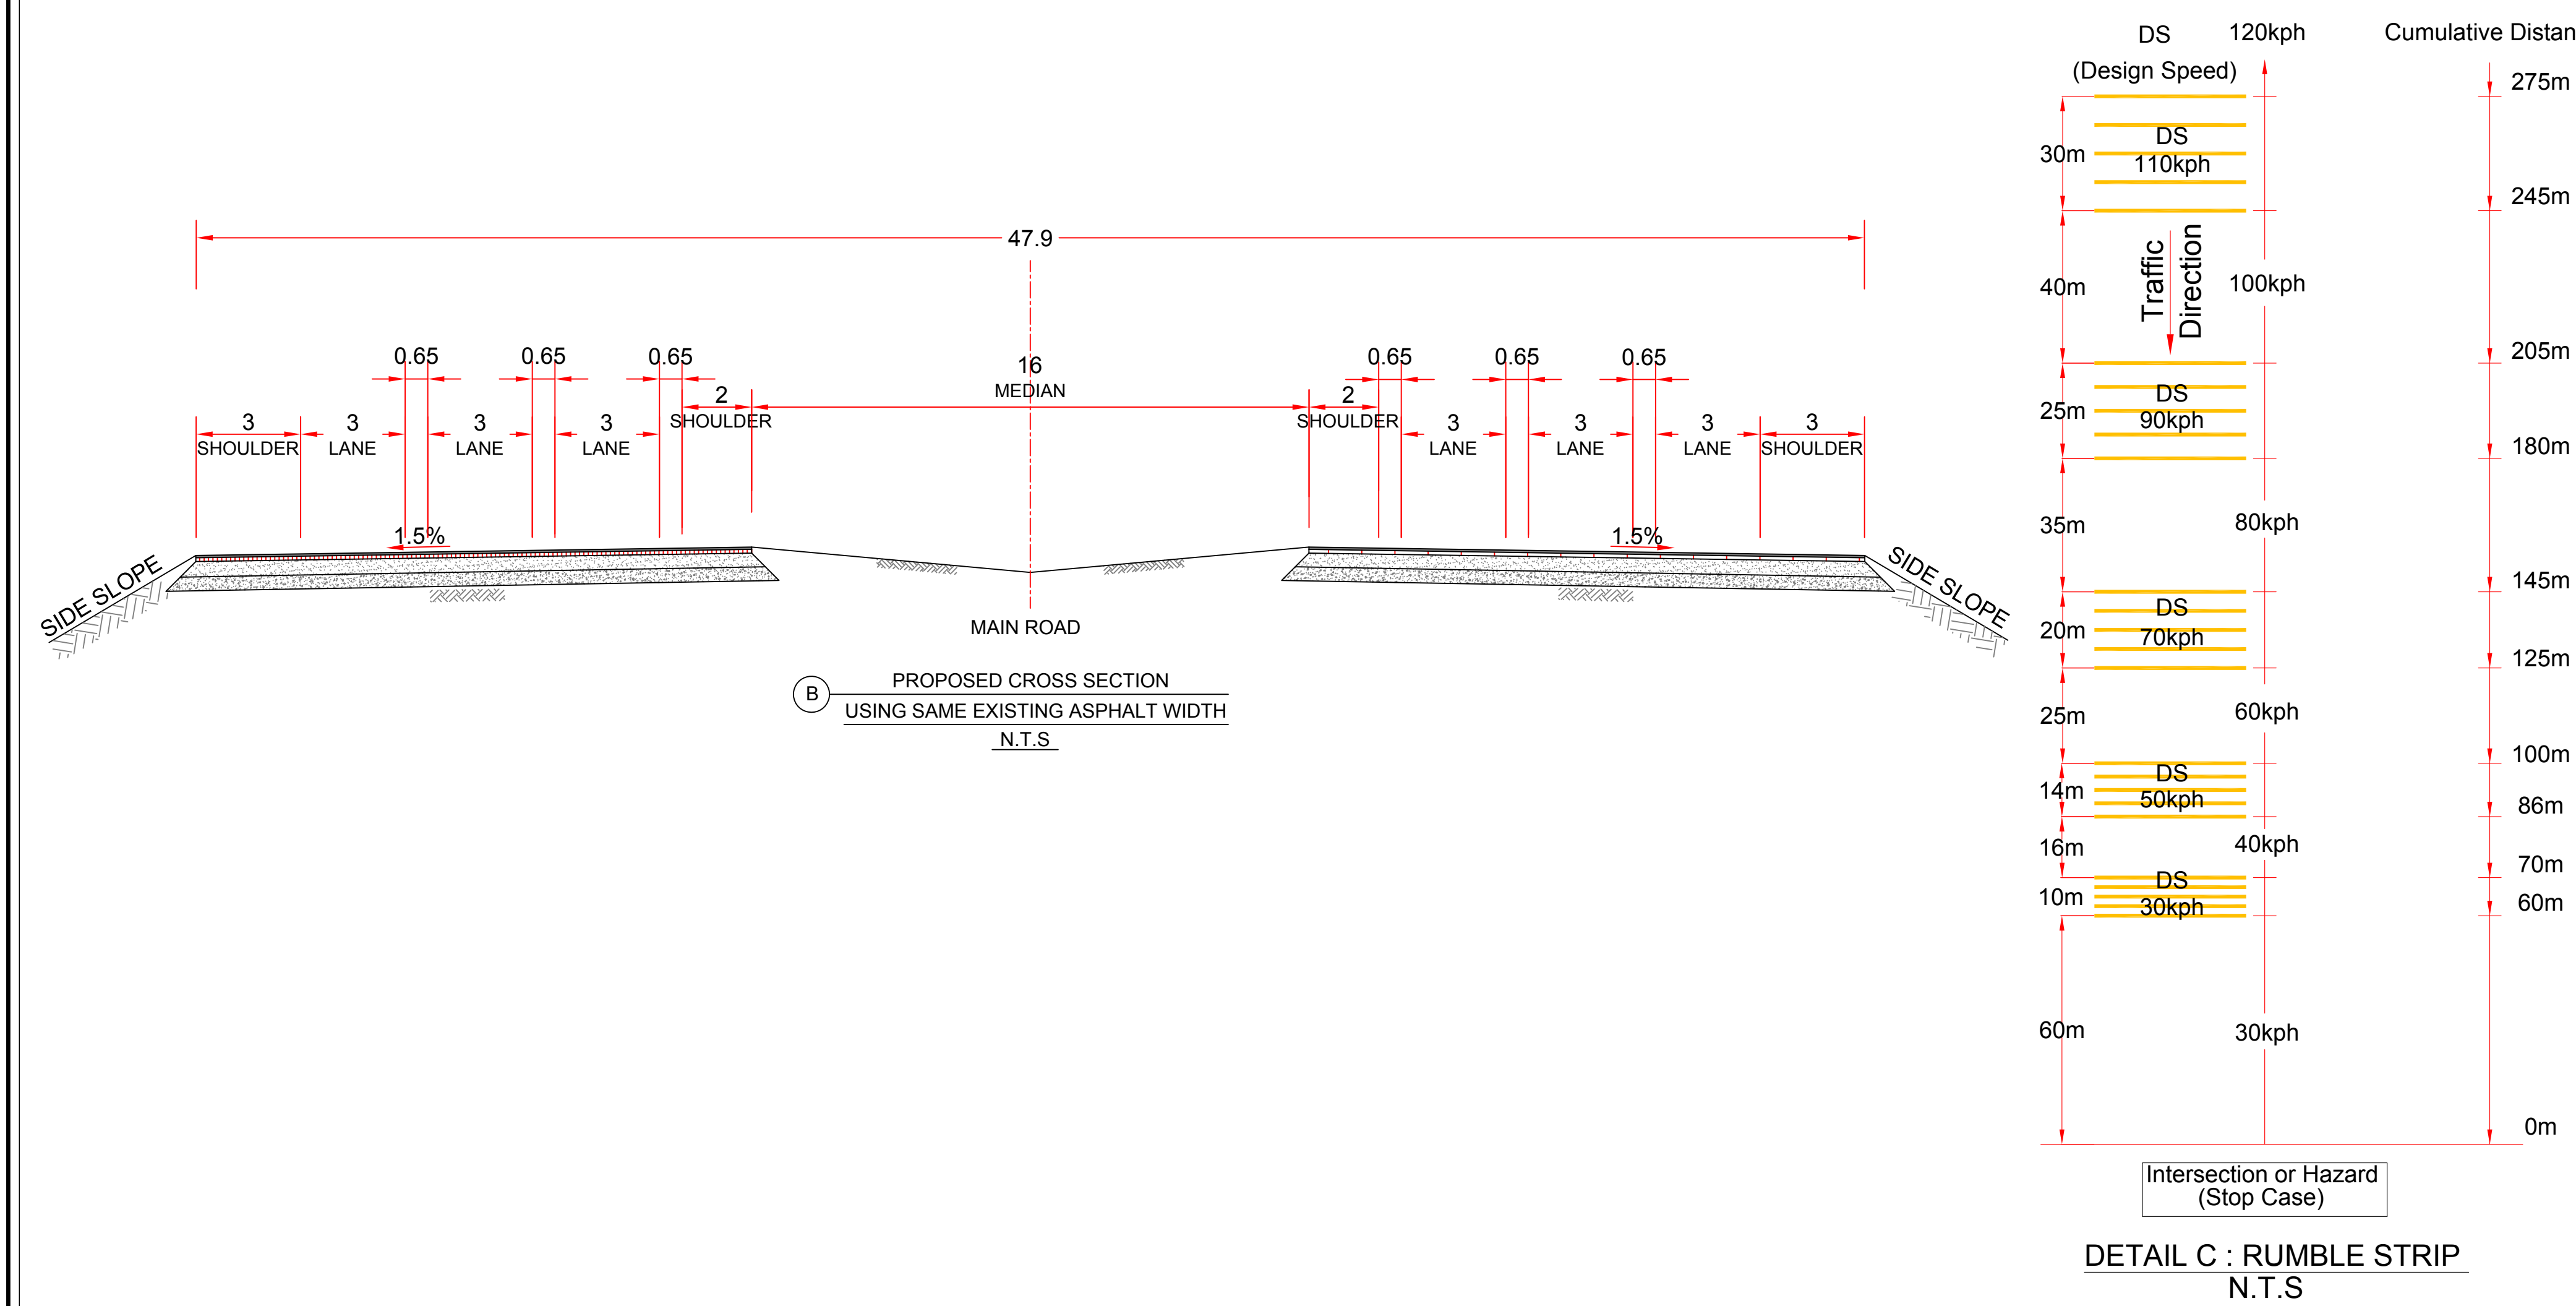

DETAIL C : RUMBLE STRIP
N.T.S

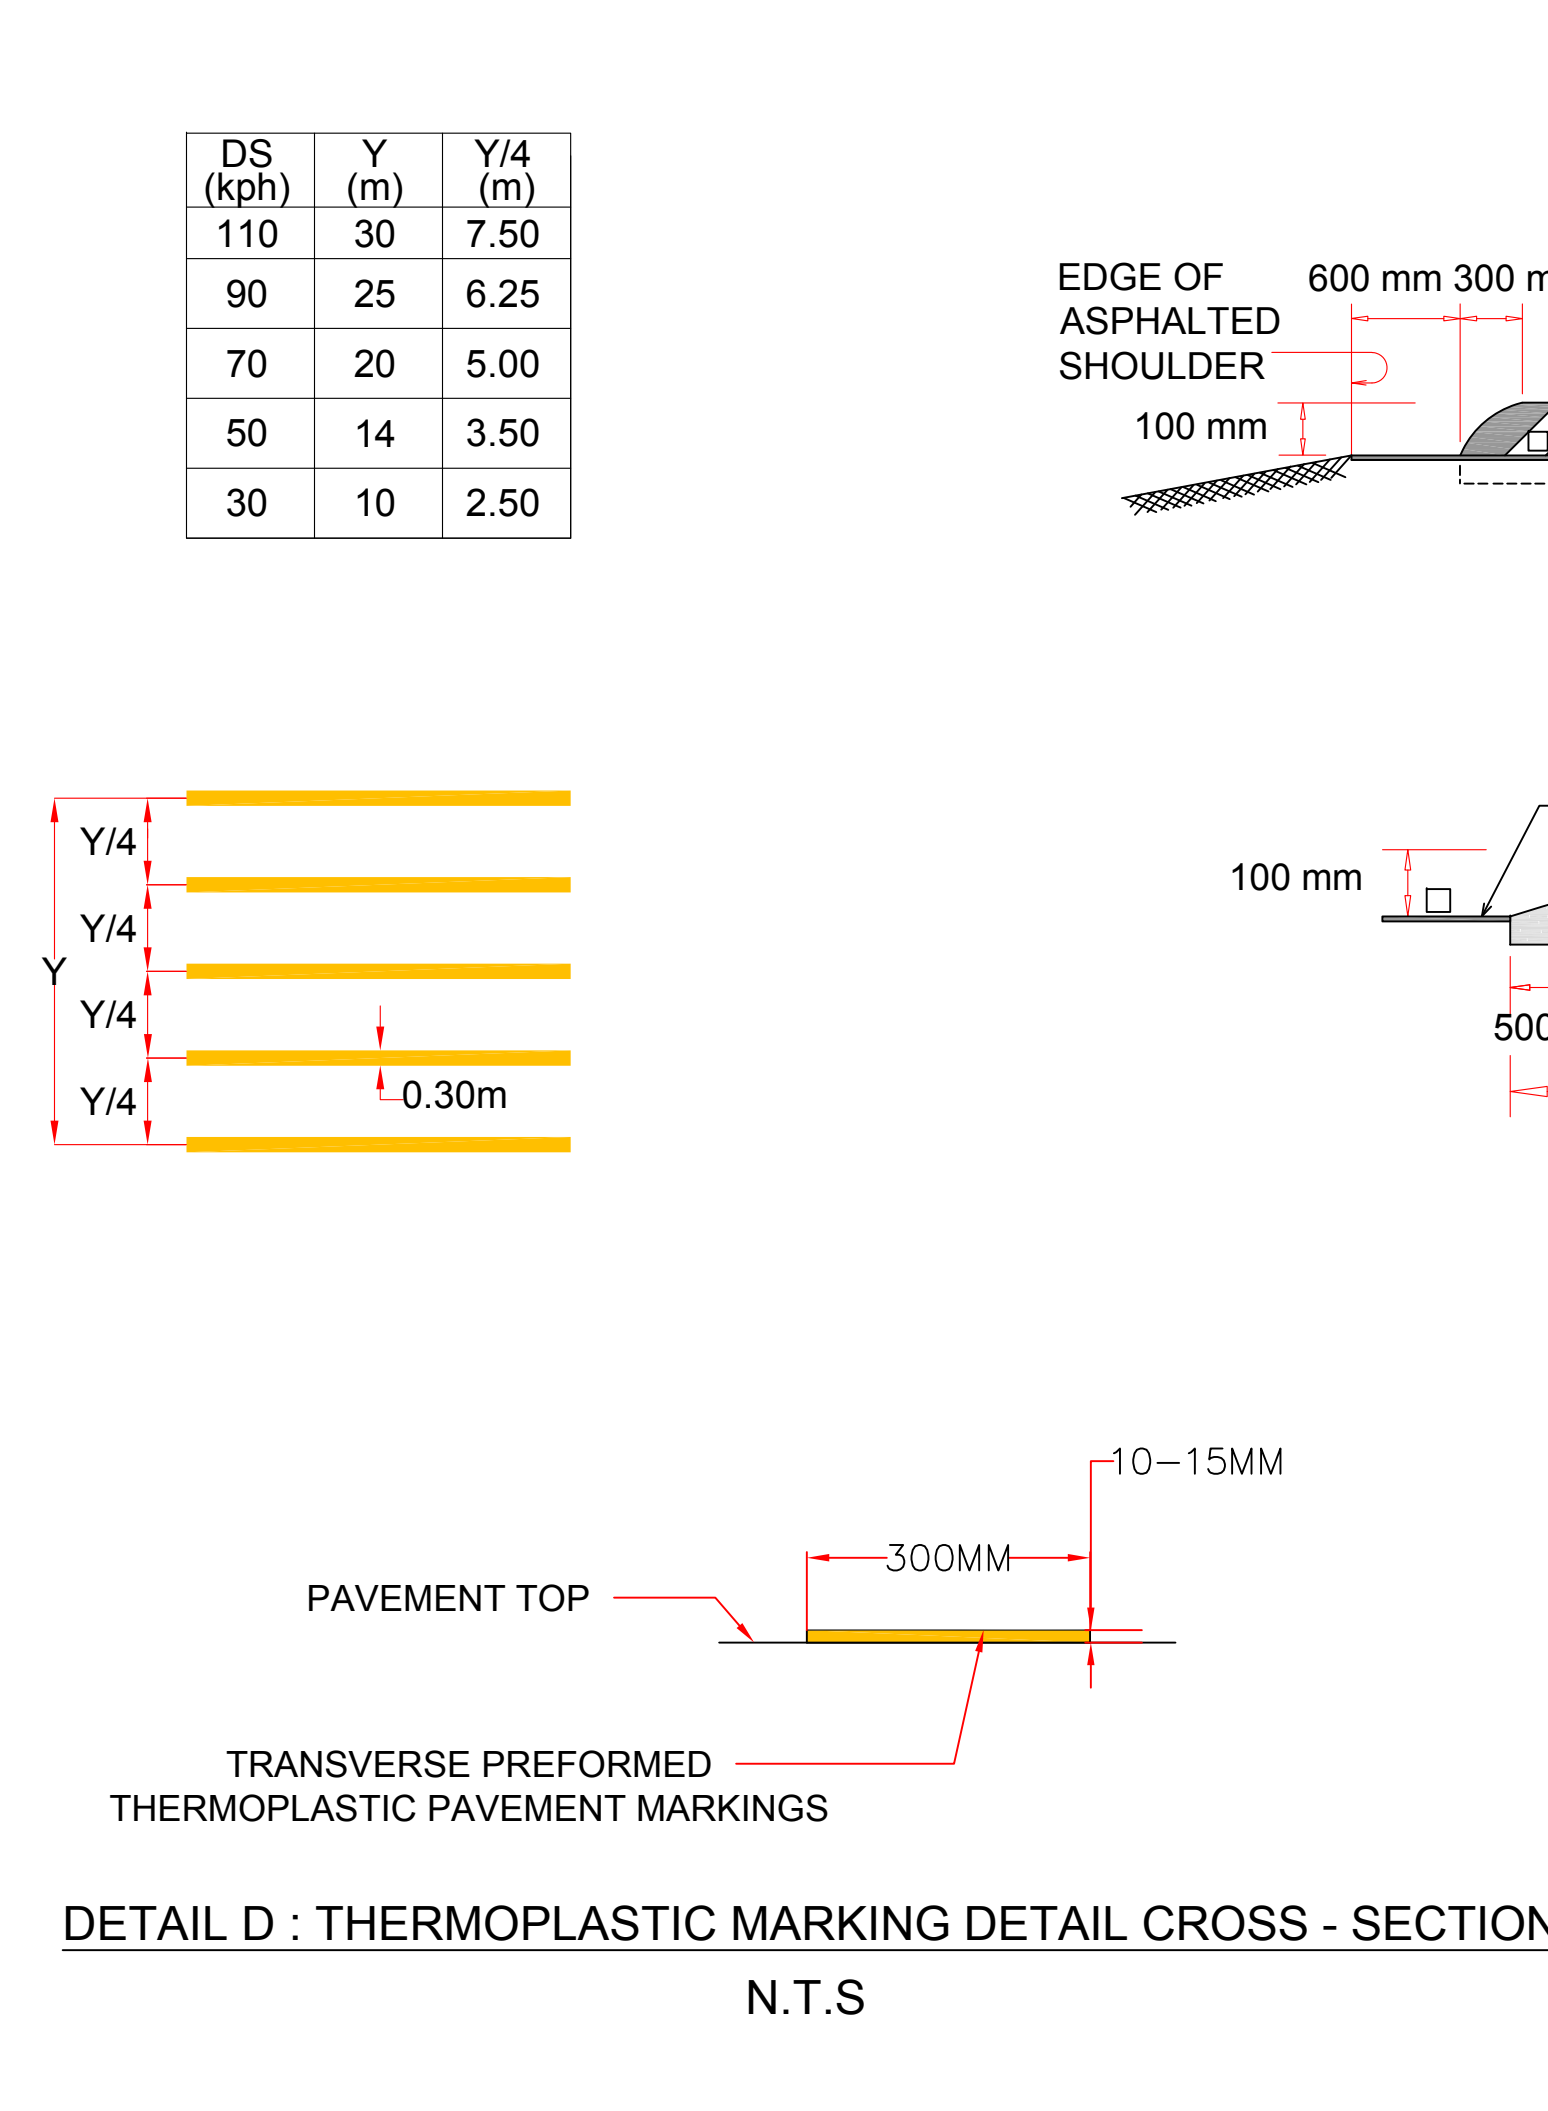

DETAIL D : THERMOPLASTIC MARKING DETAIL CROSS - SECTION
N.T.S

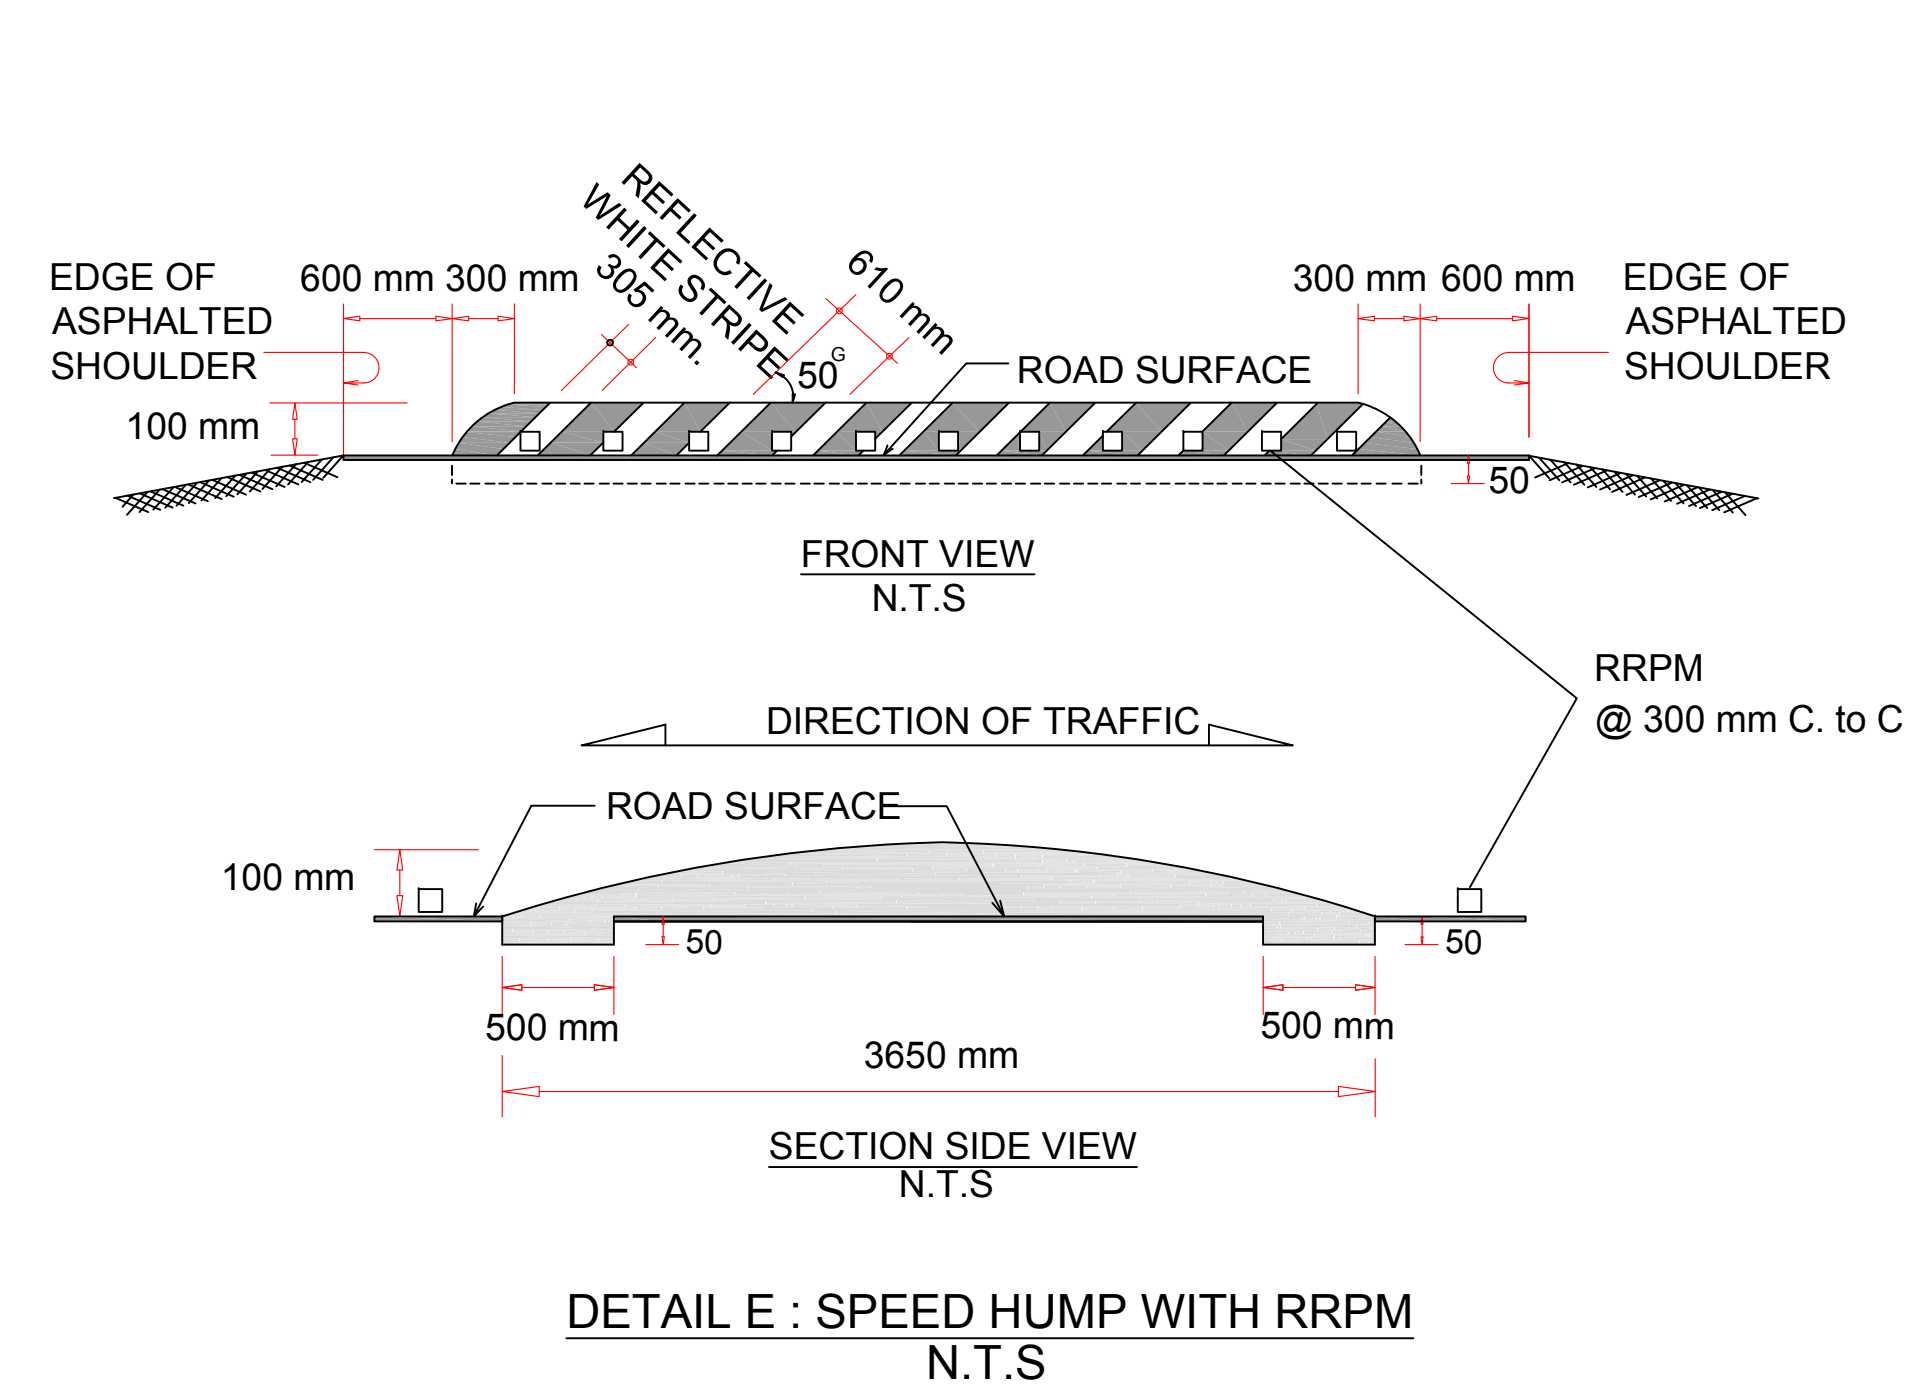

DETAIL E : SPEED HUMP WITH RRPM
N.T.S

- NOTES
1. ALL DIMENSIONS ARE IN METRIC UNITS, UNLESS OTHERWISE MENTIONED.
 2. RRPM (REFLECTIVE RAISED PAVEMENT MARKER) WITH SOLAR CELLS.
 3. THIS TYPICAL DETAIL IS VALID FOR DIVIDED HIGHWAYS AND TO BE ADJUSTED AS PER ACTUAL OPERATIONAL SPEED AND RESUBMITTED FOR APPROVAL .
 4. CHECKPOINT AREA MUST BE FURNISHED WITH STREET LIGHTING AS PER MOT STANDARDS (IF NO ELECTRICAL POWER IS AVAILABLE, SOLAR POWERED LIGHTS SHOULD BE PROVIDED.)
 5. THE SHOWN DETAILS IS FOR PERMANENT / INTERMITTENT OPERATION MODE USING STANDARD SIGNS.
 6. FOR INTERMITTENT OPERATION MODE, VMS SIGNAGE IS PREFERRED.
 7. FOLDABLE SIGNS SHOULD BE FLIPPED UP OR DOWN FOR NON-OPERATION PERIODS. SIGNS SHOULD BE FOLDED IN HALF AND BOLTED SECURELY TO THE SIGN SUPPORT.
 8. VMS SHOULD HAS THE ABILITY TO BE BLANK/DARK DURING NON-OPERATION PERIODS.
 9. THE SHOWN DETAIL IS VALID FOR OPERATION SPEED OF 120 KPH.
 10. THE CONTRACTOR SHOULD ACKNOWLEDGE TO MOT ALL OTHER REQUIRED PRECAUTIONS SHOULD BE TAKEN ON-SITE, PREPARING THE NECESSARY PROPOSALS FOR MOT APPROVAL.