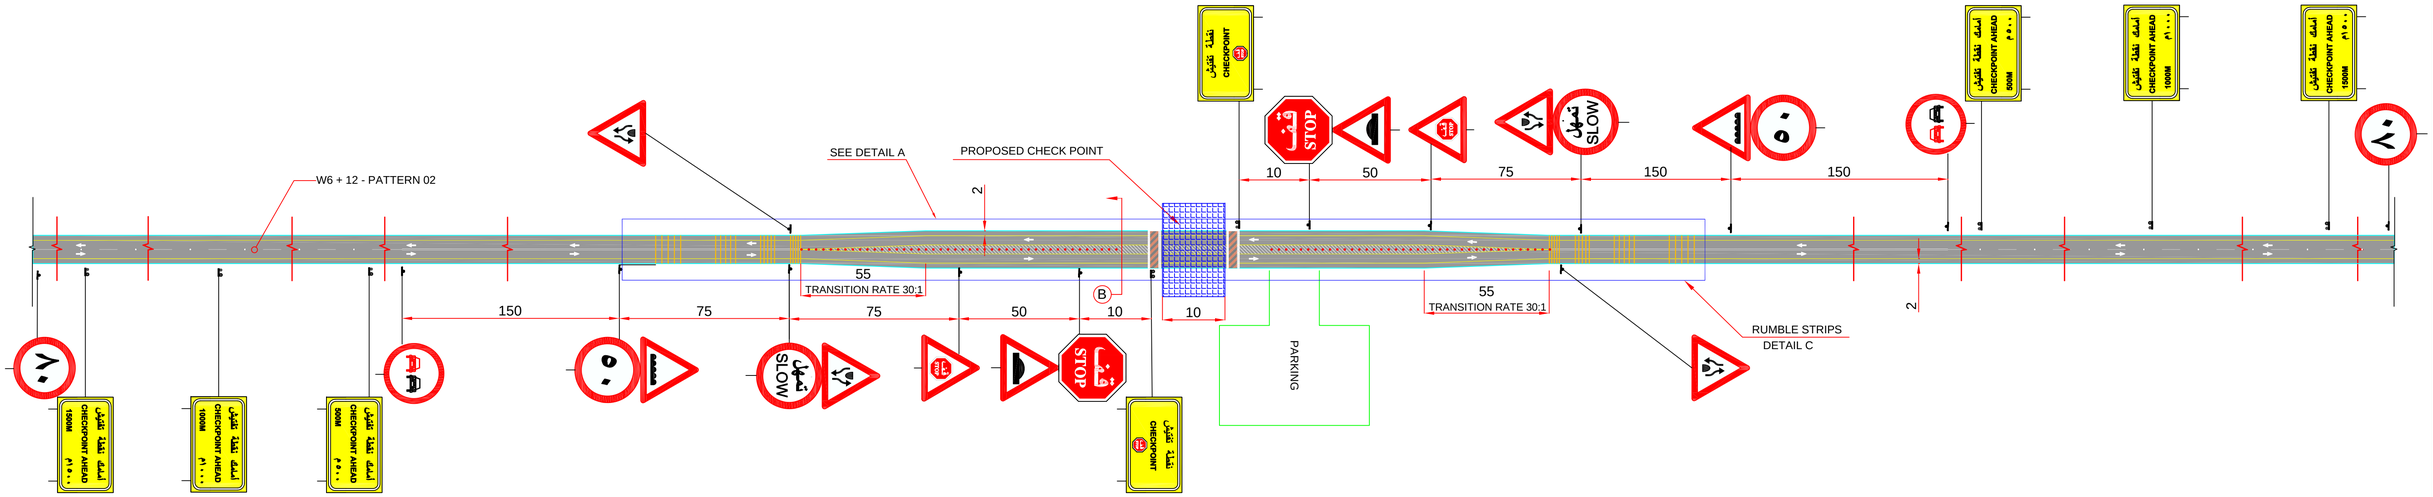

نقطـــة التفتيـــش الدائمـــة علـــي الطـــرق الســـريعة المفـــردة بتوســـعة فـــي قطـــاع الطـــريق

PERMANENT CHECK POINT AT SINGLE HIGHWAY WITH WIDENING
TYPE (E)
N.T.S

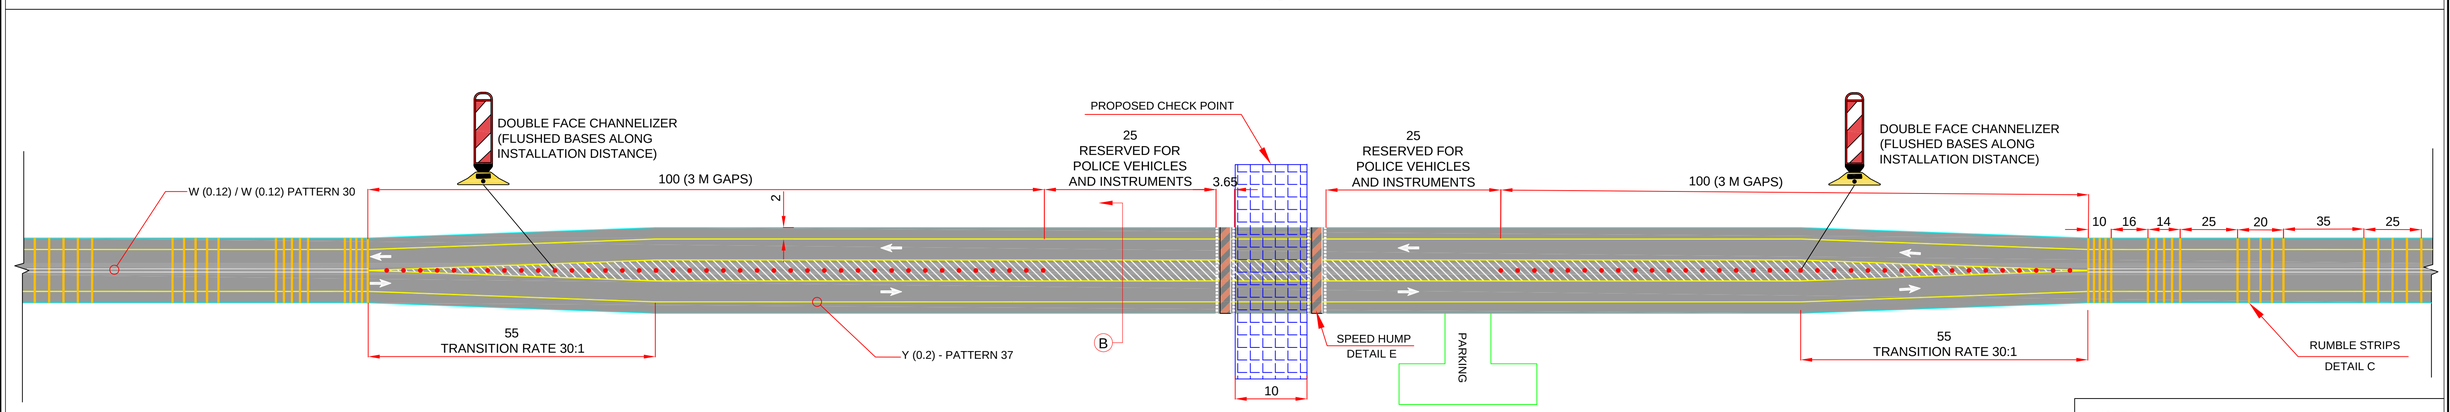

DETAIL A
N.T.S

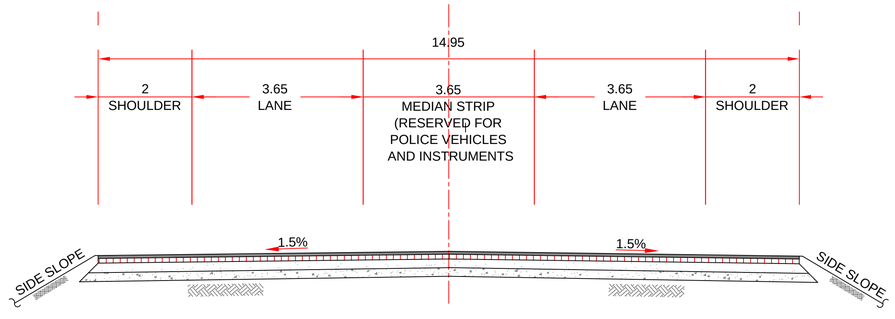

B PROPOSED CROSS SECTION
N.T.S

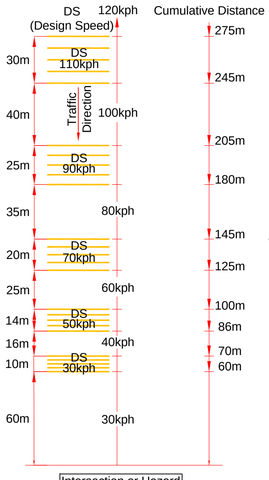

DETAIL C : RUMBLE STRIP
N.T.S

DS (kph)	Y (m)	Y/4 (m)
110	30	7.50
90	25	6.25
70	20	5.00
50	14	3.50
30	10	2.50

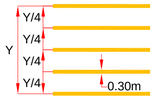

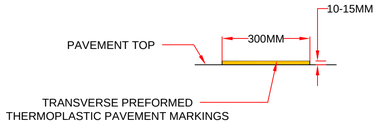

DETAIL D : THERMOPLASTIC MARKING DETAIL CROSS - SECTION
N.T.S

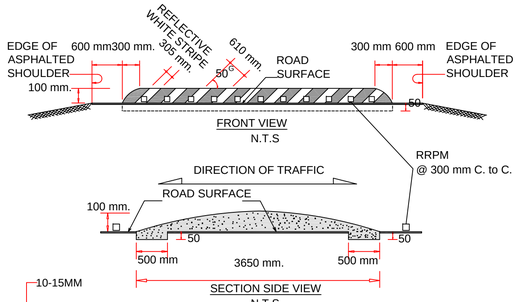

DETAIL E : SPEED HUMP W/ RRPM
N.T.S

NOTES

1. ALL DIMENSIONS ARE IN METRIC UNITS, UNLESS OTHERWISE MENTIONED.
2. RRPM (REFLECTIVE RAISED PAVEMENT MARKER) WITH SOLAR CELLS.
3. THIS TYPICAL DETAIL IS VALID FOR SINGLE HIGHWAY AND TO BE ADJUSTED AS PER ACTUAL OPERATIONAL SPEED AND RESUBMITTED FOR APPROVAL.
4. CHECKPOINT AREA MUST BE FURNISHED WITH STREET LIGHTING AS PER MOT STANDARDS (IF NO ELECTRICAL POWER IS AVAILABLE, SOLAR POWERED LIGHTS SHOULD BE PROVIDED.)
5. THE SHOWN DETAILS IS FOR PERMANENT OPERATION MODE USING STANDARD SIGNS.
6. THE CONTRACTOR SHOULD ACKNOWLEDGE TO MOT ALL OTHER REQUIRED PRECAUTIONS SHOULD BE TAKEN ON-SITE, PREPARING THE NECESSARY PROPOSALS FOR MOT APPROVAL.

KINGDOM OF SAUDI ARABIA

MINISTRY OF TRANSPORT

وزارة النقل
TRANSPORT MINISTRY

TITLE :

المخطـط النموذجـي-(ه) لنقطـة التفتيـش الدائمـة علـي الطـرق السـريعة المفـردة بتوسـعة فـي قطـاع الطـريق

TYPICAL SAFETY DEVICES AT APPROACHES TO PERMANENT CHECKPOINT AT SINGLE HIGHWAY WITH WIDENING -TYPE (E)

DRAWING NUMBER	DATE : DECEMBER 2018
RD1-MOT-RSD-DWG-1812-005	SHEET SIZE: A1