



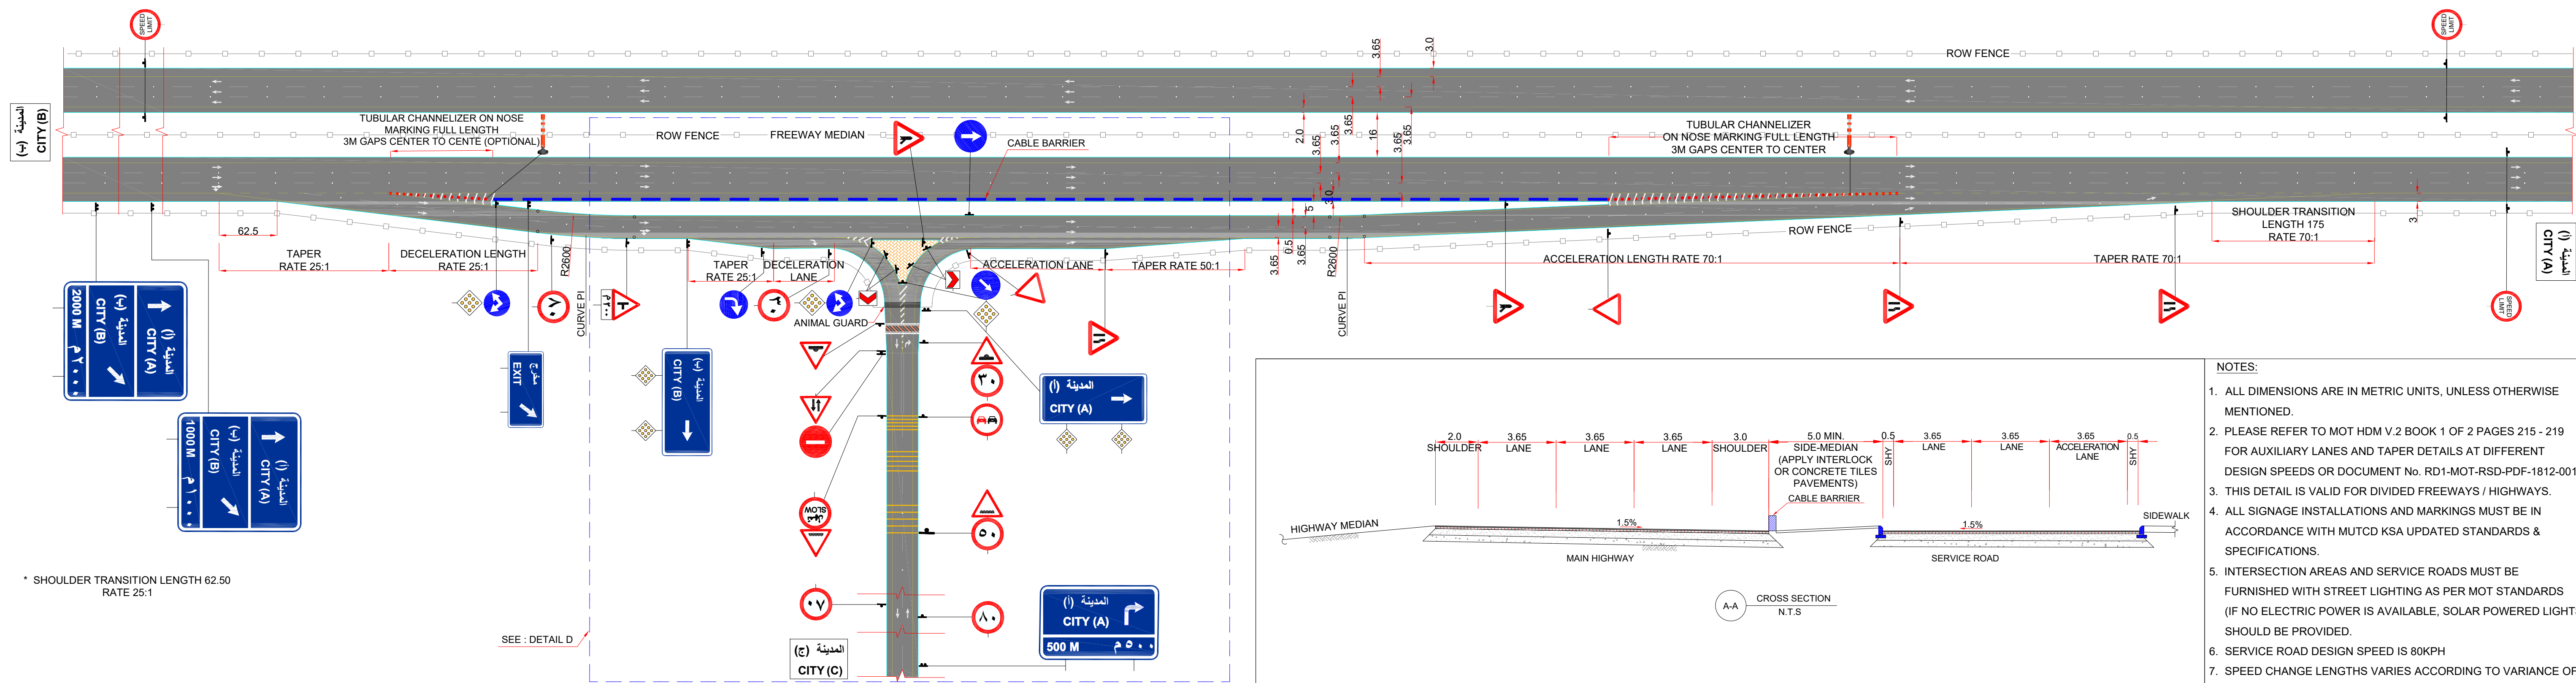


* SHOULDER TRANSITION LENGTH 62.50
RATE 25:1

SEE : DETAIL D

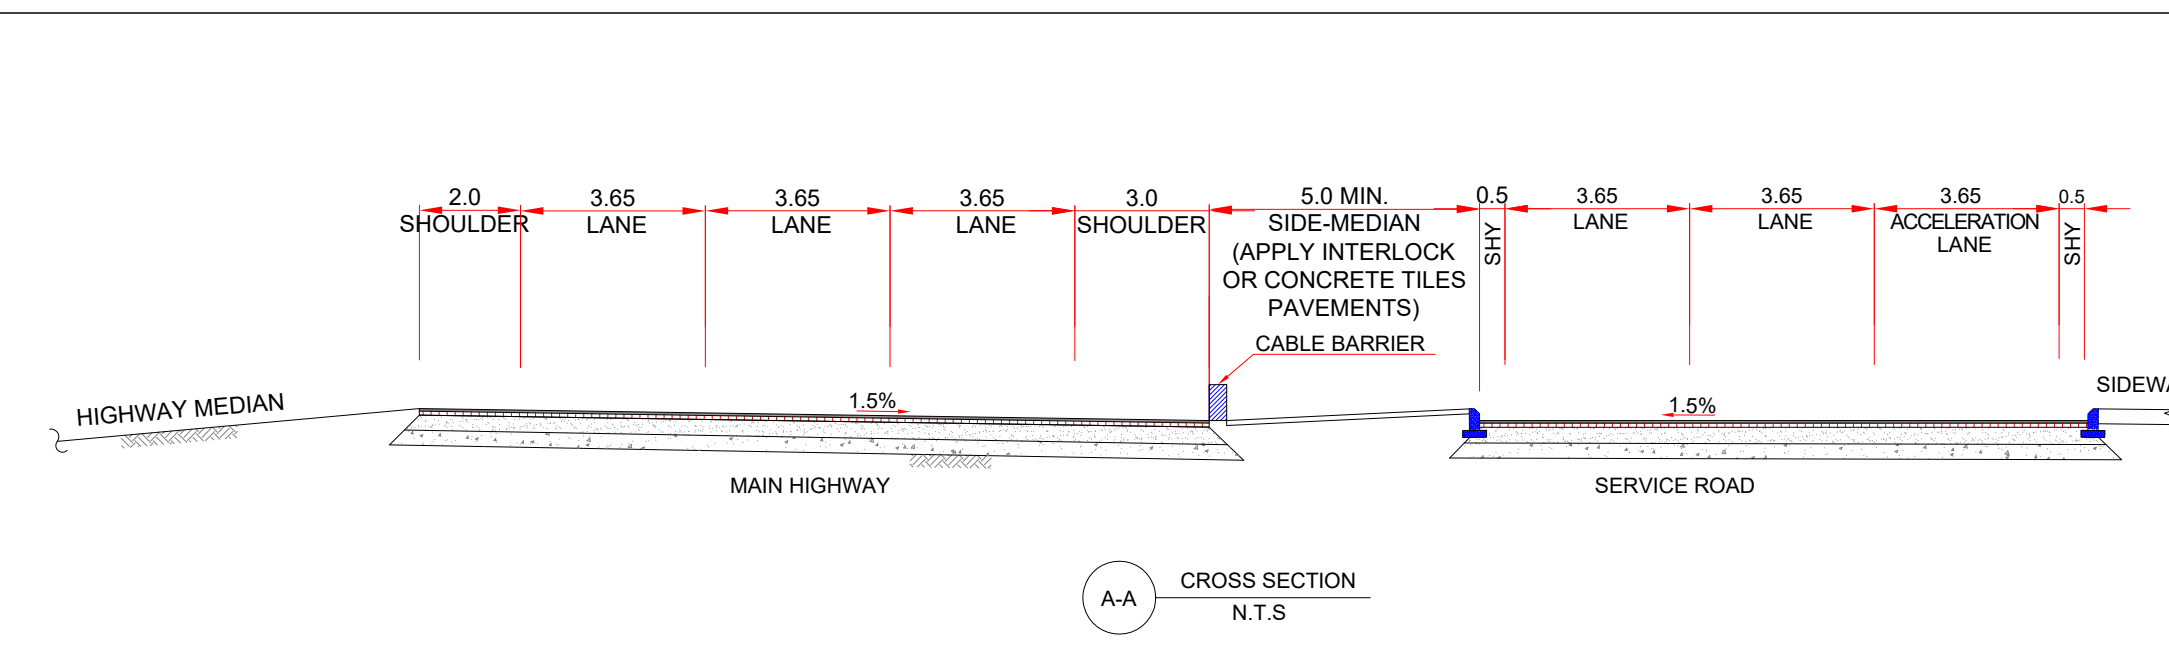


NOTES:


1. ALL DIMENSIONS ARE IN METRIC UNITS, UNLESS OTHERWISE MENTIONED.
2. PLEASE REFER TO MOT HDM V.2 BOOK 1 OF 2 PAGES 215 - 219 FOR AUXILIARY LANES AND TAPER DETAILS AT DIFFERENT DESIGN SPEEDS OR DOCUMENT No. RD1-MOT-RSD-PDF-1812-001.
3. THIS DETAIL IS VALID FOR DIVIDED FREEWAYS / HIGHWAYS.
4. ALL SIGNAGE INSTALLATIONS AND MARKINGS MUST BE IN ACCORDANCE WITH MUTCD KSA UPDATED STANDARDS & SPECIFICATIONS.
5. INTERSECTION AREAS AND SERVICE ROADS MUST BE FURNISHED WITH STREET LIGHTING AS PER MOT STANDARDS (IF NO ELECTRIC POWER IS AVAILABLE, SOLAR POWERED LIGHTS SHOULD BE PROVIDED).
6. SERVICE ROAD DESIGN SPEED IS 80KPH
7. SPEED CHANGE LENGTHS VARIES ACCORDING TO VARIANCE OF MAIN HIGHWAY DESIGN SPEED.
8. TRANSITION CURVES RADII MAY VARY TO CONFORM WITH DESIGN SPEED AND SUPERELEVATION REQUIREMENTS OF THE SERVICE ROAD HOWEVER, LARGER RADII WITH NO SUPERELEVATION REQUIRED ARE PREFERABLE AS SHOWN .
9. SIDE-MEDIAN SHOULD BE ALWAYS PROVIDED WITH APPROPRIATE BARRIER TYPE AS PER SPECS USING NECESSARY TERMINALS TREATMENT.
10. THE CONTRACTOR SHOULD ACKNOWLEDGE TO MOT ALL OTHER REQUIRED PRECAUTIONS SHOULD BE TAKEN ON-SITE. PREPARING THE NECESSARY PROPOSALS FOR MOT APPROVAL .
11. DO NOT TAKE ANY MEASUREMENTS FROM THIS DRAWING, THE DRAWING IS NOT TO SCALE.
12. ROW FENCE SHOULD BE PROVIDED HAVING THE APPROPRIATE CONNECTION WITH ACTUAL DESIGNED ANIMAL GUARD LOCATION.
13. SERVICE ROAD SHOULD BE CURBED TO CONNECT WITH URBAN/ DOMESTIC ROAD NETWORK.
14. RIGHT TURNS RADIUS FOR SINGLE ROAD SHOULD FULFILL THE GEOMETRIC DESIGN REQUIREMENTS FOR 30 KPH SPEED AT LEAST.
15. INTERSECTION'S TRIANGULAR ISLAND SHOULD BE RAISED (CURBED) BY + 0.15M.

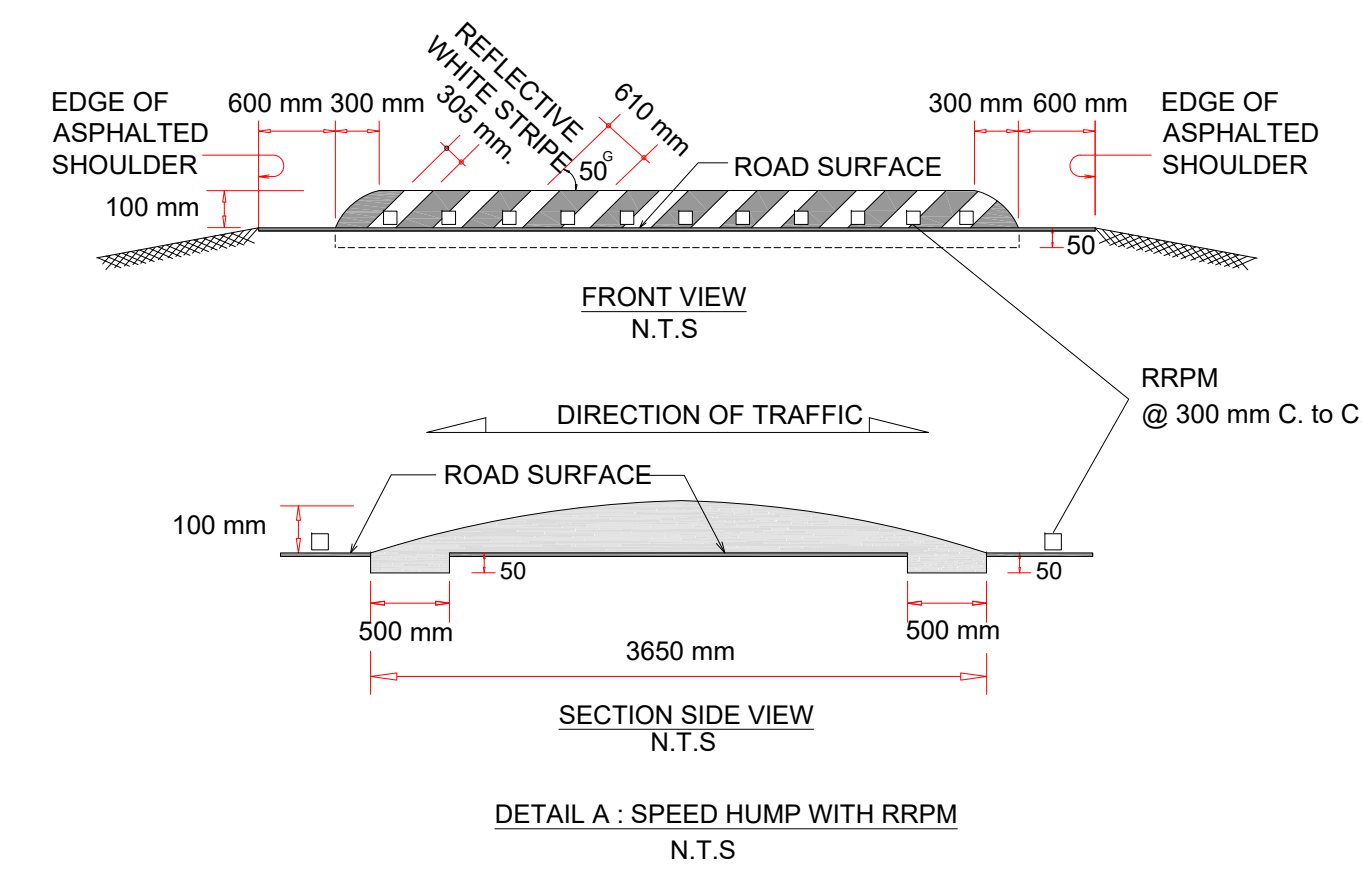


DETAIL A : SPEED HUMP WITH RRPM
N.T.S

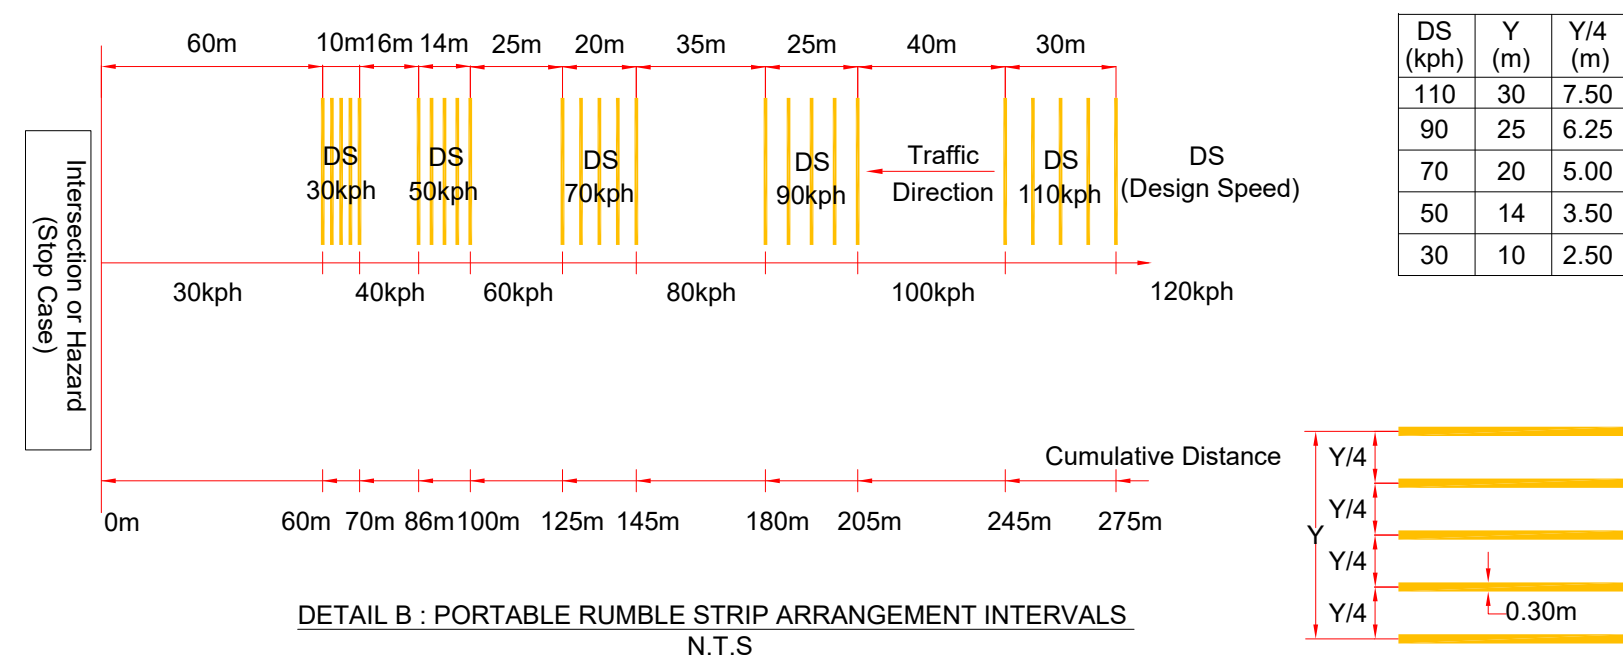

DETAIL B : PORTABLE RUMBLE STRIP ARRANGEMENT INTERVALS
N.T.S

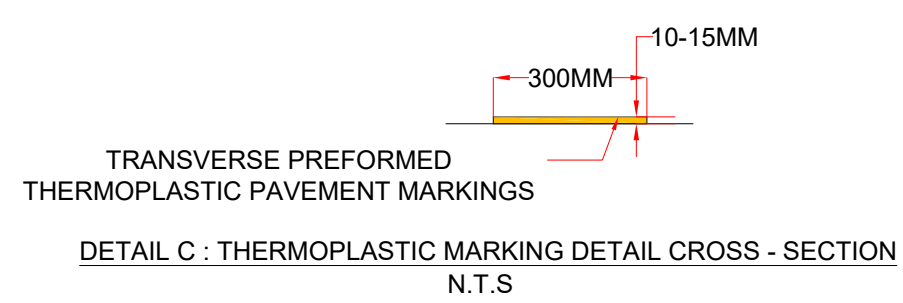

DETAIL C : THERMOPLASTIC MARKING DETAIL CROSS - SECTION
N.T.S

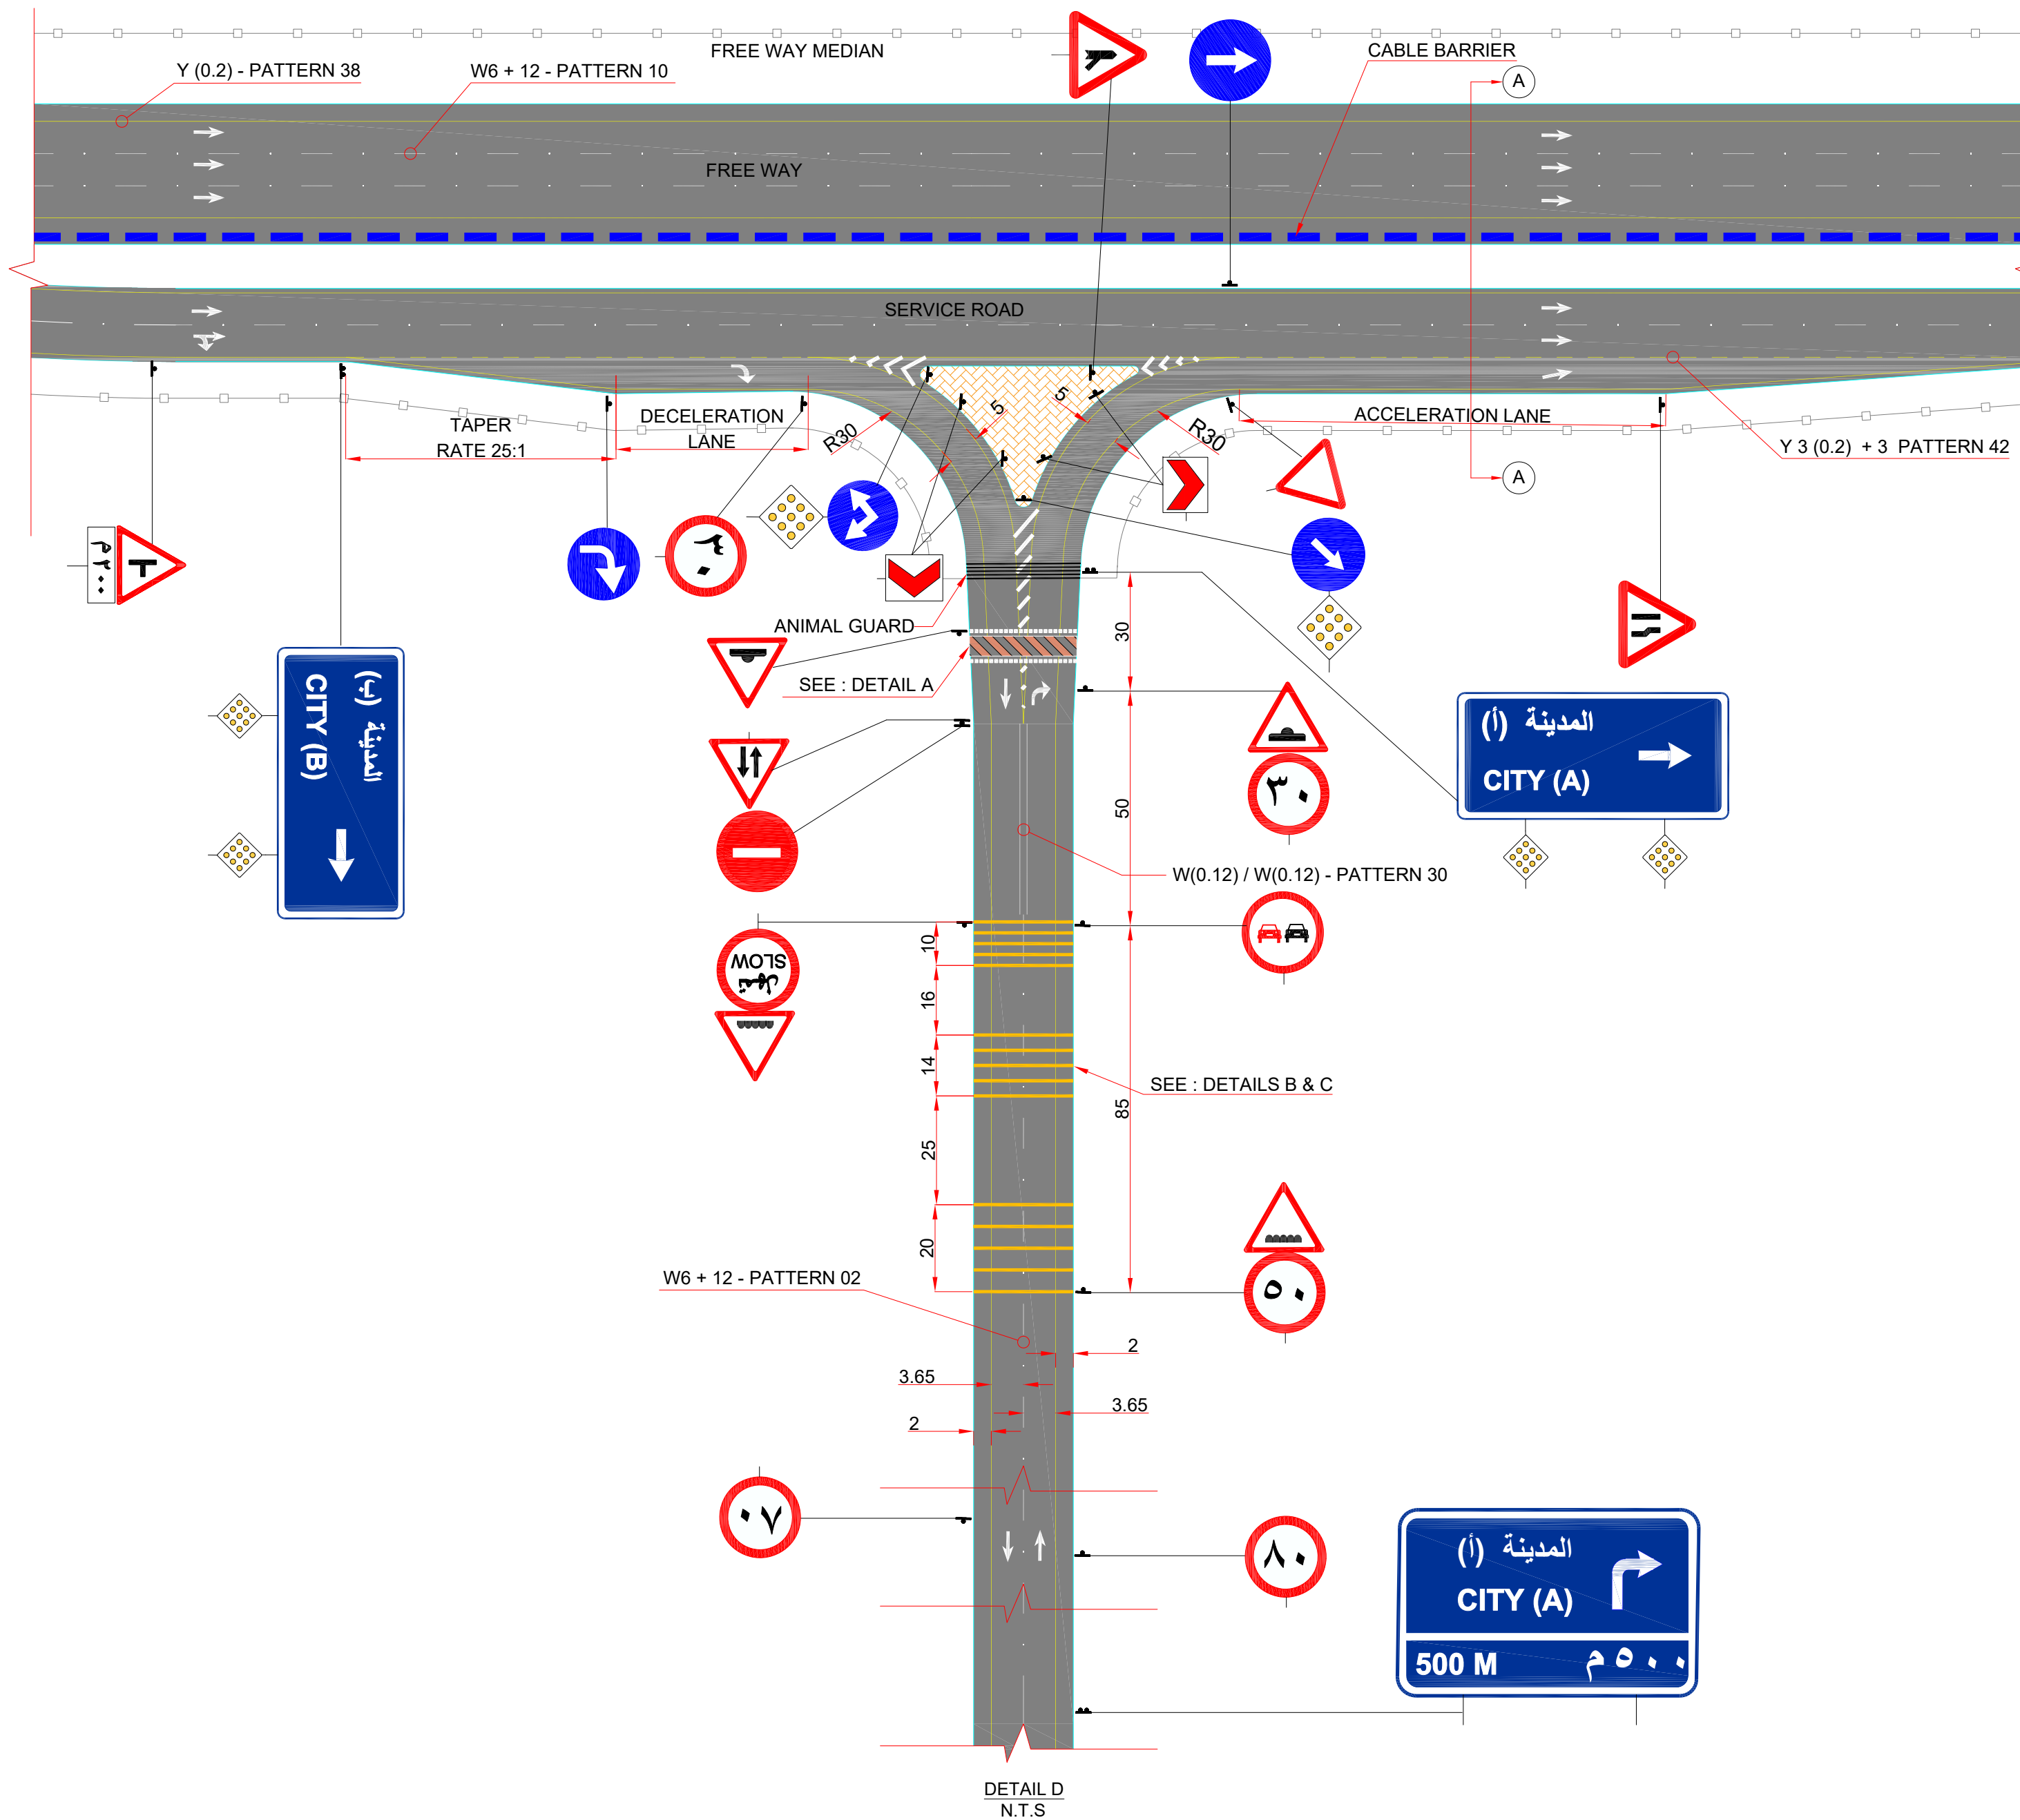

DETAIL D
N.T.S

KINGDOM OF SAUDI ARABIA
MINISTRY OF TRANSPORT



TITLE : المخطط النموذجي لربط طريق فرعي مع طريق -ر بواسطة طريق خدمة
TYPICAL CONNECTION DETAILS BETWEEN BRANCH ROAD AND DIVIDED FREE WAY THROUGH SERVICE ROAD

DRAWING NUMBER	DATE : JANUARY 2019
RD1-MOT-RSD-DWG-1901-012	SHEET SIZE: A1