
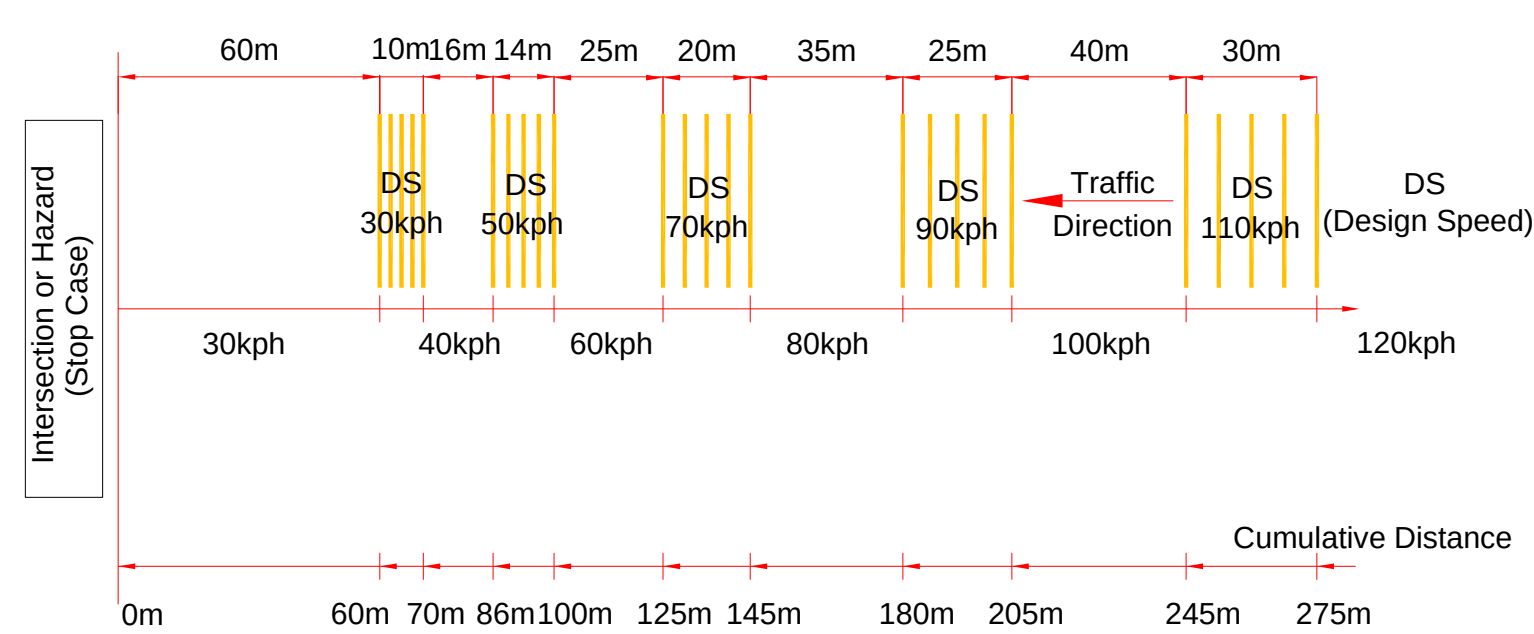
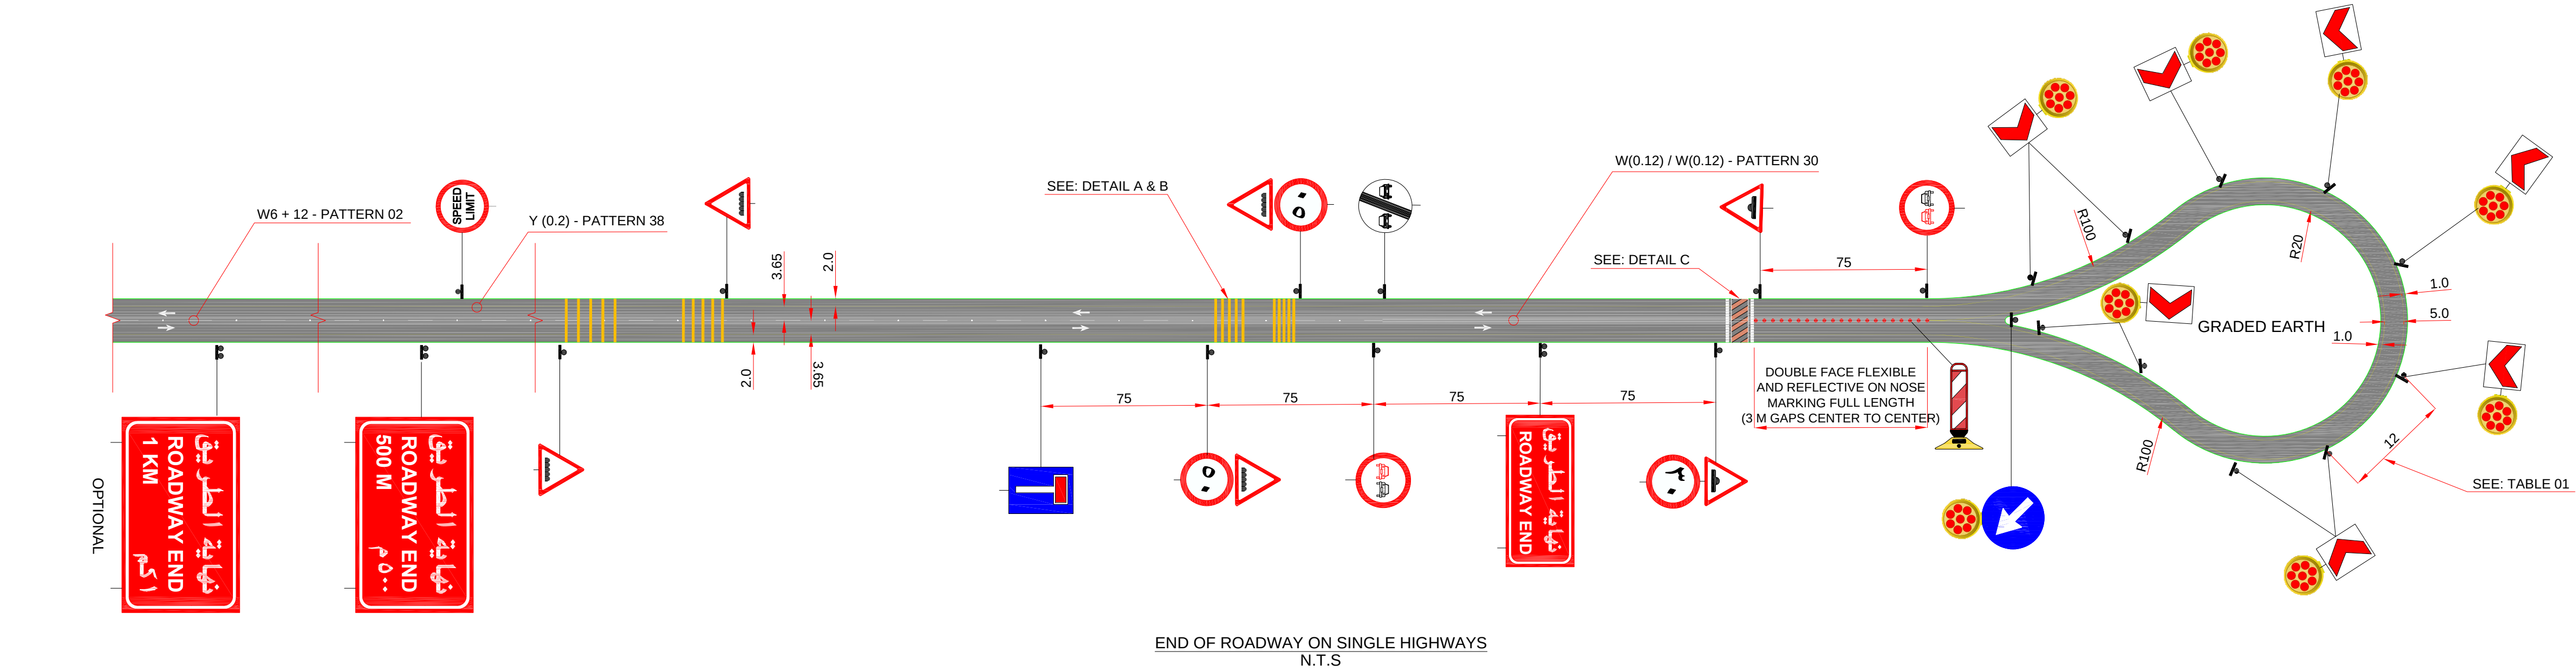


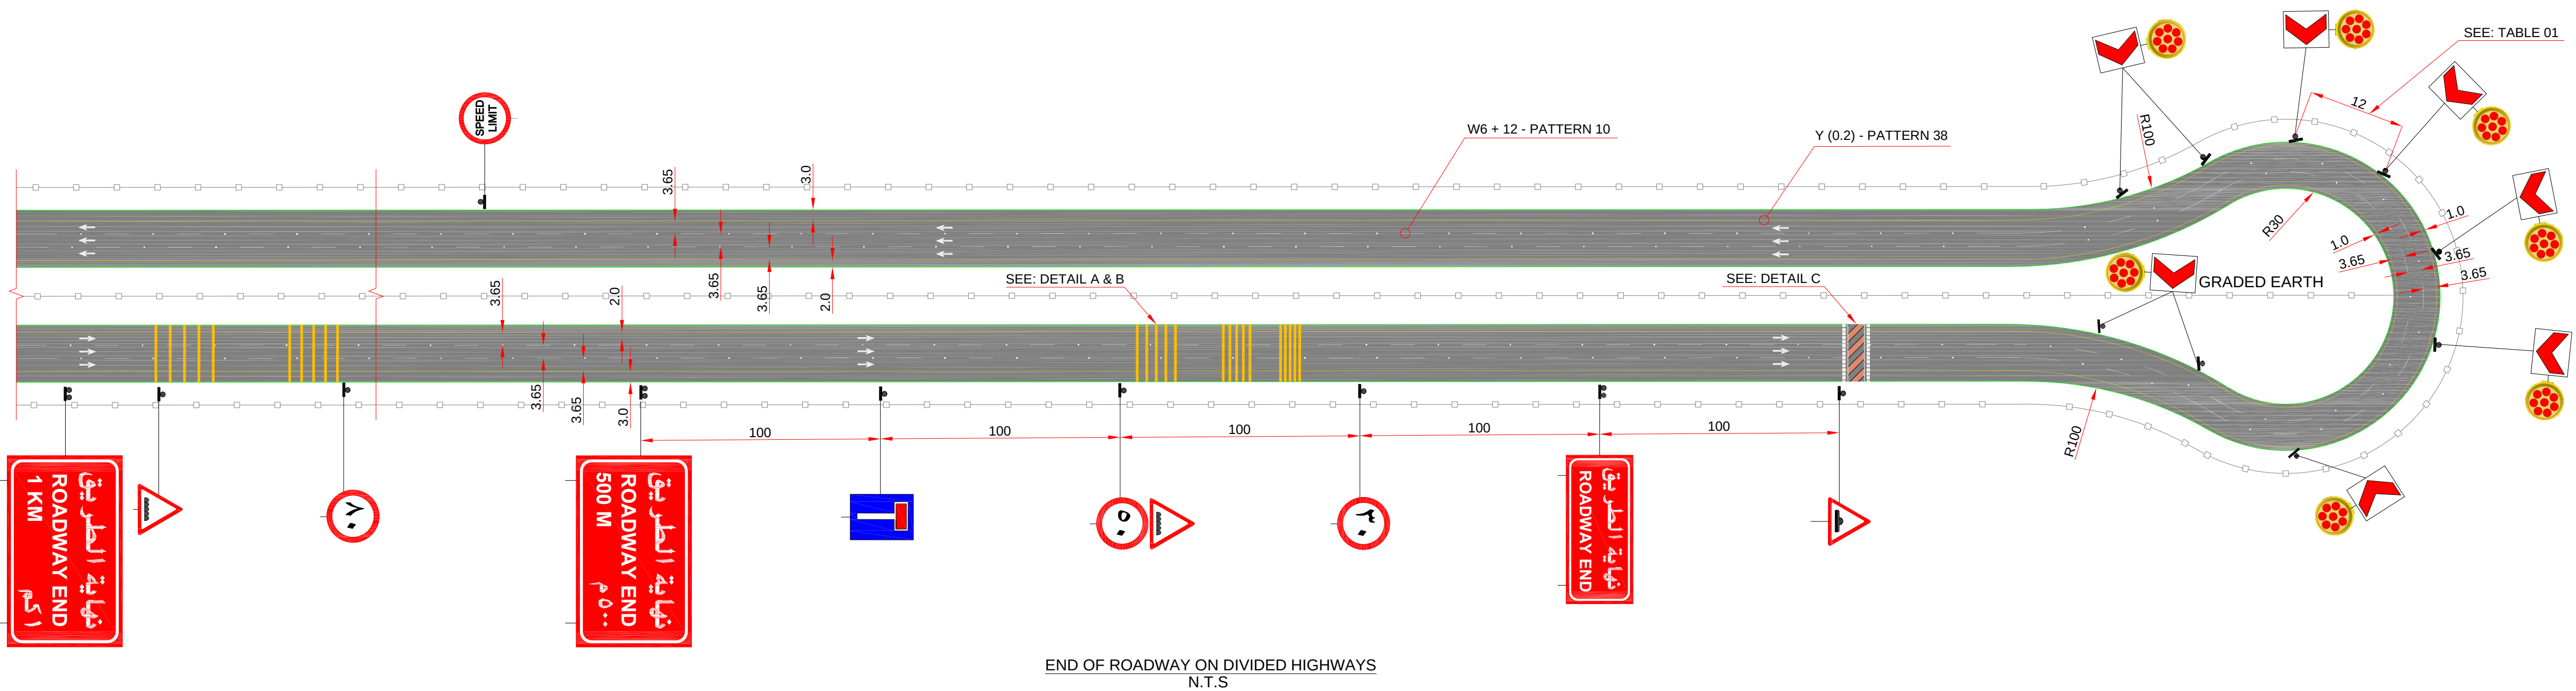

DS (kph)	Y (m)	Y/4 (m)
110	30	7.50
90	25	6.25
70	20	5.00
50	14	3.50
30	10	2.50


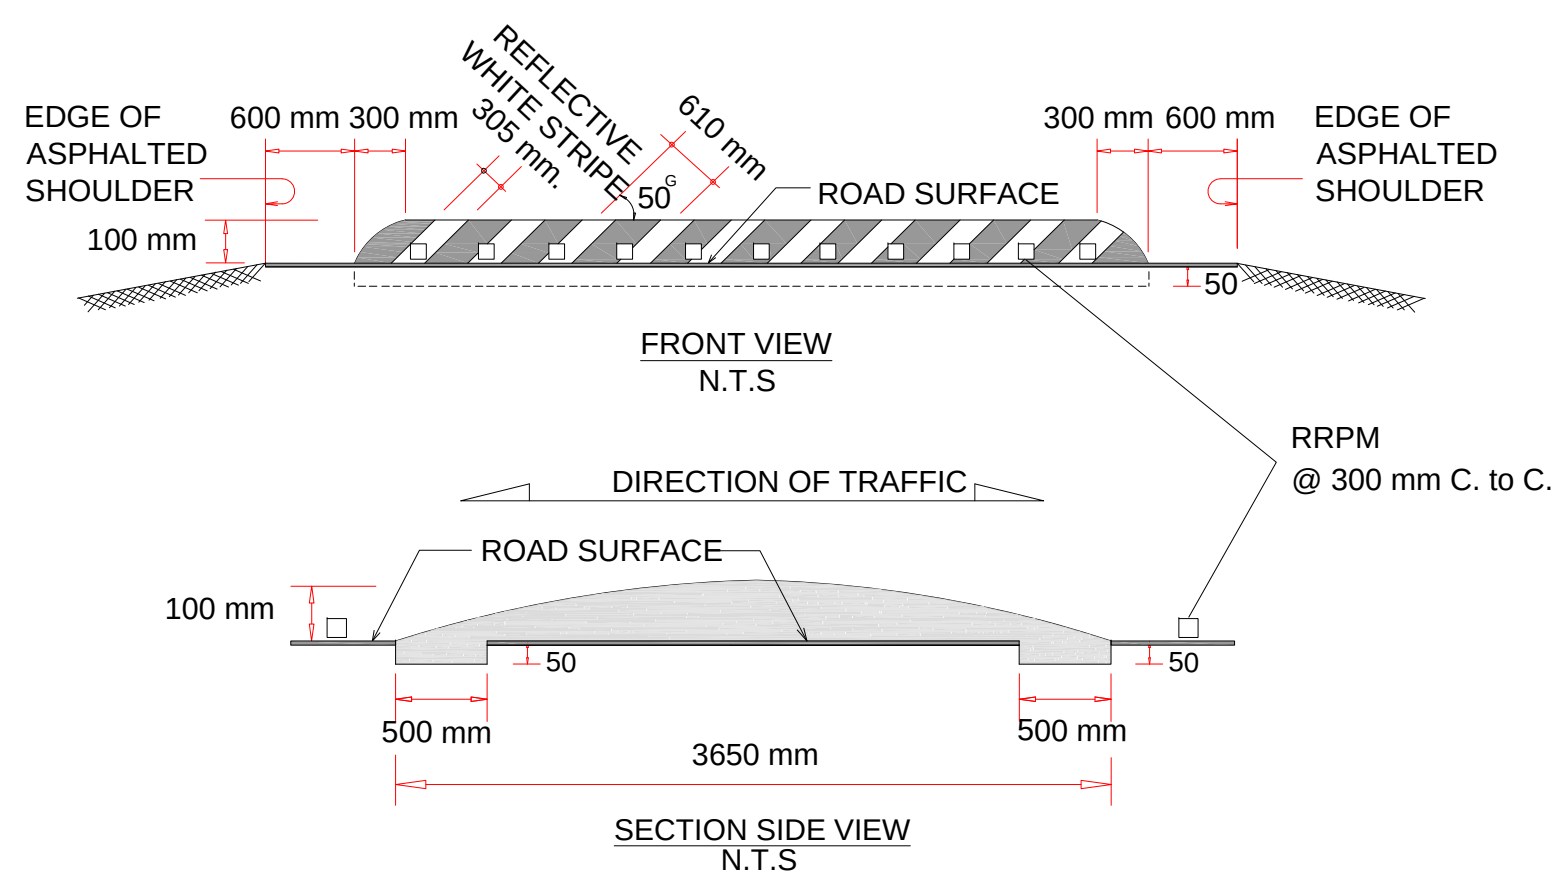


TABLE 01:
CHEVRON ALIGNMENT SIGN SPACING

POSTED SPEED (KM/HR)	CURVE RADIUS (M)	SIGN SPACING (M)
30 OR LESS	60 OR LESS	12
31 - 50	61 - 120	24
51 - 70	120 - 215	36
71 - 90	215 - 380	48
OVER 90	380 - 1000	60

- NOTES:
1. ALL DIMENSIONS ARE IN METRIC UNITS, UNLESS OTHERWISE MENTIONED.
 2. ALL SIGNAGE INSTALLATIONS AND MARKINGS MUST BE IN ACCORDANCE WITH MUTCD KSA UPDATED STANDARDS & SPECIFICATIONS.
 3. THE CONTRACTOR SHOULD ACKNOWLEDGE TO MOT ALL OTHER REQUIRED PRECAUTIONS SHOULD BE TAKEN ON-SITE, PREPARING THE NECESSARY PROPOSALS FOR MOT APPROVAL .
 4. DO NOT TAKE ANY MEASUREMENTS FROM THIS DRAWING, THE DRAWING IS NOT TO SCALE.
 5. THE SHOWN DETAIL IS VALID FOR DIVIDED AND SINGLE HIGHWAYS WITH VARIOUS OPERATION SPEED.

KINGDOM OF SAUDI ARABIA
MINISTRY OF TRANSPORT

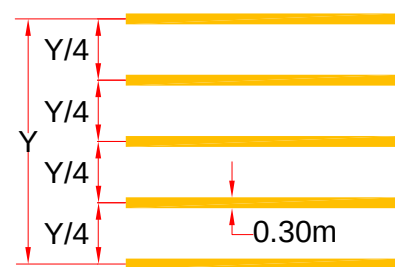

TITLE :
المخطط النموذجي لطرق الغير نافذة
TYPICAL DETAILS END OF ROADWAY

DRAWING NUMBER
RD1-MOT-RSD-DWG-1903-044

DATE : MARCH 2019
SHEET SIZE: A1