
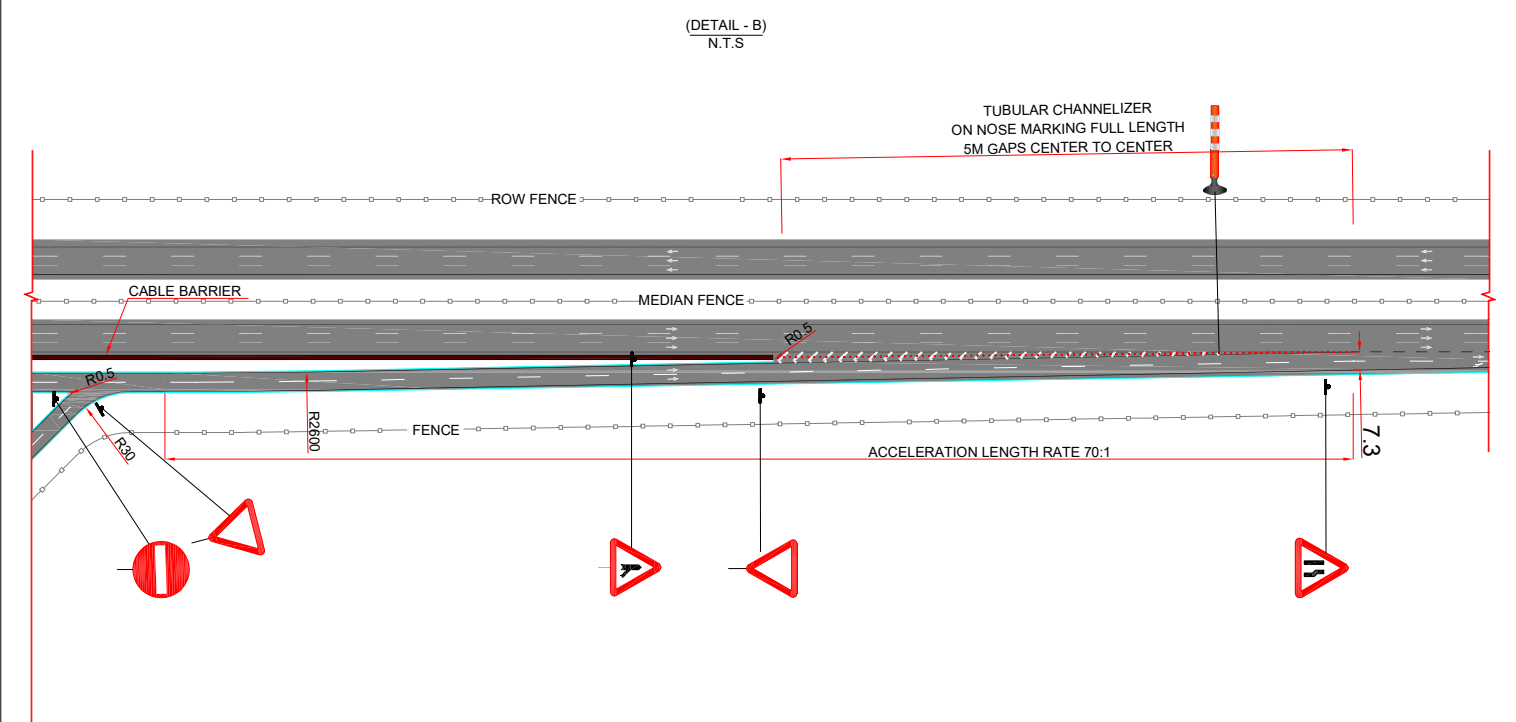
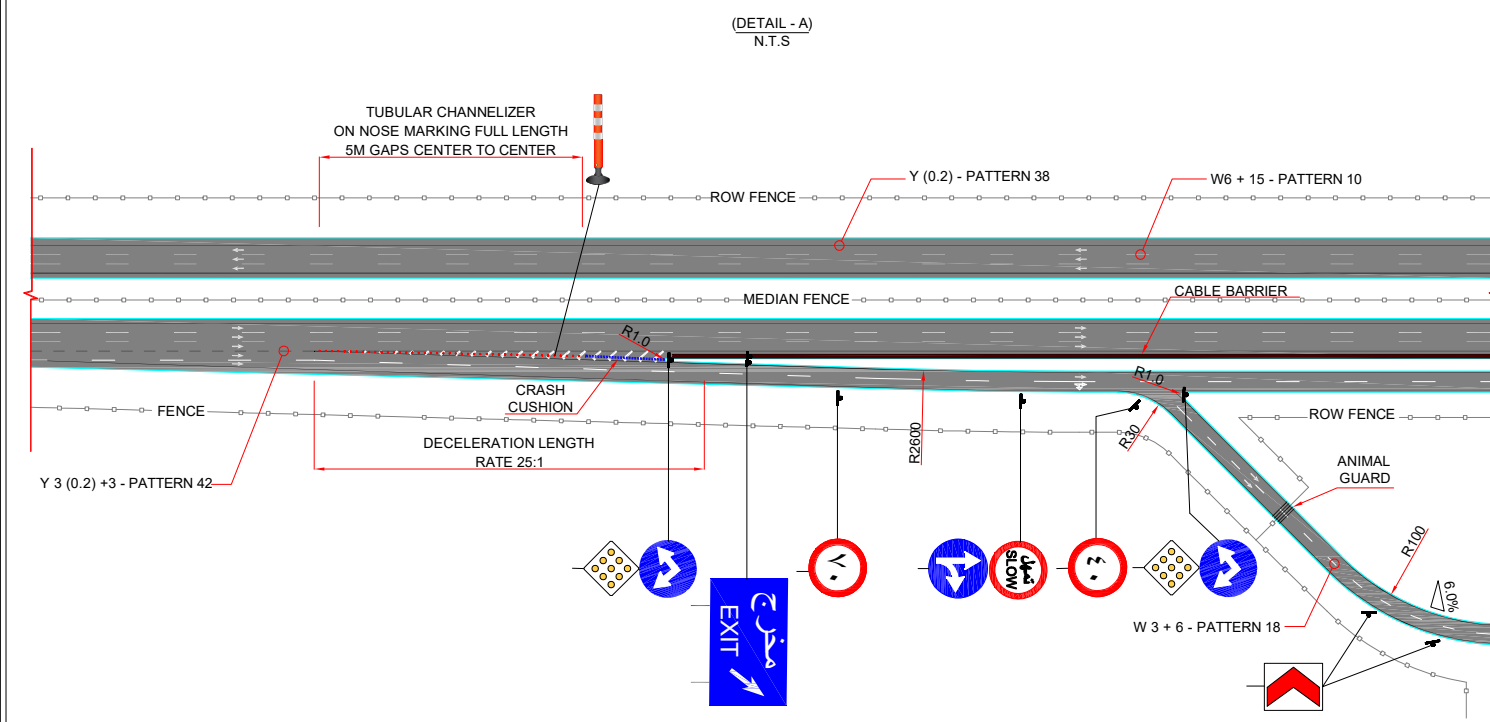


NOTES:

- ALL DIMENSIONS ARE IN METRIC UNITS, UNLESS OTHERWISE MENTIONED.
- PLEASE REFER TO MOT HDM V.2 BOOK 1 OF 2 PAGES 215 - 219 FOR AUXILIARY LANES AND TAPER DETAILS AT DIFFERENT DESIGN SPEEDS.
- THIS DETAIL IS VALID FOR DIVIDED FREEWAYS / HIGHWAYS.
- SERVICE SYMBOLS ON EXIT SIGNS VARY AS PER AVAILABILITY ON SITE.
- FENCE SHOULD BE CONTINUOUS AROUND THE PETROL STATION, ROW EDGES AND IN THE MEDIAN TO PREVENT ANIMAL CROSSING AND OFF-ROAD VEHICLES ENTRY/EXIT.
- ALL SIGNAGE INSTALLATIONS AND MARKINGS MUST BE IN ACCORDANCE WITH MUTCD KSA UPDATE STANDARDS & SPECIFICATIONS.
- BUFFER DISTANCE CROSS SLOPE SHALL BE DETERMINED BY THE CONSULTANT ACCORDING TO SITE DRAINAGE STUDY.
- INTERSECTION AREAS AND SERVICE ROADS MUST BE FURNISHED WITH STREET LIGHTING AS PER MOT STANDARDS (IF NO ELECTRIC POWER IS AVAILABLE, SOLAR POWERED LIGHTS SHOULD BE PROVIDED.)

- BUFFER DISTANCE OF 100 M COULD BE REDUCED TO 30 M MINIMUM ONLY (MEASURED FROM ROW) IN MOUNTAINOUS AREAS AFTER COORDINATION AND APPROVAL OF RELEVANT MOT BRANCH ENGINEER WITHIN THE AREA.
- SERVICE ROAD DESIGN SPEED IS 80KPH, AND FOR PETROL STATION ACCESS IS 50KPH IN THE SHOWN SCHEME, WHILE POSTED SPEEDS ARE AS SHOWN.
- SPEED CHANGE LENGTHS VARIES ACCORDING TO VARIANCE OF MAIN HIGHWAY DESIGN SPEED.
- TRANSITION CURVES RADII MAY VARY TO CONFORM WITH DESIGN SPEED AND SUPERELEVATION REQUIREMENTS OF THE SERVICE ROAD HOWEVER, LARGER RADII WITH NO SUPERELEVATION REQUIRED ARE PREFERABLE AS SHOWN .
- SIDE-MEDIAN SHOULD BE ALWAYS PROVIDED WITH APPROPRIATE BARRIER TYPE AS PER SPECS USING NECESSARY TERMINALS TREATMENT.
- THE CONTRACTOR SHOULD ACKNOWLEDGE TO MOT ALL OTHER REQUIRED PRECAUTIONS SHOULD BE TAKEN ON-SITE, PREPARING THE NECESSARY PROPOSALS FOR MOT APPROVAL .
- DO NOT TAKE ANY MEASUREMENTS FROM THIS DRAWING, THE DRAWING IS NOT TO SCALE.

KINGDOM OF SAUDI ARABIA
MINISTRY OF TRANSPORT

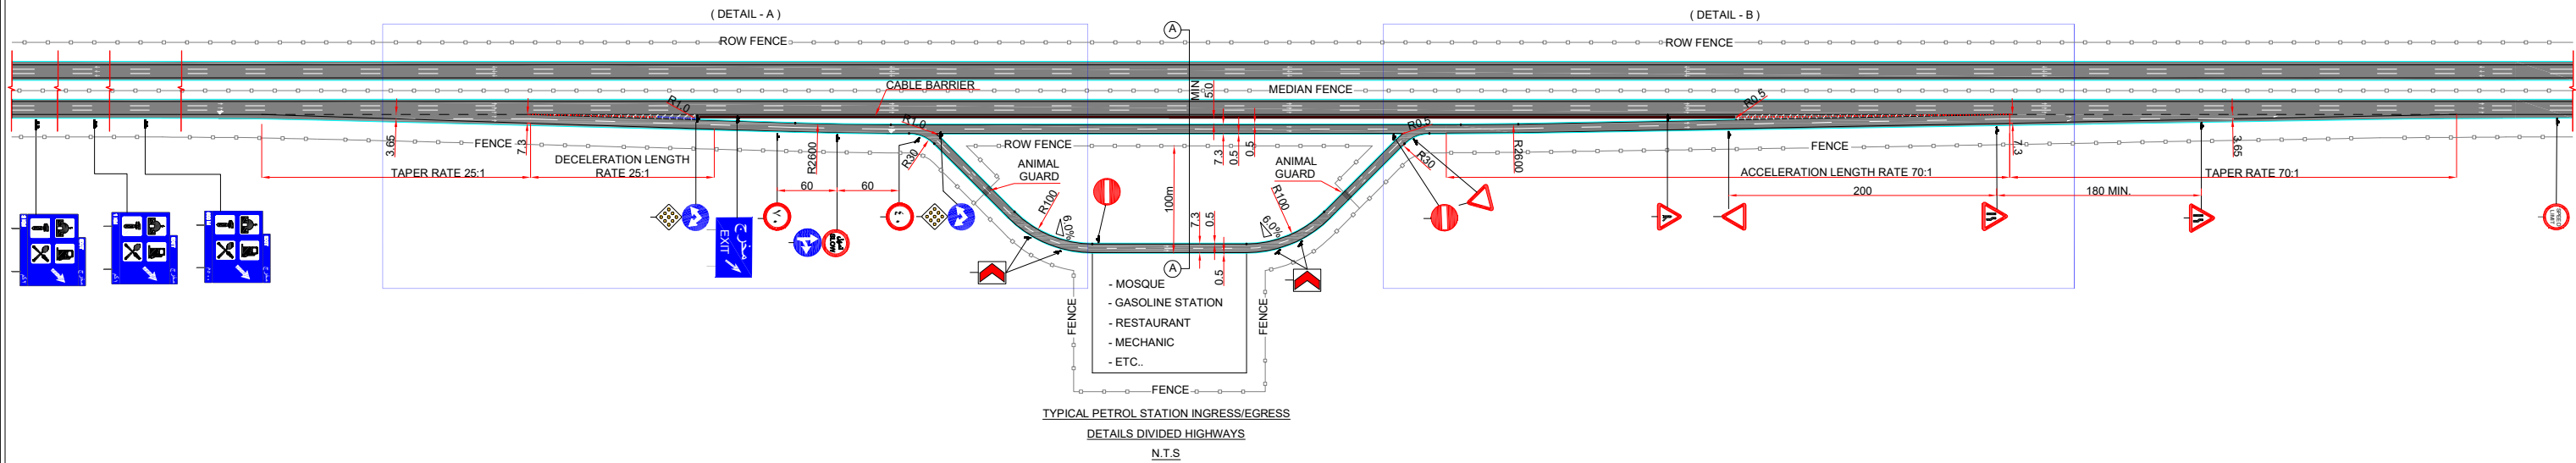

TITLE :
المخطط النموذجي لمداخل ومخارج محطة خدمات علي
الطرق السريعة المزدوجة
TYPICAL SERVICE STATION INGRESS / EGRESS
DETAILS ON DIVIDED HIGHWAYS

DRAWING NUMBER DATE : DECEMBER 2018

RD1-MOT-RSD-DWG-1812-007 SHEET SIZE: A1