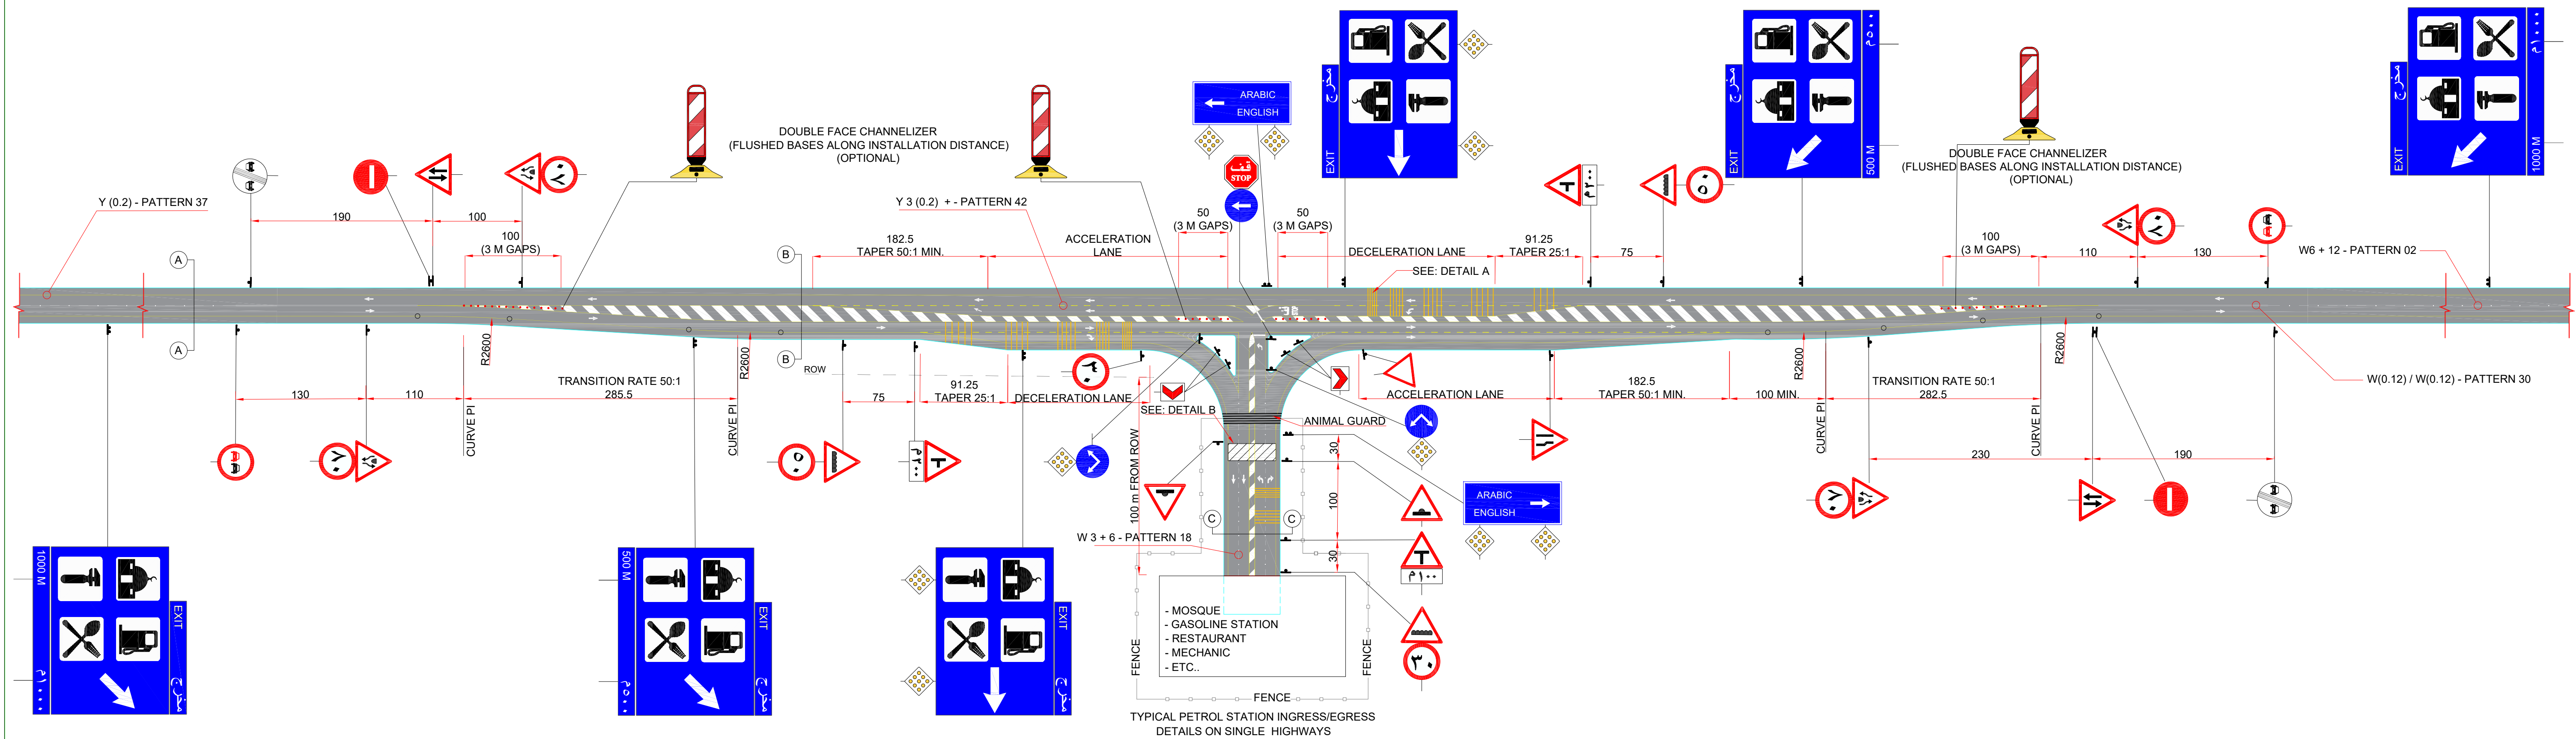


NOTES:

- ALL DIMENSIONS ARE IN METRIC UNITS, UNLESS OTHERWISE MENTIONED.
- PLEASE REFER TO MOT HDM V.2 BOOK 1 OF 2 PAGES 215 - 219 FOR AUXILIARY LANES AND TAPER DETAILS AT DIFFERENT DESIGN SPEEDS.
- SERVICE SYMBOLS ON EXIT SIGNS VARY AS PER AVAILABILITY ON SITE.
- FENCE SHOULD BE CONTINUOUS AROUND THE PETROL STATION AND CLOSING CONNECTED TO THE ANIMAL GUARD.
- ALL SIGNAGE INSTALLATIONS MUST BE IN ACCORDANCE WITH MUTCD KSA STANDARDS & SPECIFICATIONS.
- SPEED CHANGE LANE LENGTHS VARIES ACCORDING TO VARIANCE OF HIGHWAY DESIGN SPEED.
- INTERSECTION AREA MUST BE FURNISHED WITH STREET LIGHTING AS PER MOT STANDARDS (IF NO ELECTRIC POWER IS AVAILABLE, SOLAR POWERED LIGHTS SHOULD BE PROVIDED).
- BUFFER DISTANCE OF 100 M COULD BE REDUCED TO 30 M MINIMUM ONLY (MEASURED FROM ROW) IN MOUNTAINOUS AREAS AFTER COORDINATION AND APPROVAL OF RELEVANT MOT BRANCH ENGINEER WITHIN THE AREA .
- RIGHT AND LEFT TURNS RADIUS WITH IN THE INTERSECTION SHOULD FULFILL THE GEOMETRIC DESIGN REQUIREMENTS FOR 30 KPH SPEED.
- THE CONTRACTOR SHOULD ACKNOWLEDGE TO MOT ALL OTHER REQUIRED PRECAUTIONS SHOULD BE TAKEN ON-SITE, PREPARING THE NECESSARY PROPOSALS FOR MOT APPROVAL.
- THE SHOWN DETAIL IS VALID FOR SINGLE HIGHWAYS WITH VARIOUS OPERATION SPEEDS.
- DO NOT TAKE ANY MEASUREMENTS FROM THIS DRAWING, THE DRAWING IS NOT TO SCALE.

KINGDOM OF SAUDI ARABIA

MINISTRY OF TRANSPORT

TITLE :

المخطط النموذجي لمدخل ومخرج محطة خدمات على الطرق السريعة المفردة

TYPICAL SERVICE STATION INGRESS/EGRESS DETAILS ON SINGLE HIGHWAYS

DRAWING NUMBER

DATE : DECEMBER 2018

RD1-MOT-RSD-DWG-1812-008

SHEET SIZE: A1