
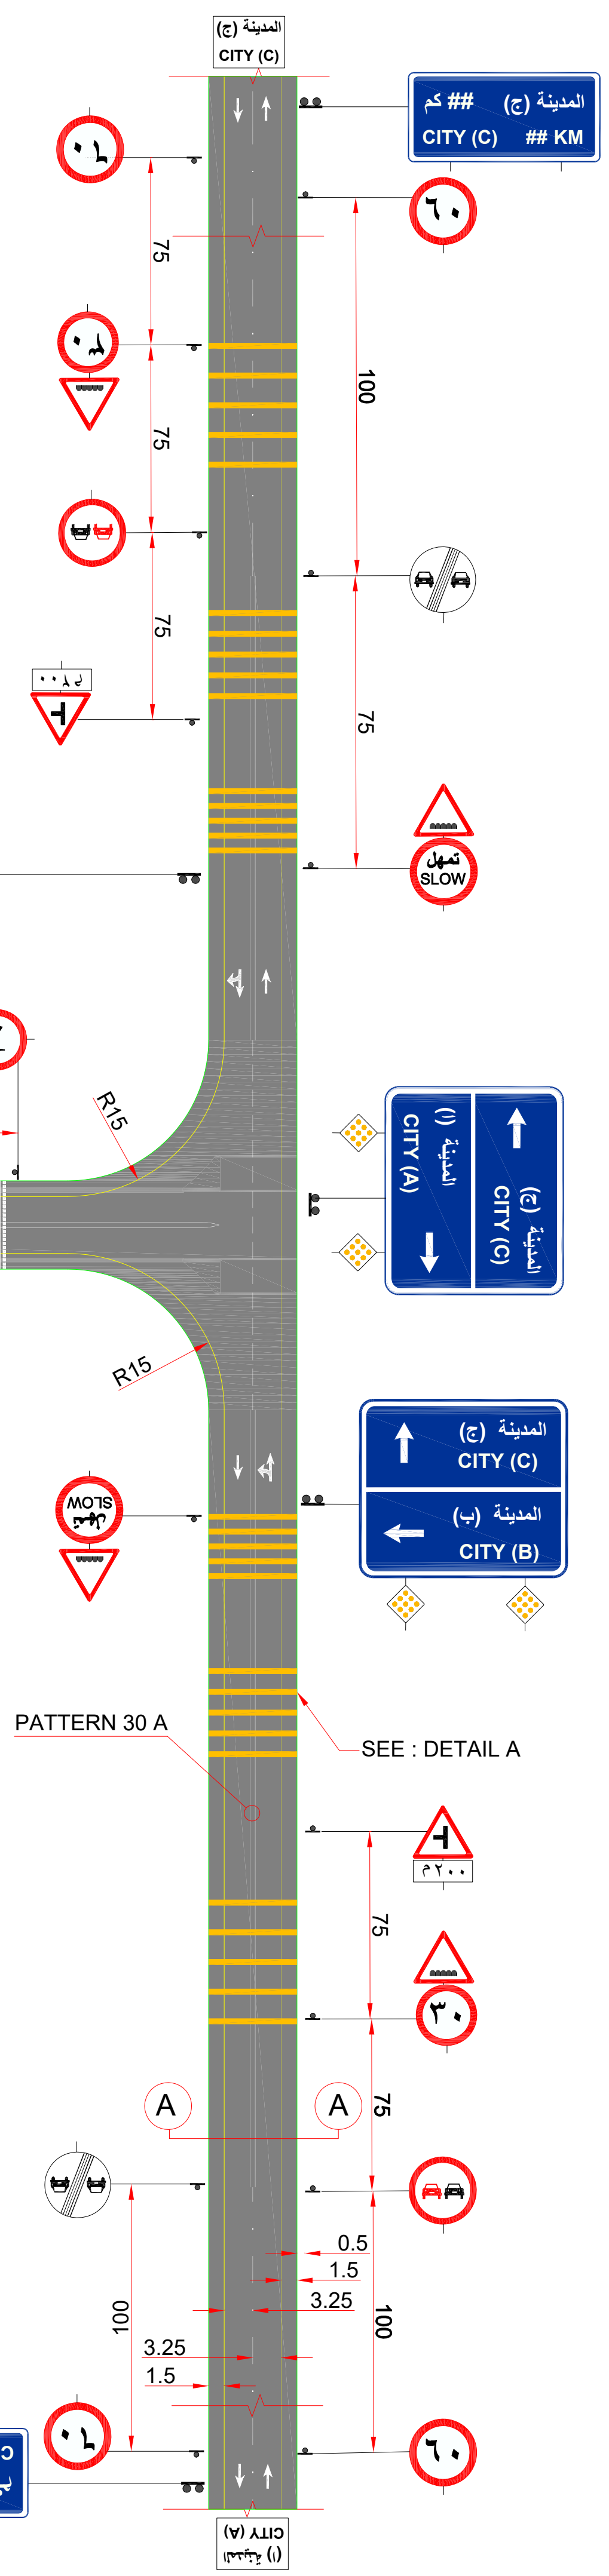
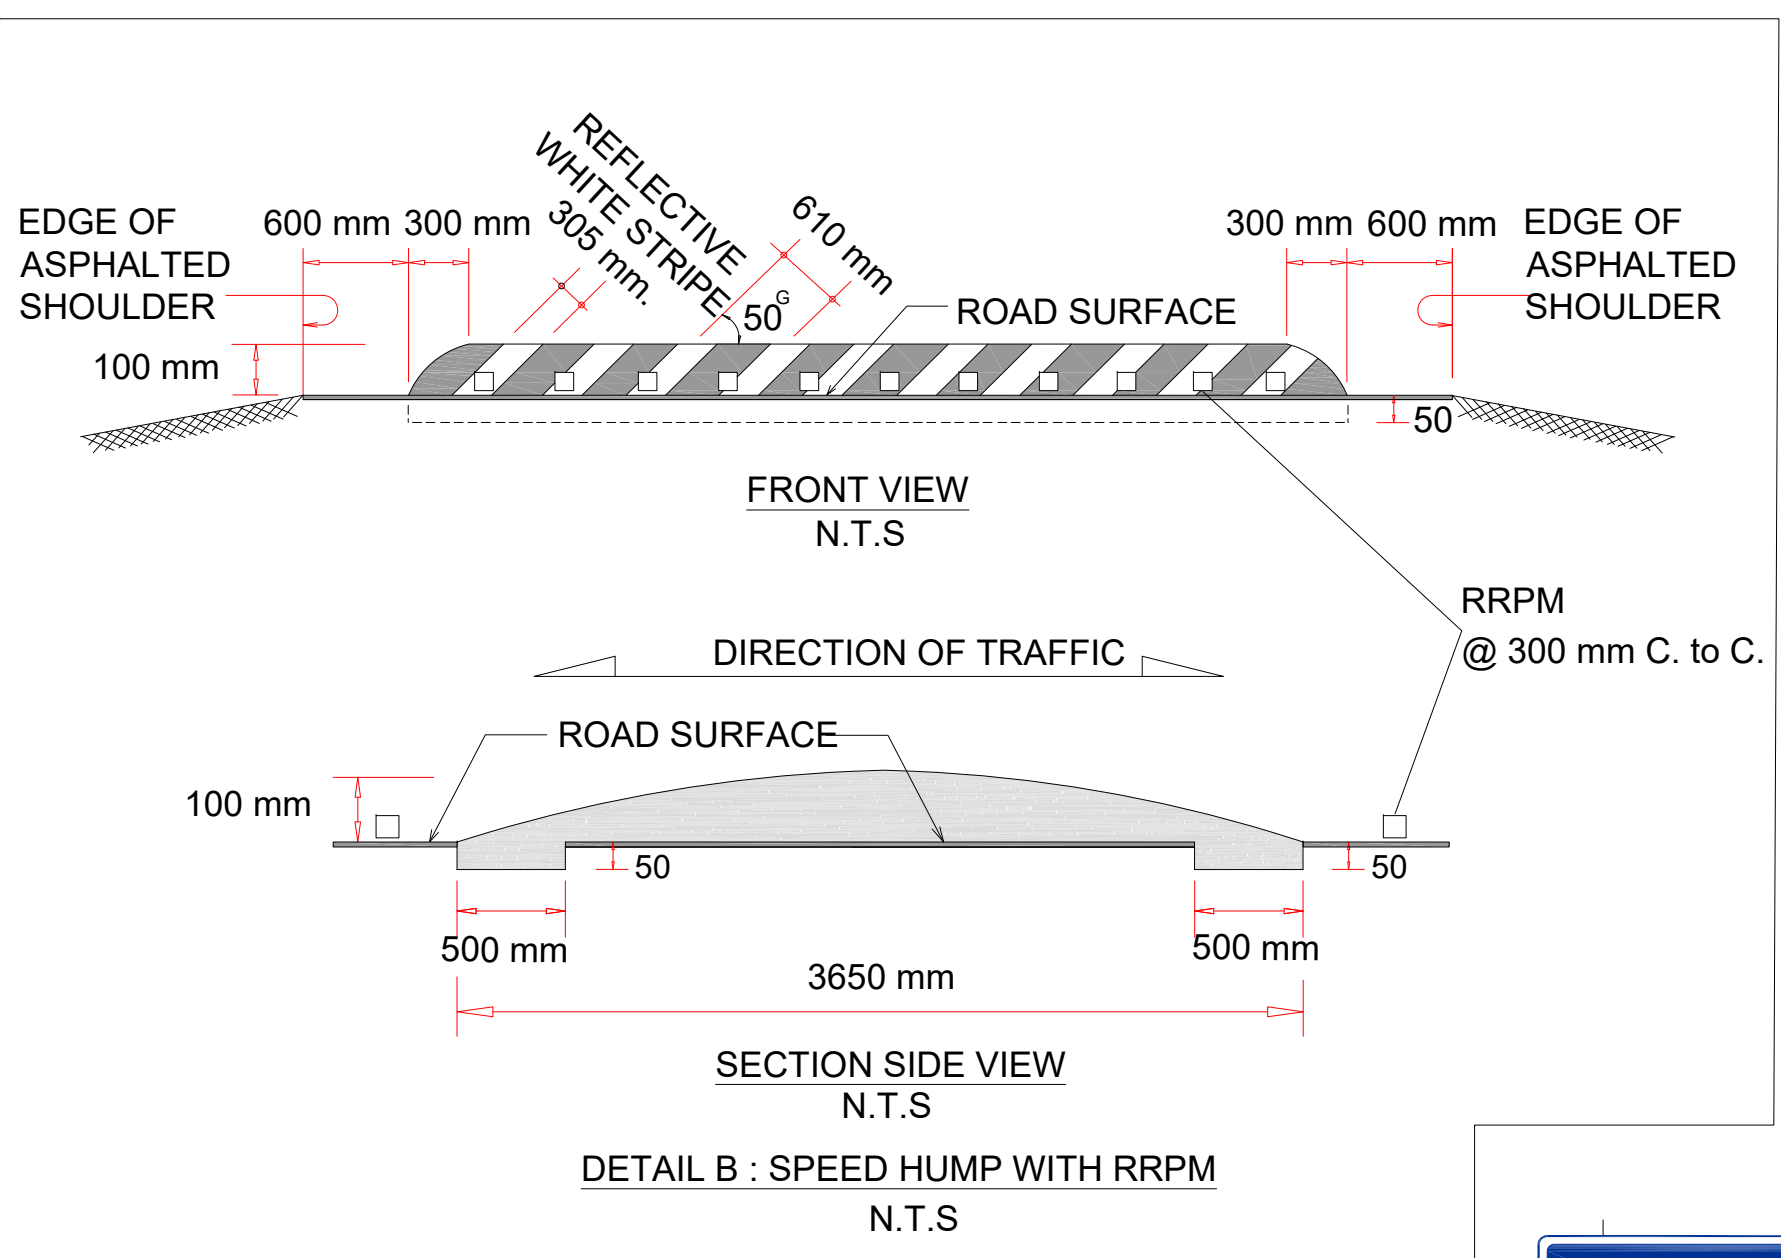
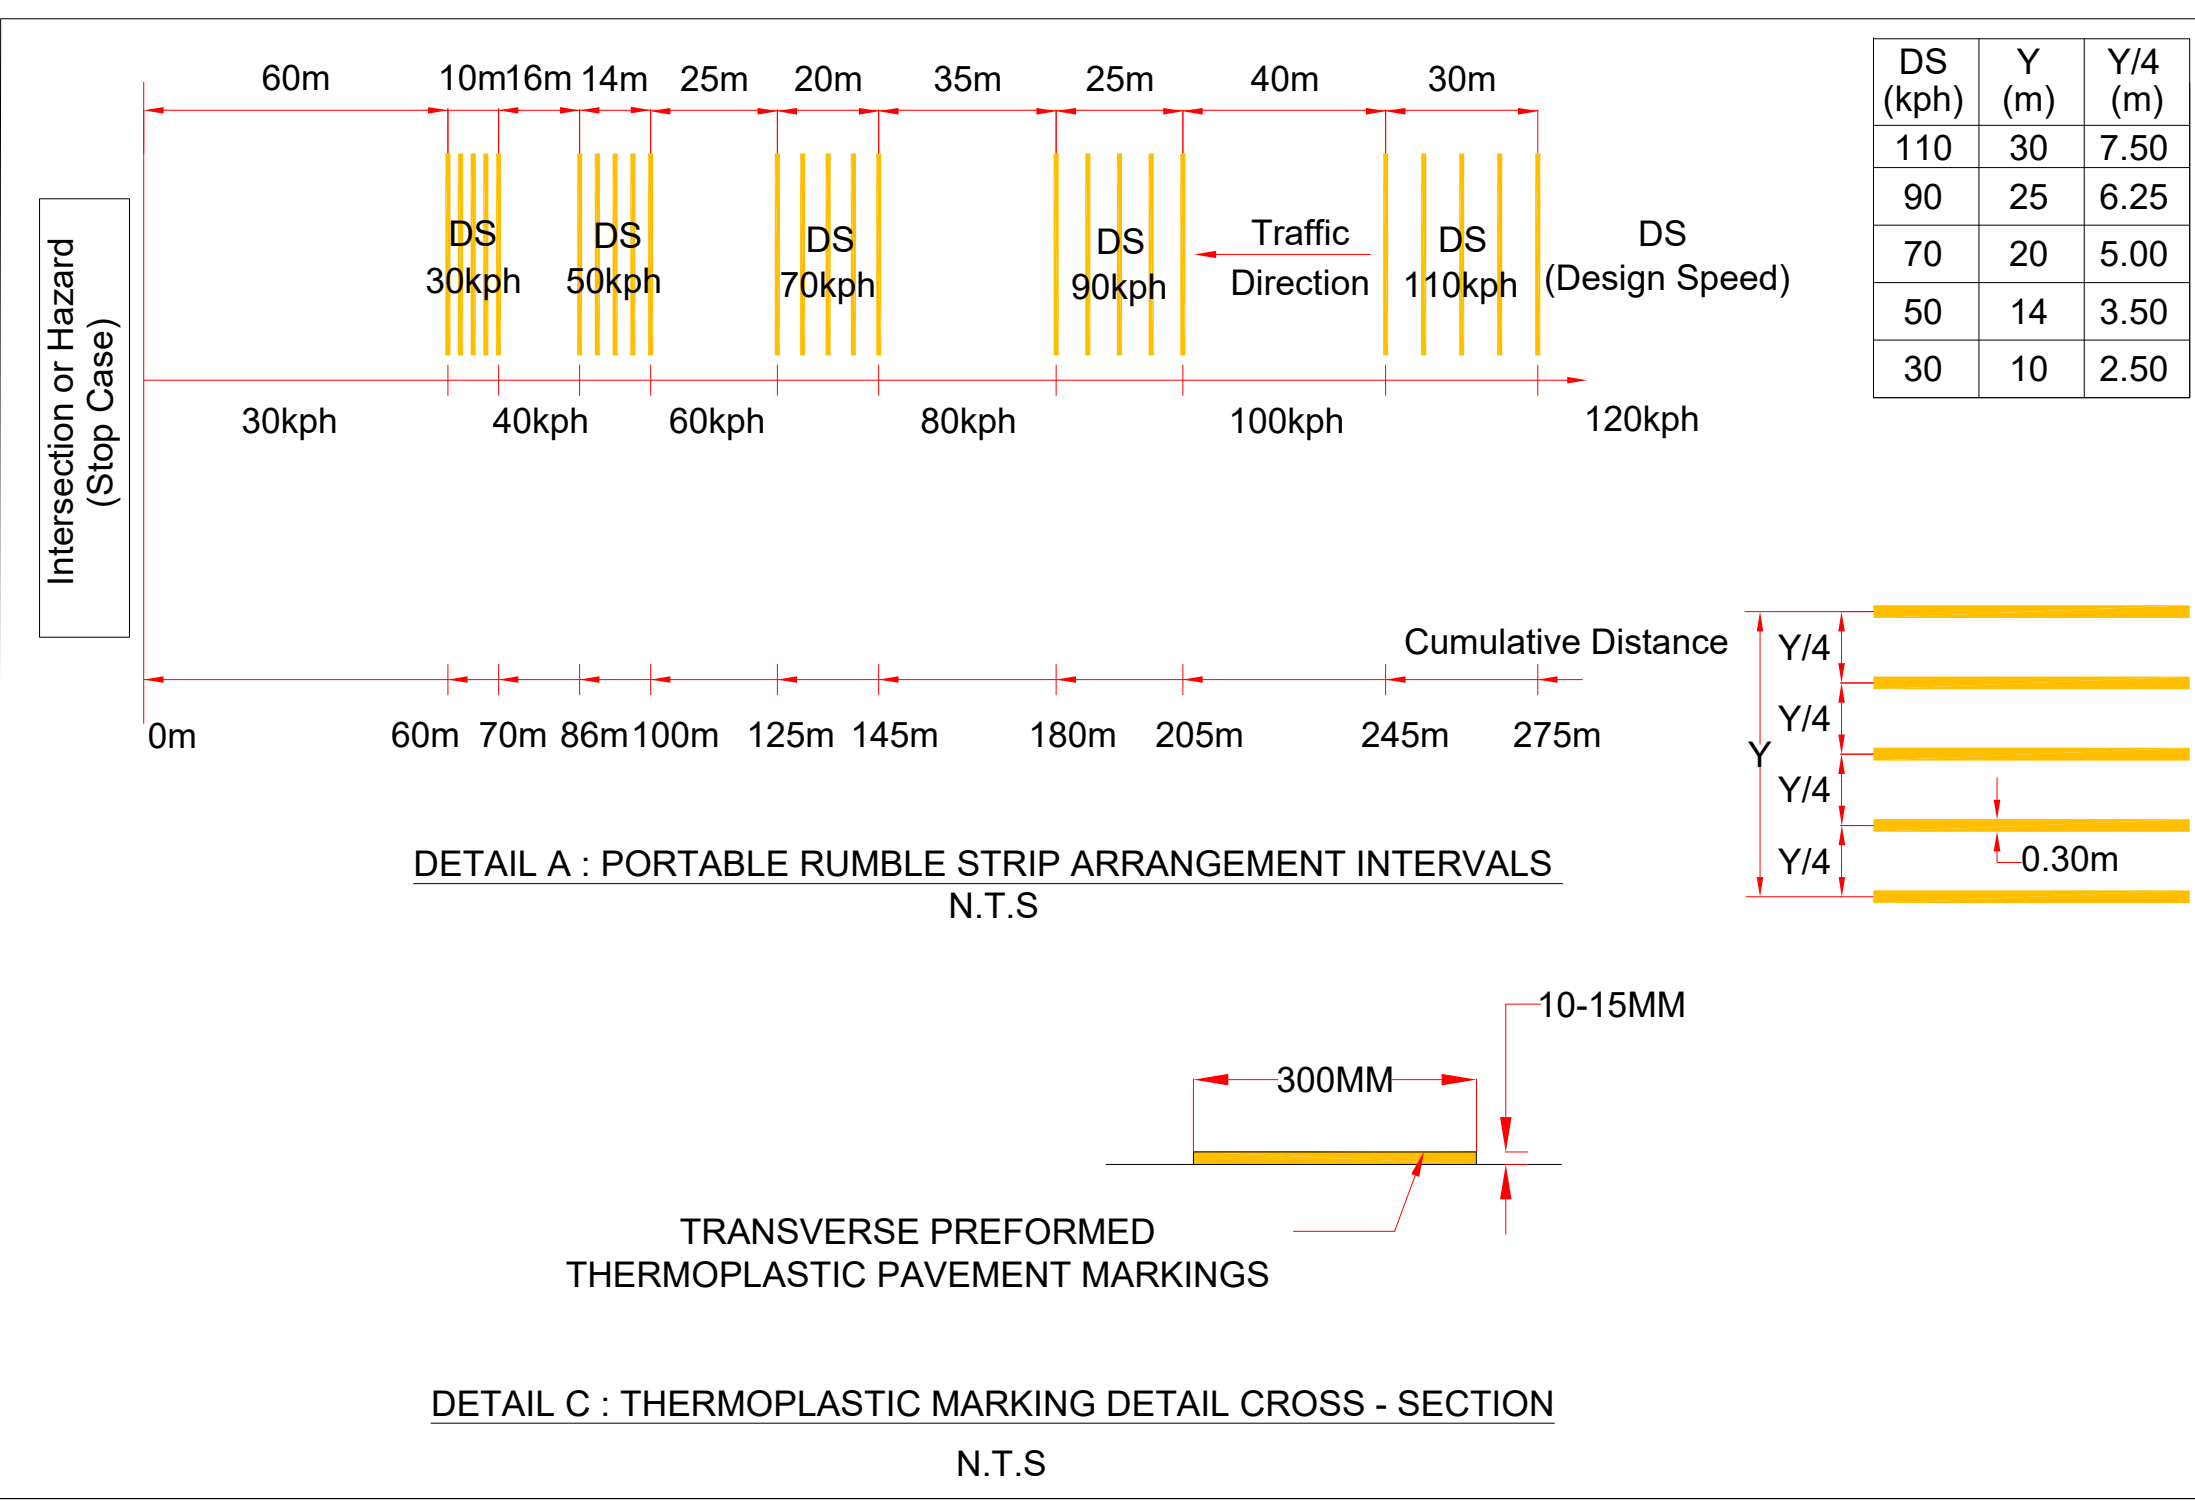
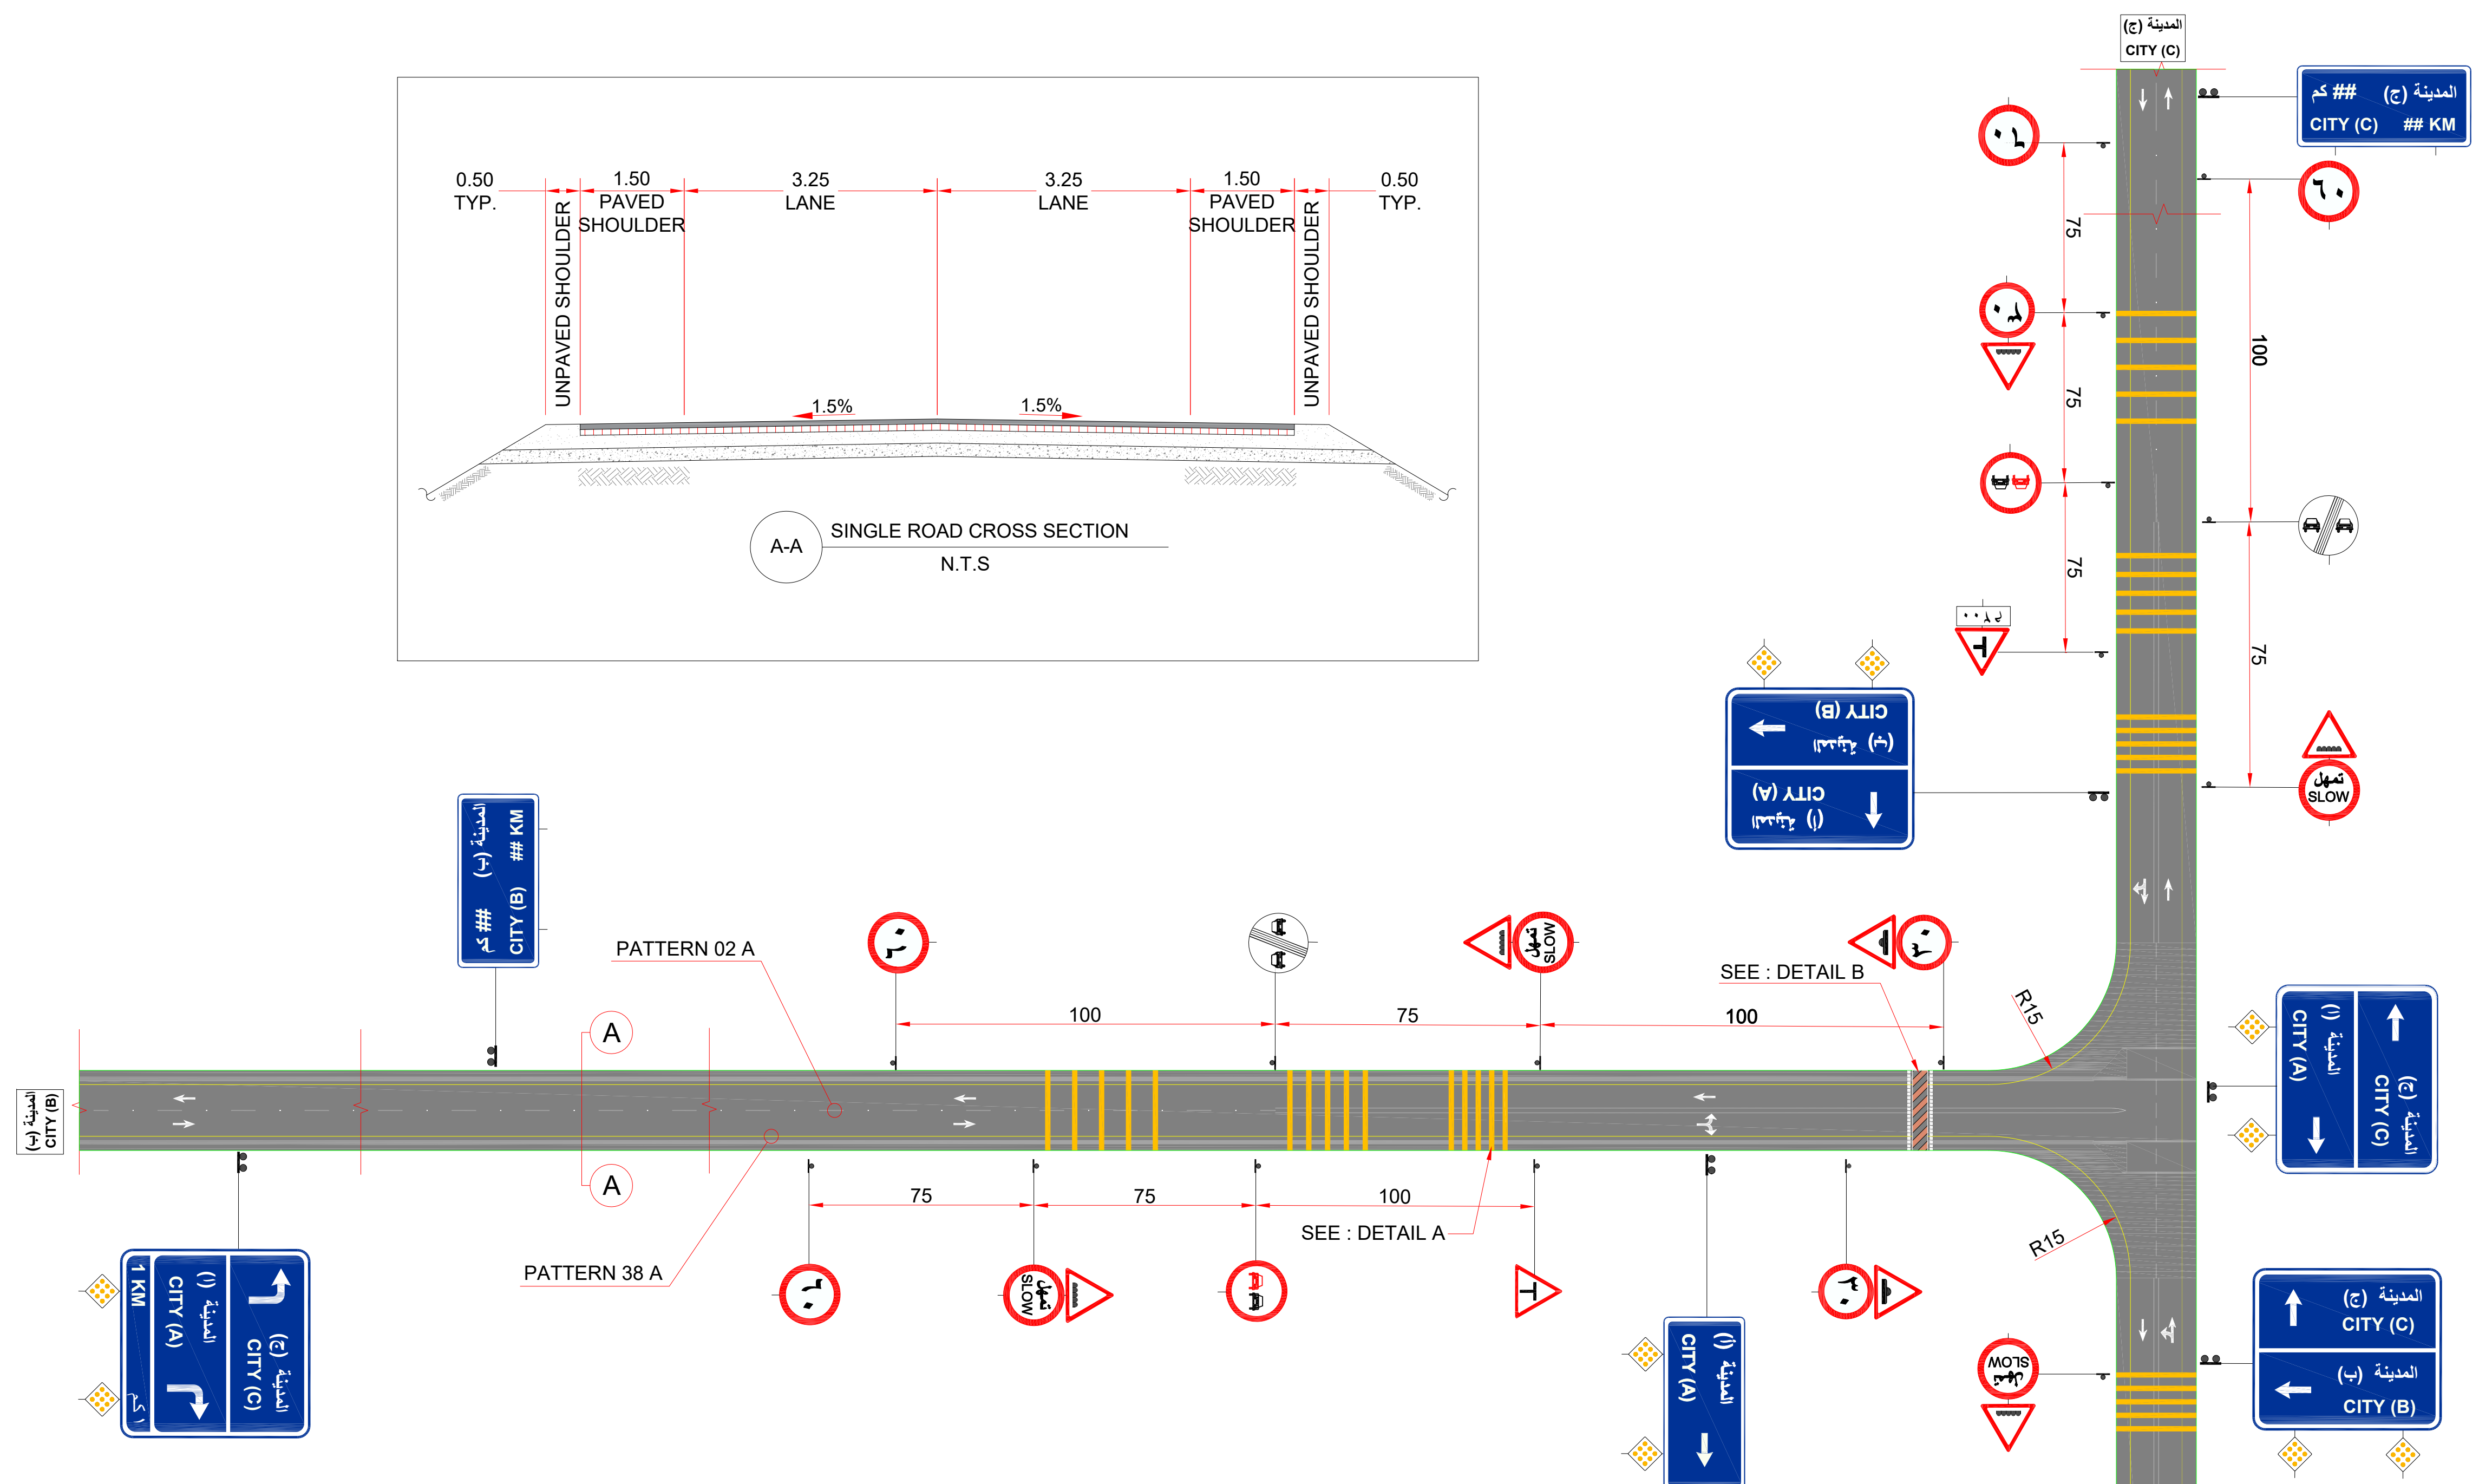


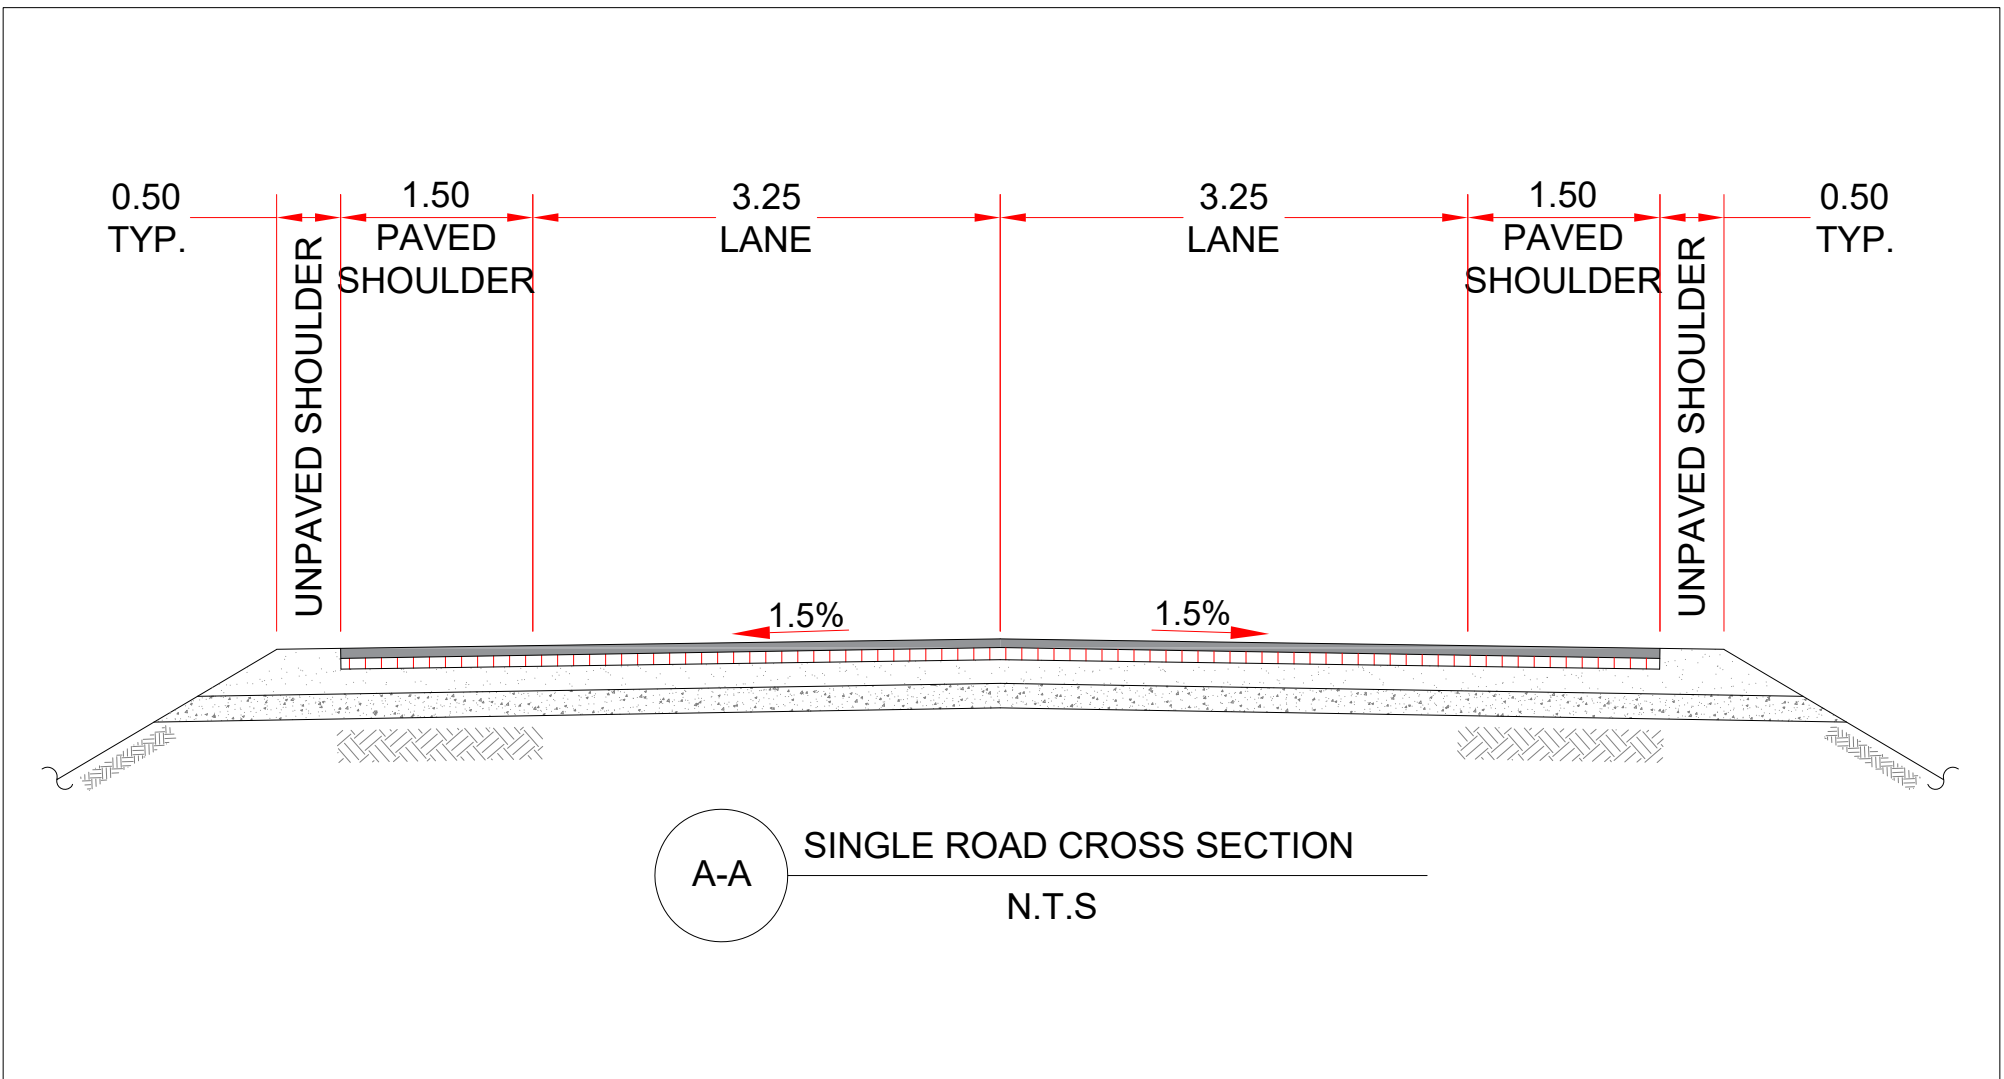

- NOTES:
- ALL DIMENSIONS ARE IN METRIC UNITS, UNLESS OTHERWISE MENTIONED.
  - ALL SIGNAGE INSTALLATIONS AND MARKINGS MUST BE IN ACCORDANCE WITH MUTCD KSA UPDATED STANDARDS & SPECIFICATIONS.
  - INTERSECTION AREAS MUST BE FURNISHED WITH STREET LIGHTING AS PER MOT STANDARDS (IF NO ELECTRIC POWER IS AVAILABLE, SOLAR POWERED LIGHTS SHOULD BE PROVIDED).
  - THE CONTRACTOR SHOULD ACKNOWLEDGE TO MOT ALL OTHER REQUIRED PRECAUTIONS SHOULD BE TAKEN ON-SITE, PREPARING THE NECESSARY PROPOSALS FOR MOT APPROVAL
  - DO NOT TAKE ANY MEASUREMENTS FROM THIS DRAWING, THE DRAWING IS NOT TO SCALE.
  - THE SHOWN DETAIL IS VALID FOR RURAL LOCAL ROADS INTERSECTION, OPERATION SPEED MIGHT VARY AS PER ACTUAL DESIGN.
  - THIS INTERSECTION DETAILS ARE APPLICABLE ONLY FOR LOW - VOLUME- RURAL ROAD, ADT ≤ 500