
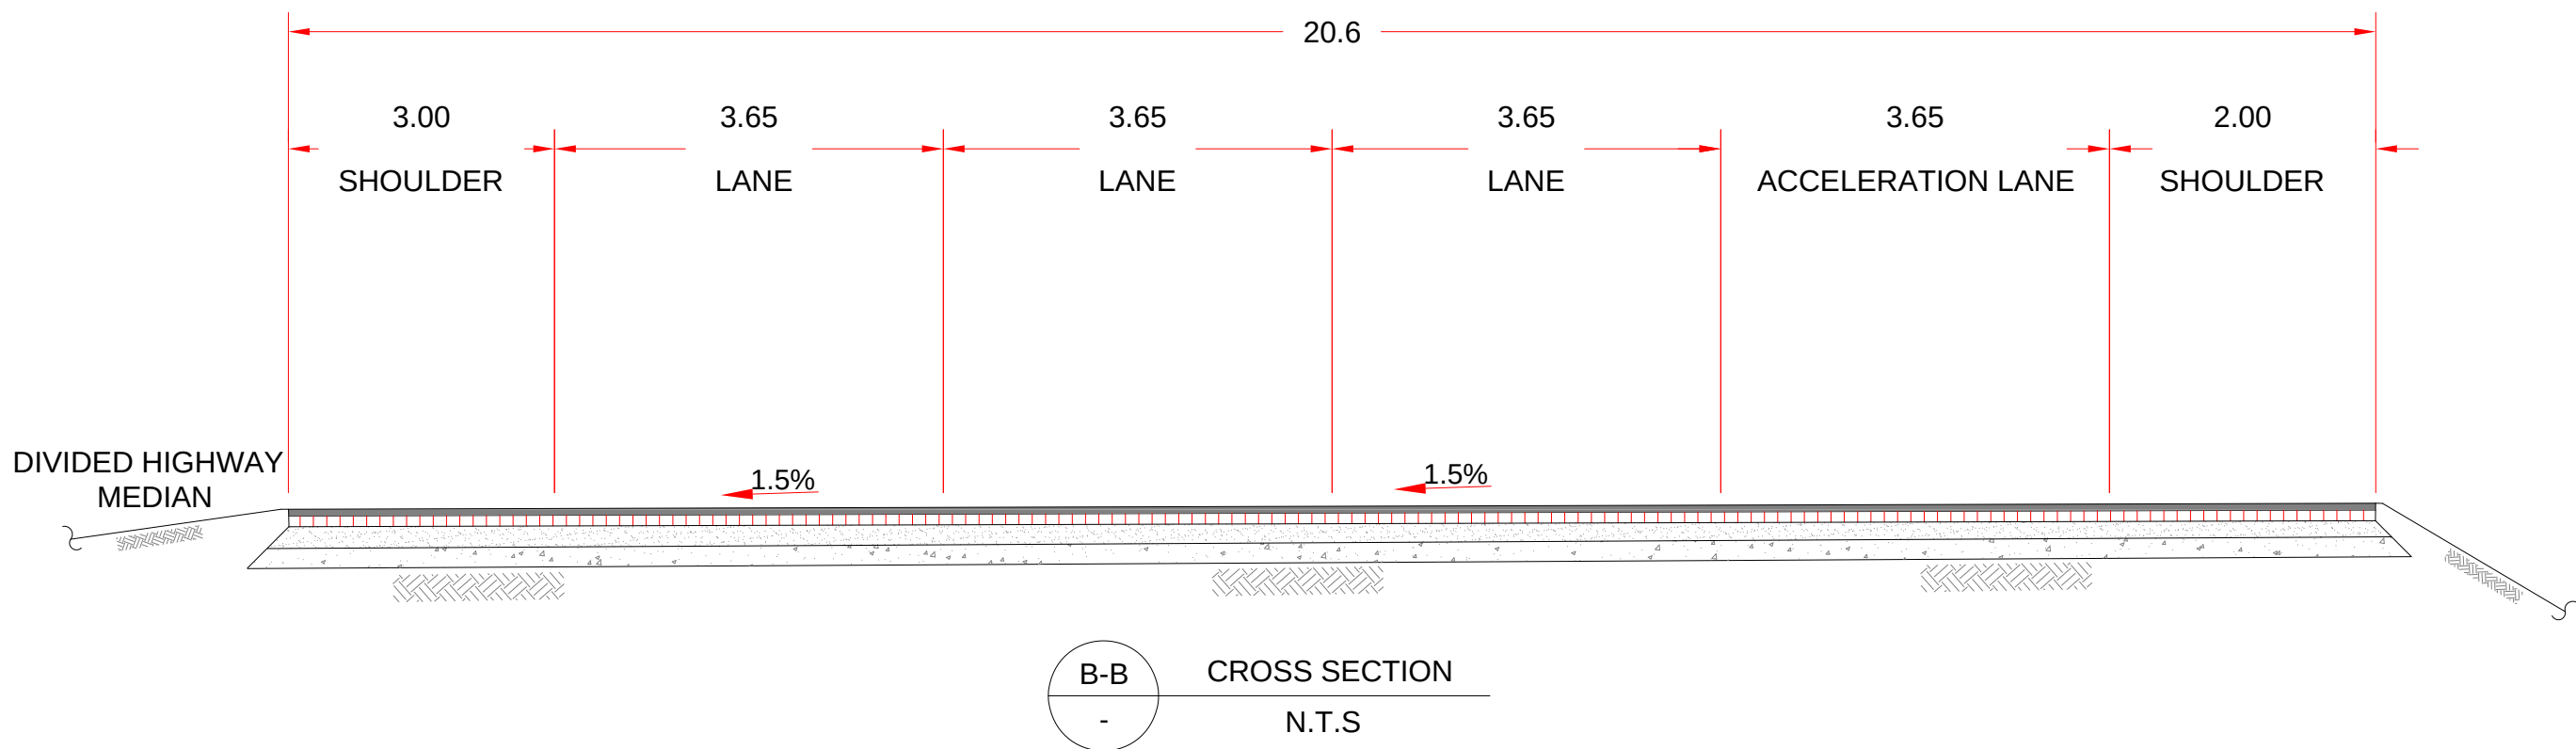
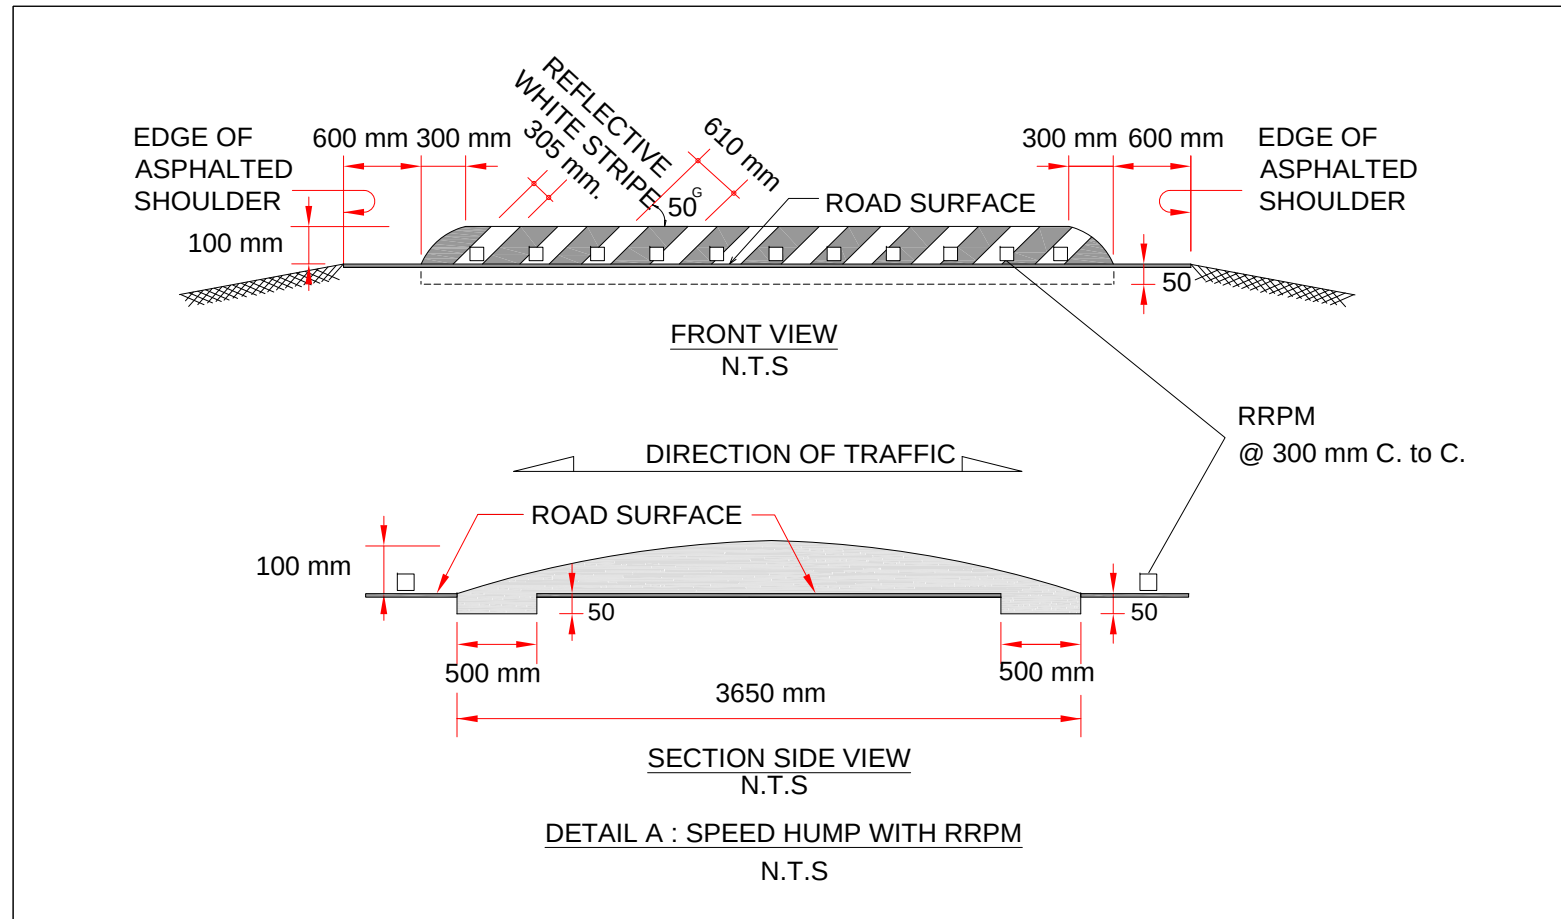


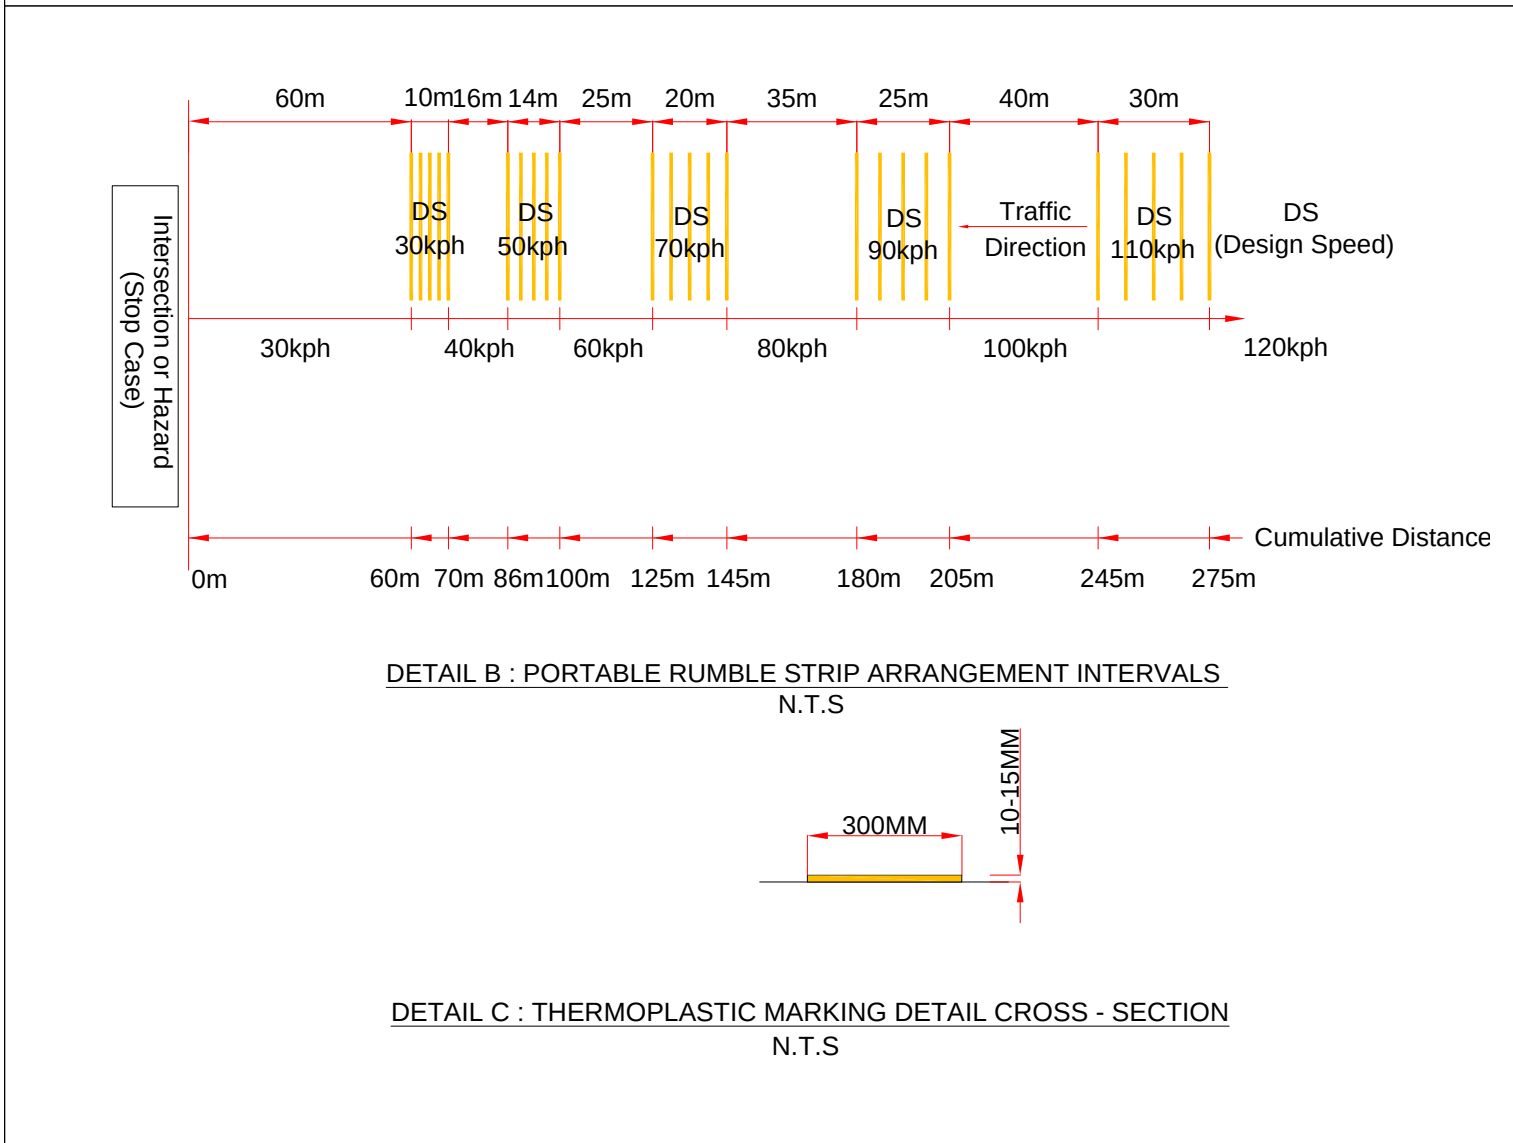

- | | | |
|--|--|---|
| KINGDOM OF SAUDI ARABIA
MINISTRY OF TRANSPORT | | 
وزارة النقل
TRANSPORT MINISTRY |
| TITLE : المخطط النموذجي لتقاطعات ثلاثي
الطريق فرعي مع طريق سريع مزووج (بديل مؤقت لطريق الخدمة)
TYPICAL T-JUNCTION DETAILS
BETWEEN BRANCH ROAD AND DIVIDED HIGHWAYS
(TEMPORARY ALTERNATIVE FOR SERVICE ROAD) | | |
| DRAWING NUMBER | | DATE : FEBRUARY 2019 |
| RD1-MOT-RSD-DWG-1902-043 | | SHEET SIZE: A1 |