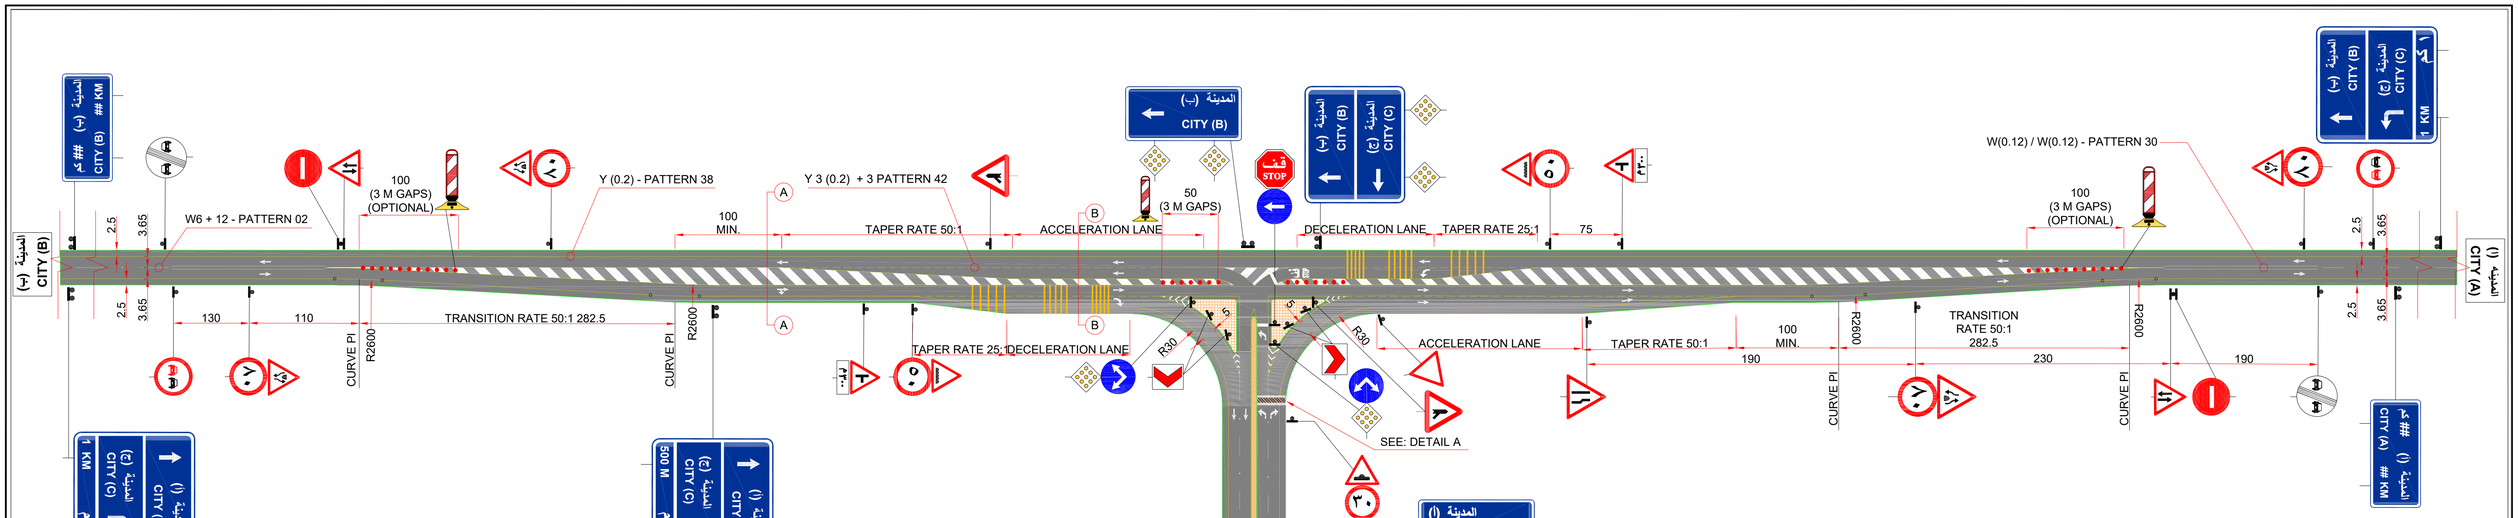

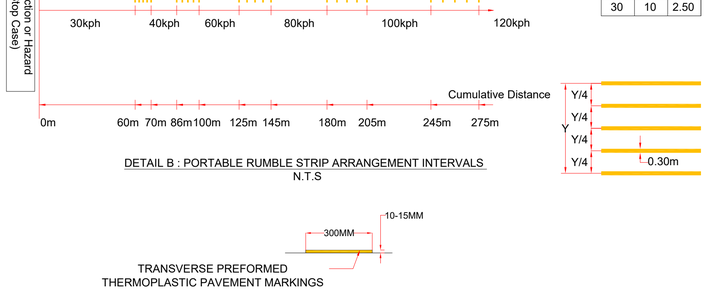

DS (kph)	Y (m)	Y/4 (m)
110	30	7.50
90	25	6.25
70	20	5.00
50	14	3.50
30	10	2.50

DETAIL B : PORTABLE RUMBLE STRIP ARRANGEMENT INTERVALS
N.T.S

TRANSVERSE PREFORMED THERMOPLASTIC PAVEMENT MARKINGS

DETAIL C : THERMOPLASTIC MARKING DETAIL CROSS - SECTION
N.T.S

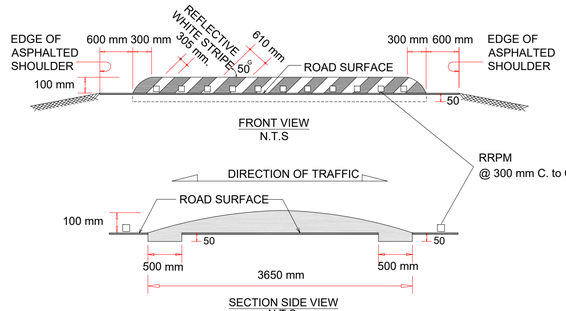

DETAIL A : SPEED HUMP WITH RRPM
N.T.S

NOTES:

1. ALL DIMENSIONS ARE IN METRIC UNITS, UNLESS OTHERWISE MENTIONED.
2. PLEASE REFER TO MOT HDM V.2 BOOK 1 OF 2 PAGES 215 - 219 FOR AUXILIARY LANES AND TAPER DETAILS AT DIFFERENT DESIGN SPEEDS.
3. ALL SIGNAGE INSTALLATIONS AND MARKINGS MUST BE IN ACCORDANCE WITH MUTCD KSA UPDATED STANDARDS & SPECIFICATIONS.
4. INTERSECTION AREAS MUST BE FURNISHED WITH STREET LIGHTING AS PER MOT STANDARDS
   (IF NO ELECTRIC POWER IS AVAILABLE, SOLAR POWERED LIGHTS SHOULD BE PROVIDED.
5. SPEED CHANGE LENGTHS VARIES ACCORDING TO VARIANCE OF MAIN HIGHWAY DESIGN SPEED.
6. TRANSITION CURVES RADII MAY VARY TO CONFORM WITH DESIGN SPEED AND SUPERELEVATION REQUIREMENTS OF THE SERVICE ROAD HOWEVER, LARGER RADII WITH NO SUPERELEVATION REQUIRED ARE PREFERABLE AS SHOWN.
7. THE CONTRACTOR SHOULD ACKNOWLEDGE TO MOT ALL OTHER REQUIRED PRECAUTIONS SHOULD BE TAKEN ON-SITE, PREPARING THE NECESSARY PROPOSALS FOR MOT APPROVAL .
8. DO NOT TAKE ANY MEASUREMENTS FROM THIS DRAWING, THE DRAWING IS NOT TO SCALE.
9. THE SHOWN DETAIL IS VALID FOR SINGLE HIGHWAYS WITH VARIOUS OPERATION SPEED
10. RIGHT AND LEFT TURN RADIUS WITHIN THE INTERSECTION SHOULD FULFILL THE GEOMETRIC DESIGN REQUIREMENTS FOR 30 KPH SPEED AT LEAST
11. MEDIAN MARKING HATCH IS PREFERRED TO BE REFLECTIVE CERAMIC STUDS TO PROHIBIT VEHICLES PASSING OR PARKING OVER MEDIAN SPACE.
12. INTERSECTION'S TRIANGULAR ISLAND SHOULD BE RAISED (CURBED) BY +0.15M.

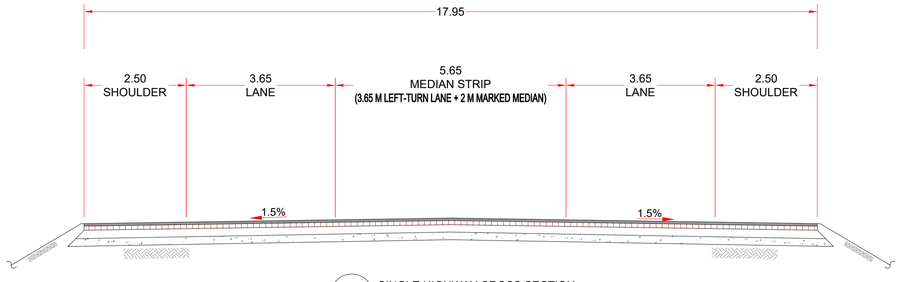

A-A SINGLE HIGHWAY CROSS SECTION
N.T.S

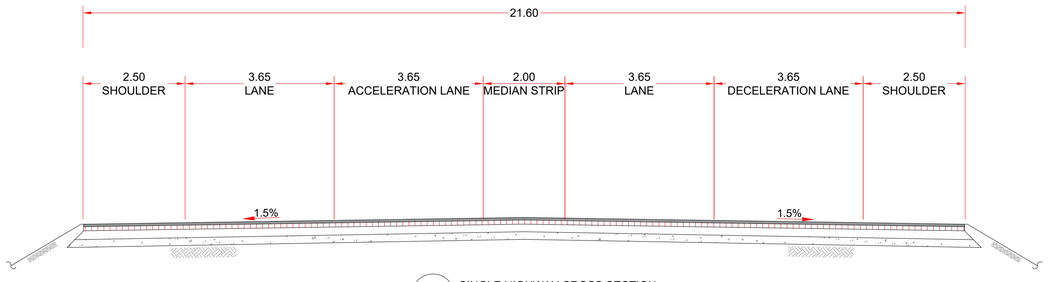

B-B SINGLE HIGHWAY CROSS SECTION
N.T.S

KINGDOM OF SAUDI ARABIA

MINISTRY OF TRANSPORT

وزارة النقل
TRANSPORT MINISTRY

TITLE :

المخطط النموذجي لربط طريق سريع مفرد مع طريق مزدوج محلي

TYPICAL T-INTERSECTION ON SINGLE HIGHWAY WITH LOCAL DIVIDED ROAD

DRAWING NUMBER	DATE : JANUARY 2019
RD1-MOT-RSD-DWG-1901-042	SHEET SIZE: A1