
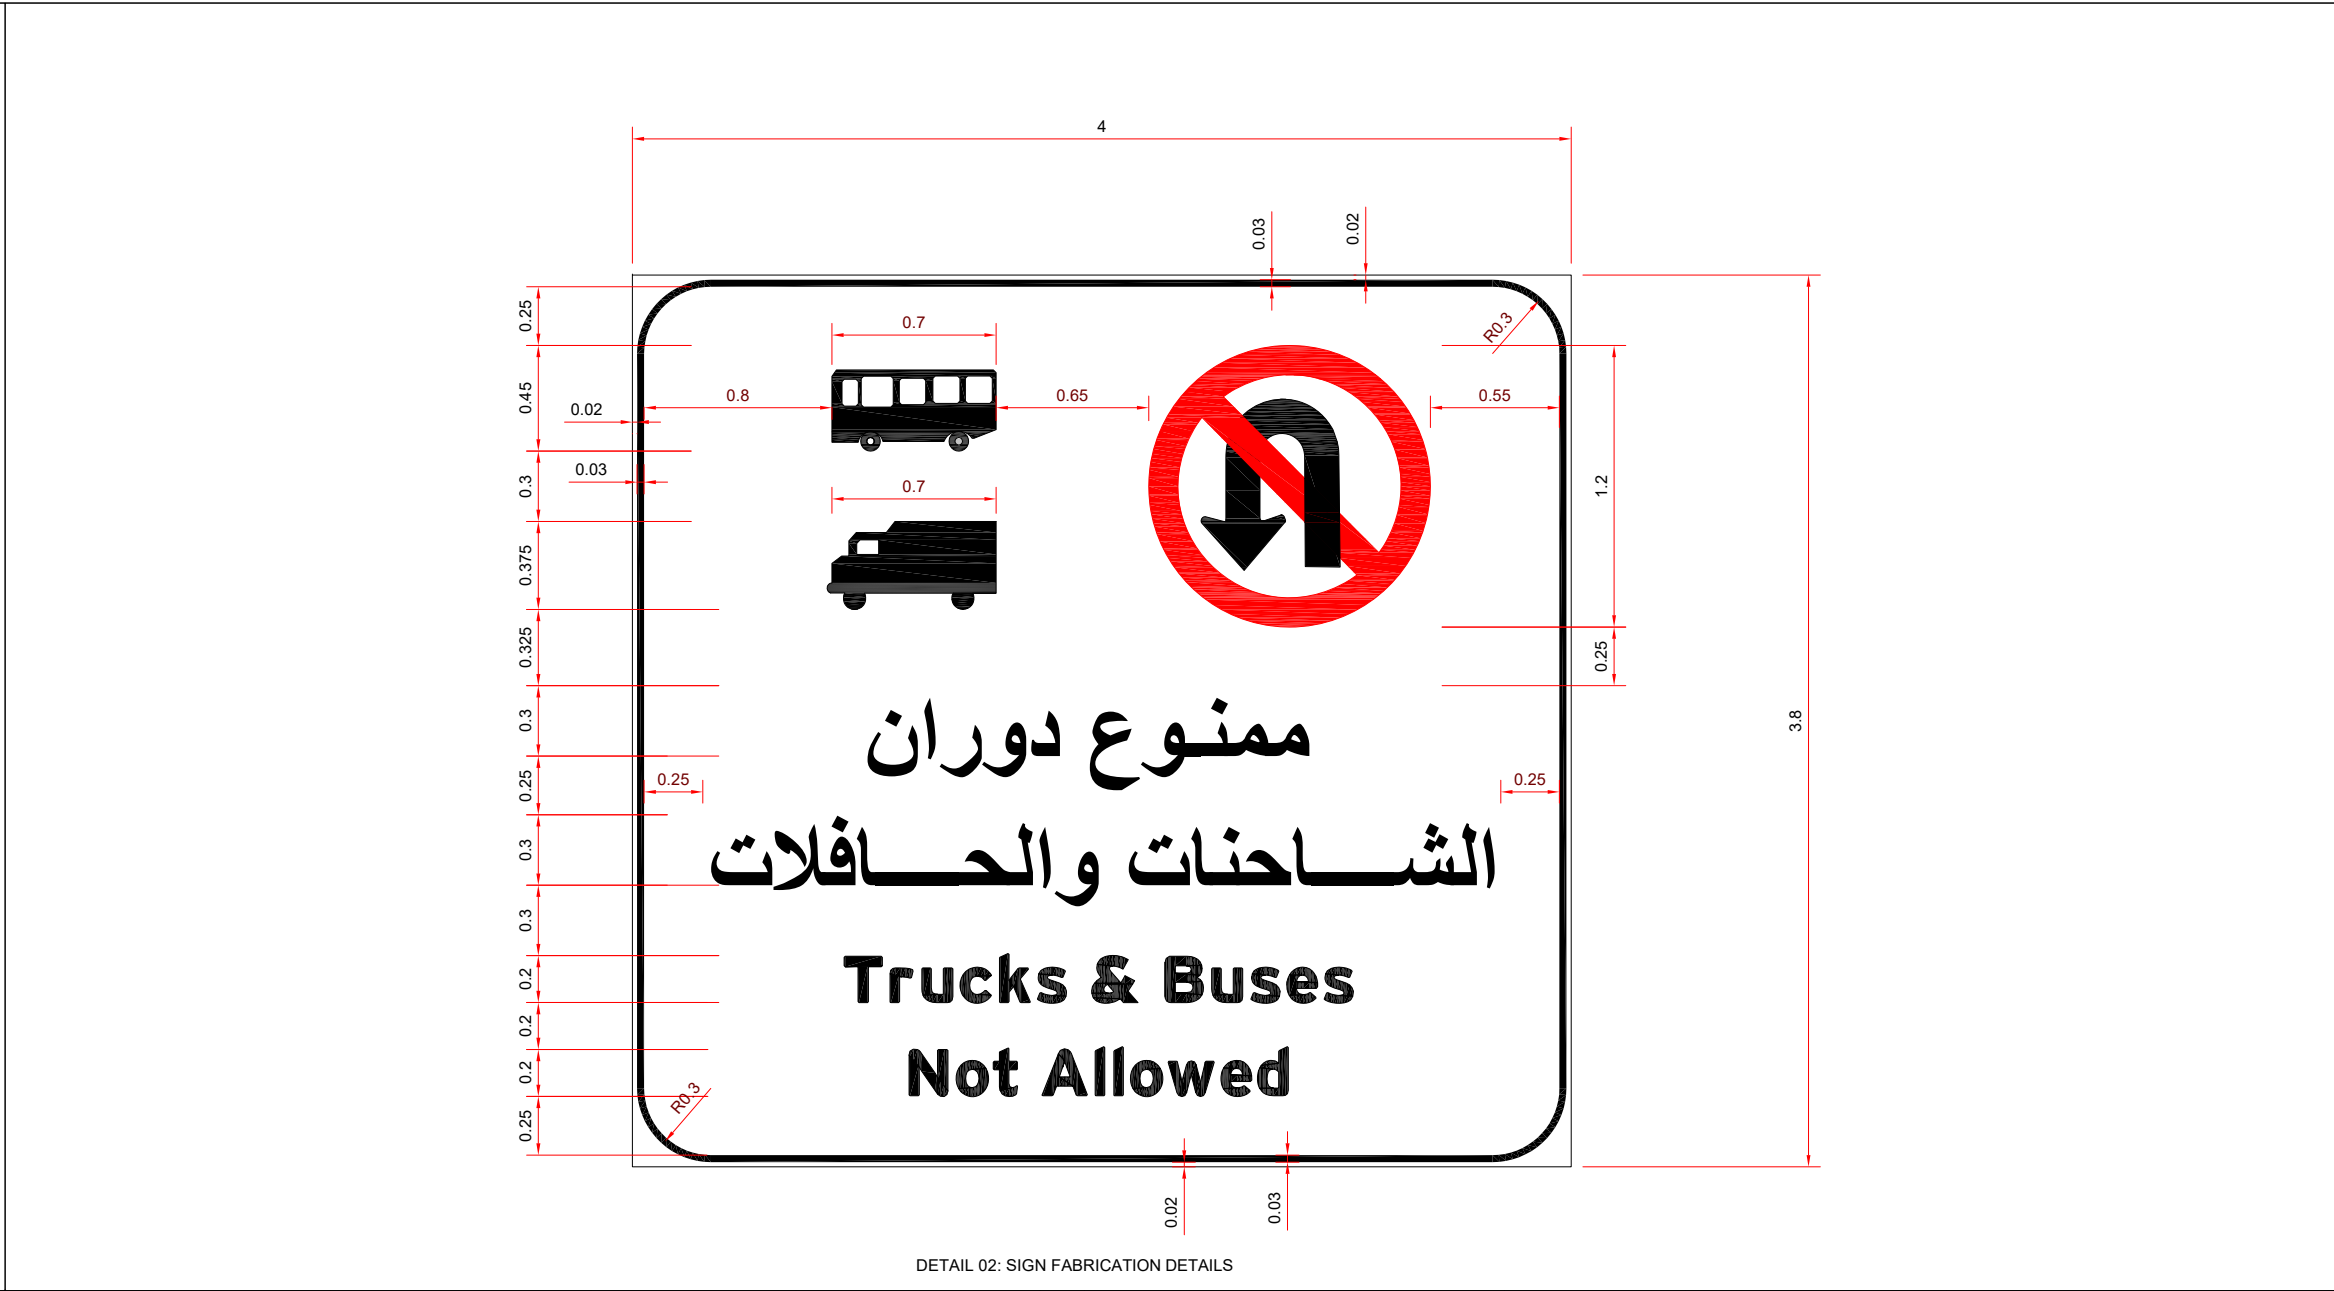
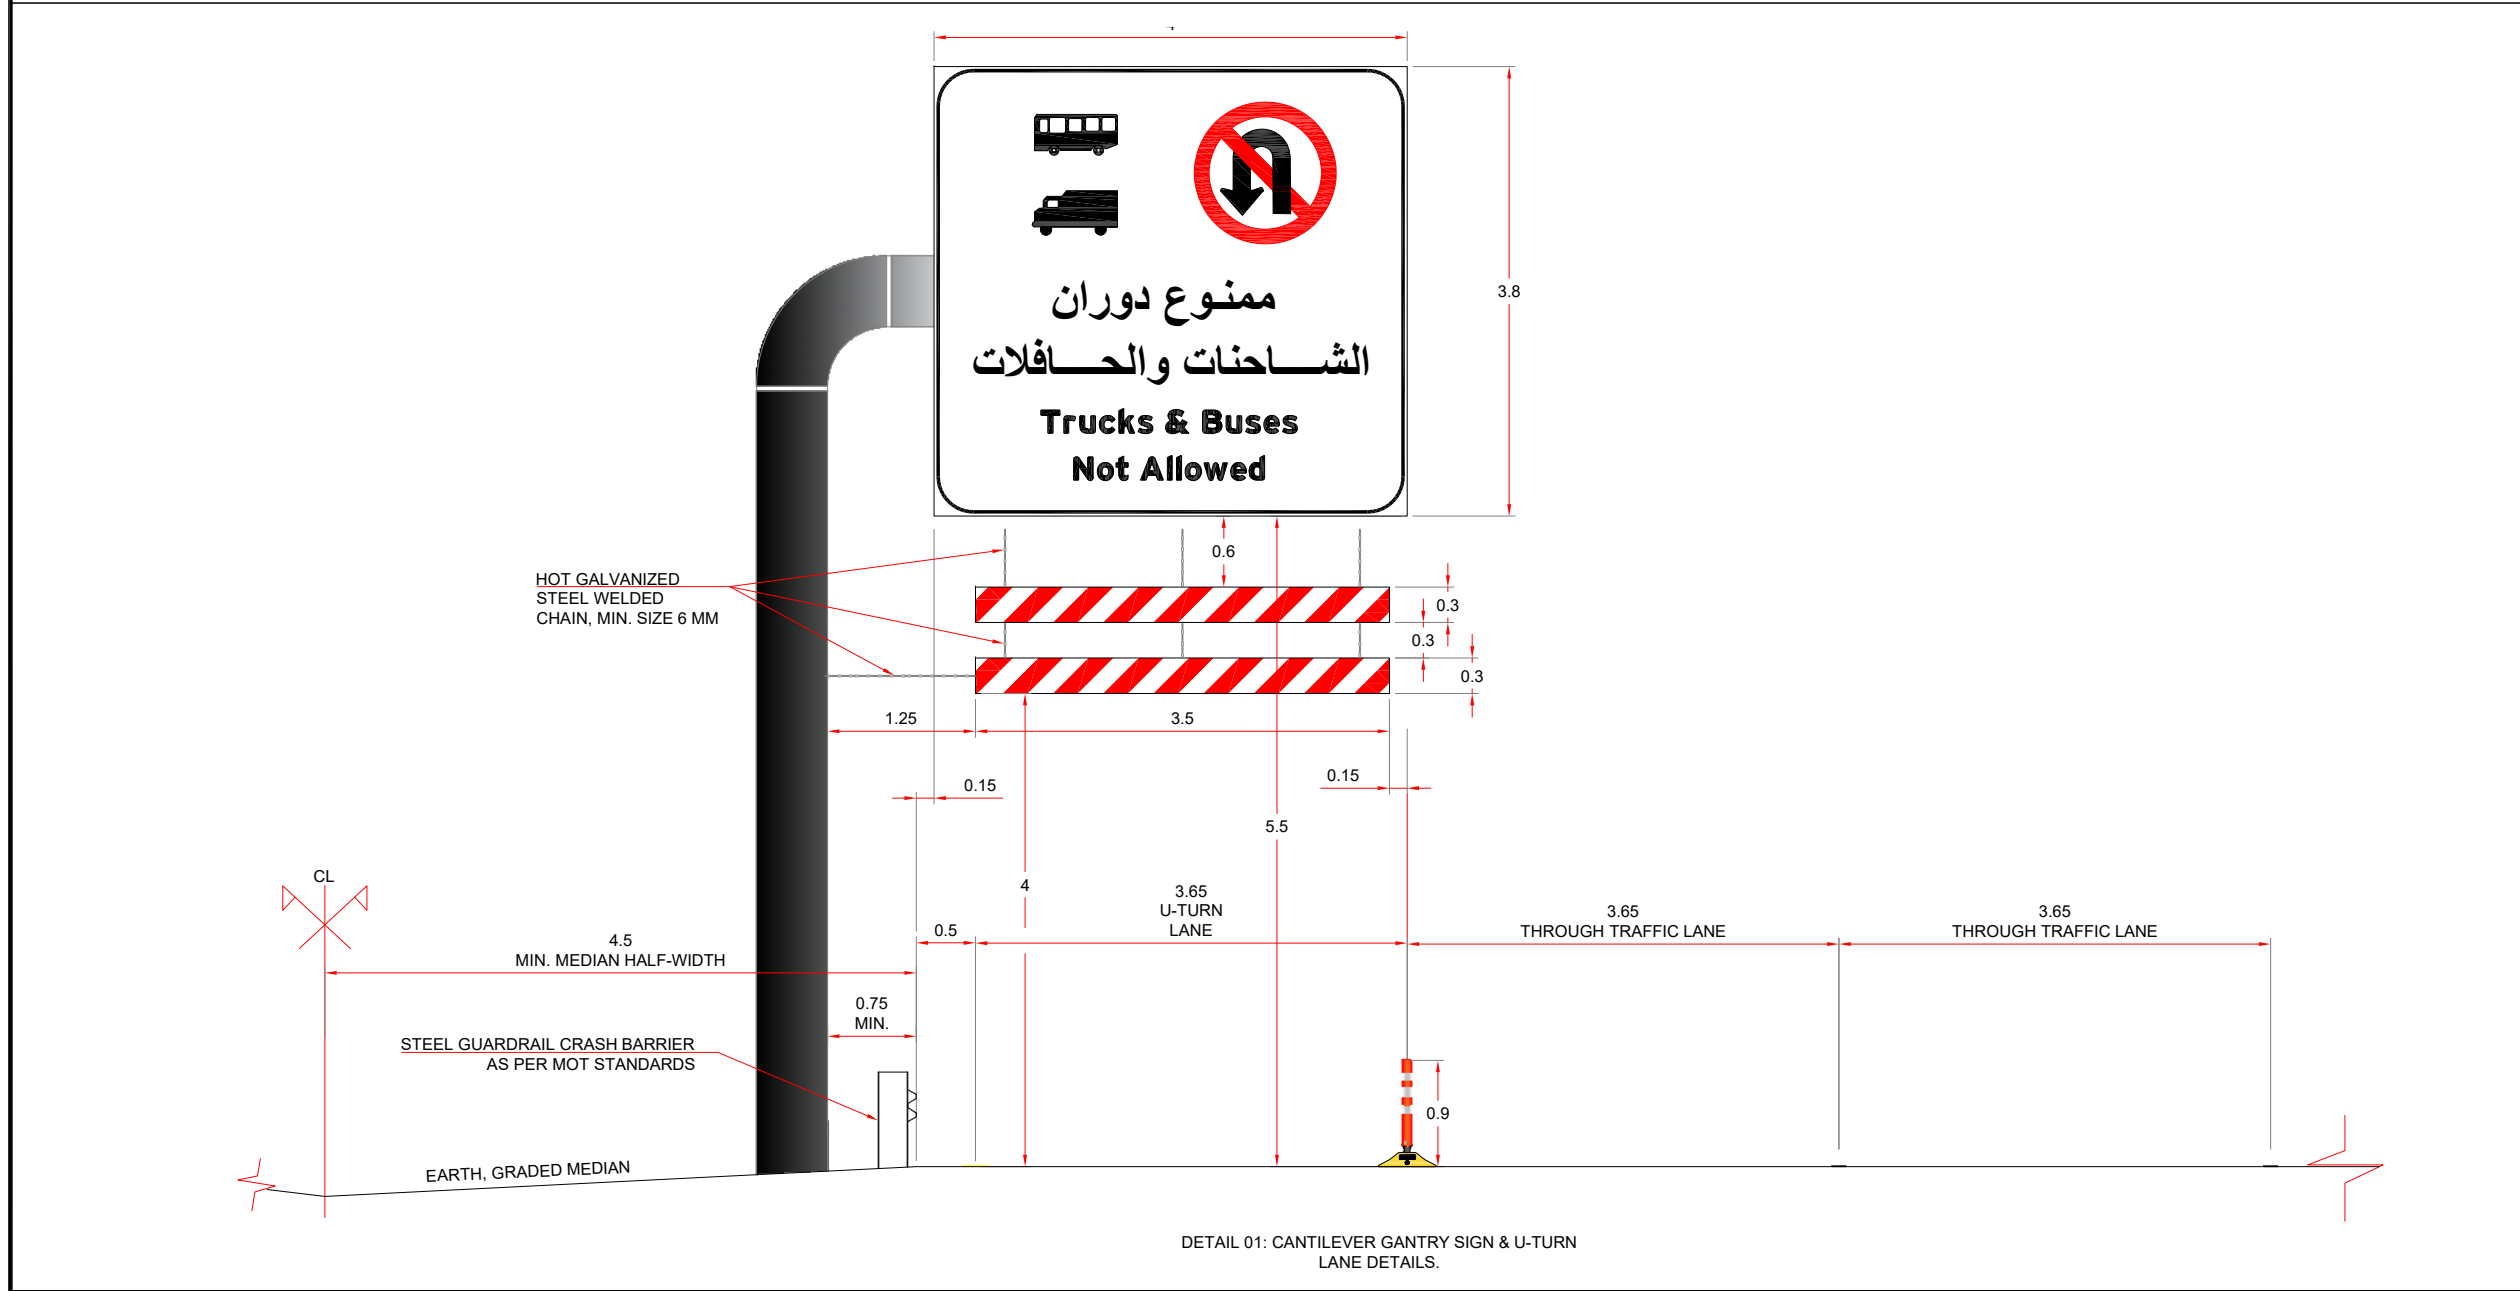



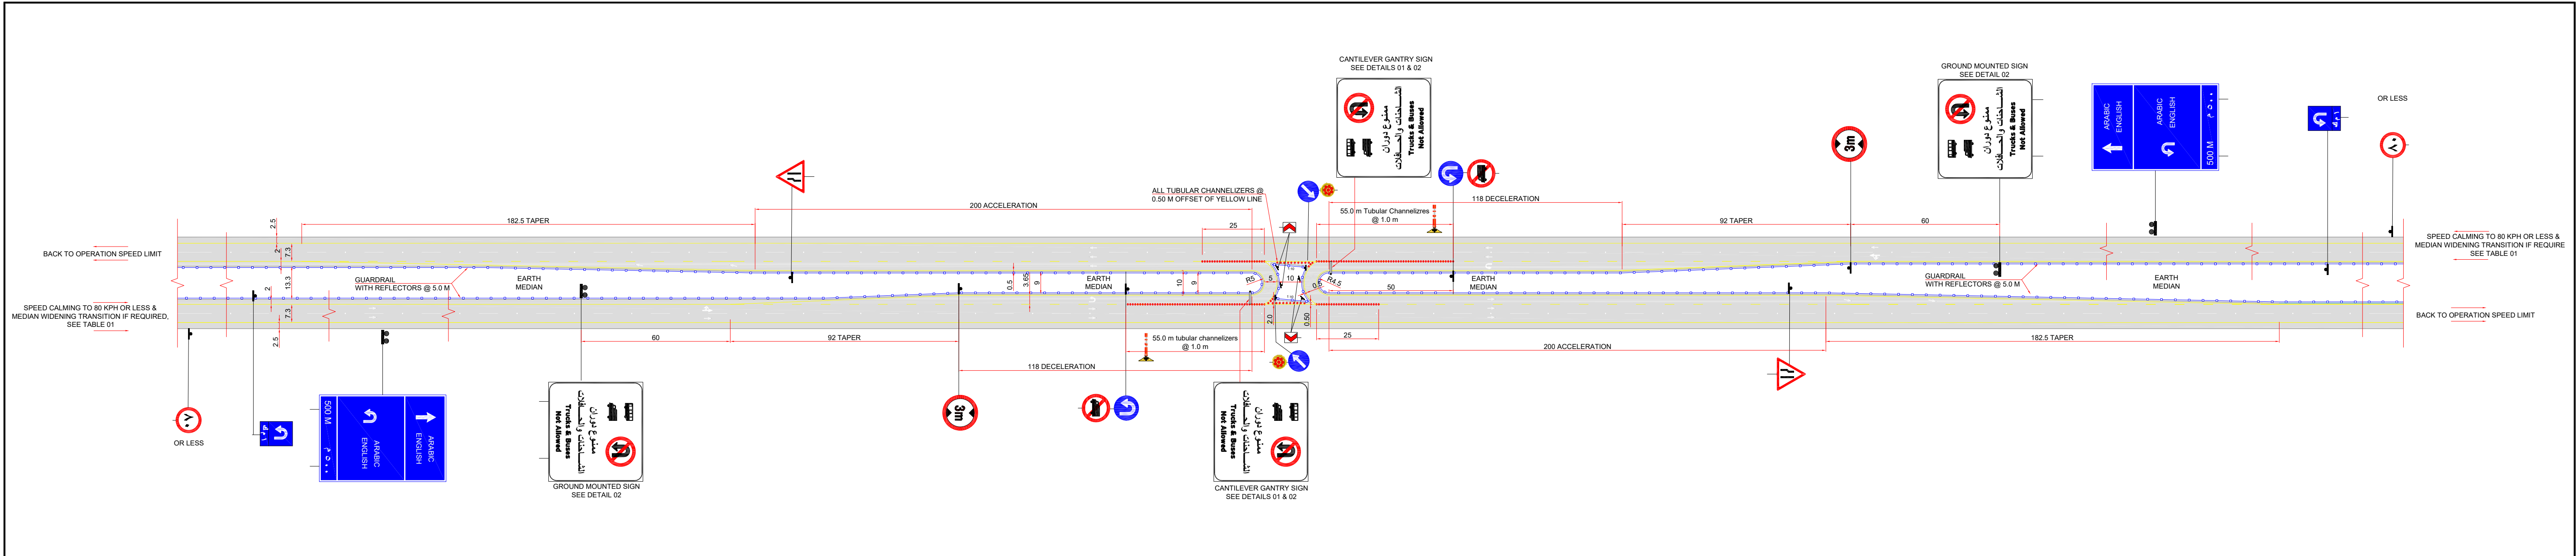


- NOTES :
- DIMENSIONS SHOWN ARE AS SPECIFIED AND NOT TO SCALE.
 - SHOWN SPEED-CHANGE LANES LENGTHS ARE DESIGNED TO DESIGN SPEED OF 80 KPH AS THE MAX ALLOWED SPEED.
 - U-TURN AREA MUST BE FURNISHED WITH STREET LIGHTING AS PER MOT STANDARD (IF ELECTRIC POWER LINES ARE NOT AVAILABLE ONSITE THEN, SOLAR POWERED LIGHTING SHOULD BE PROVIDED).
 - TRANSITION CURVES RADII MAY VARY TO CONFORM WITH DESIGN SPEED AND SUPERELEVATION REQUIREMENTS. HOWEVER, LARGER RADII WITH NO SUPERELEVATION REQUIRED ARE PREFERABLE AS SHOWN.
 - U-TURN OPENINGS ARE TO BE AVOIDED ON CURVED SEGMENTS OF HIGHWAY ALIGNMENT EXCEPT FOR CURVES WITH LARGE RADII WHERE NO SUPERELEVATION IS REQUIRED ACCORDING TO MOT HDM DESIGN STANDARDS.
 - NARROW MEDIAN (LESS THAN 9 M WIDTH) SHOULD BE ALWAYS PROTECTED WITH THE APPROPRIATE BARRIER SYSTEM.
 - INTERSECTIONS AND DIRECT ACCESS ENTRANCES OR EXISTS MUST BE AVOIDED THROUGH U-TURN AND TRANSITION ZONES.
 - USE GUARDRAIL TERMINALS TYPE No. 4 ANCHOR TERMINALS FOR U-TURN SEPARATOR ISLAND EDGES.
 - ALL SIGNS, MARKINGS AND OTHER SAFETY DEVICES SHOULD FOLLOW UPDATED MOT STANDARDS.

TABLE 01:

DESIGN SPEED (KPH)	TRANSITION TAPER RATE (M:M)
60	25:1
70	45:1
80	50:1
90	55:1
100	60:1
110	70:1
120	75:1

- * SHOWN TAPER RATES DEFINE THE LONGITUDINAL DISTANCE (M) TRAVELED BY TRAFFIC VEHICLES TO MOVE Laterally BY (1 M) SHIFT DISTANCE OF THE TAPER FOR MEDIAN WIDENING OR NARROWING PURPOSES.
- * SHOWN TAPER RATES ARE NOT VALID FOR ACCELERATION NOR DECELERATION LANE TAPERS.
- * OPERATION SPEED REDUCTION SHOULD BE APPLIED THROUGH MEDIAN TRANSITION SECTION .
- *REFER TO MUTCD FOR THE EQUATIONS OF THE ABOVE VALUES.

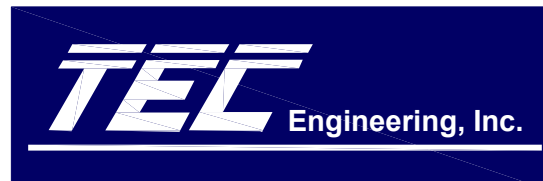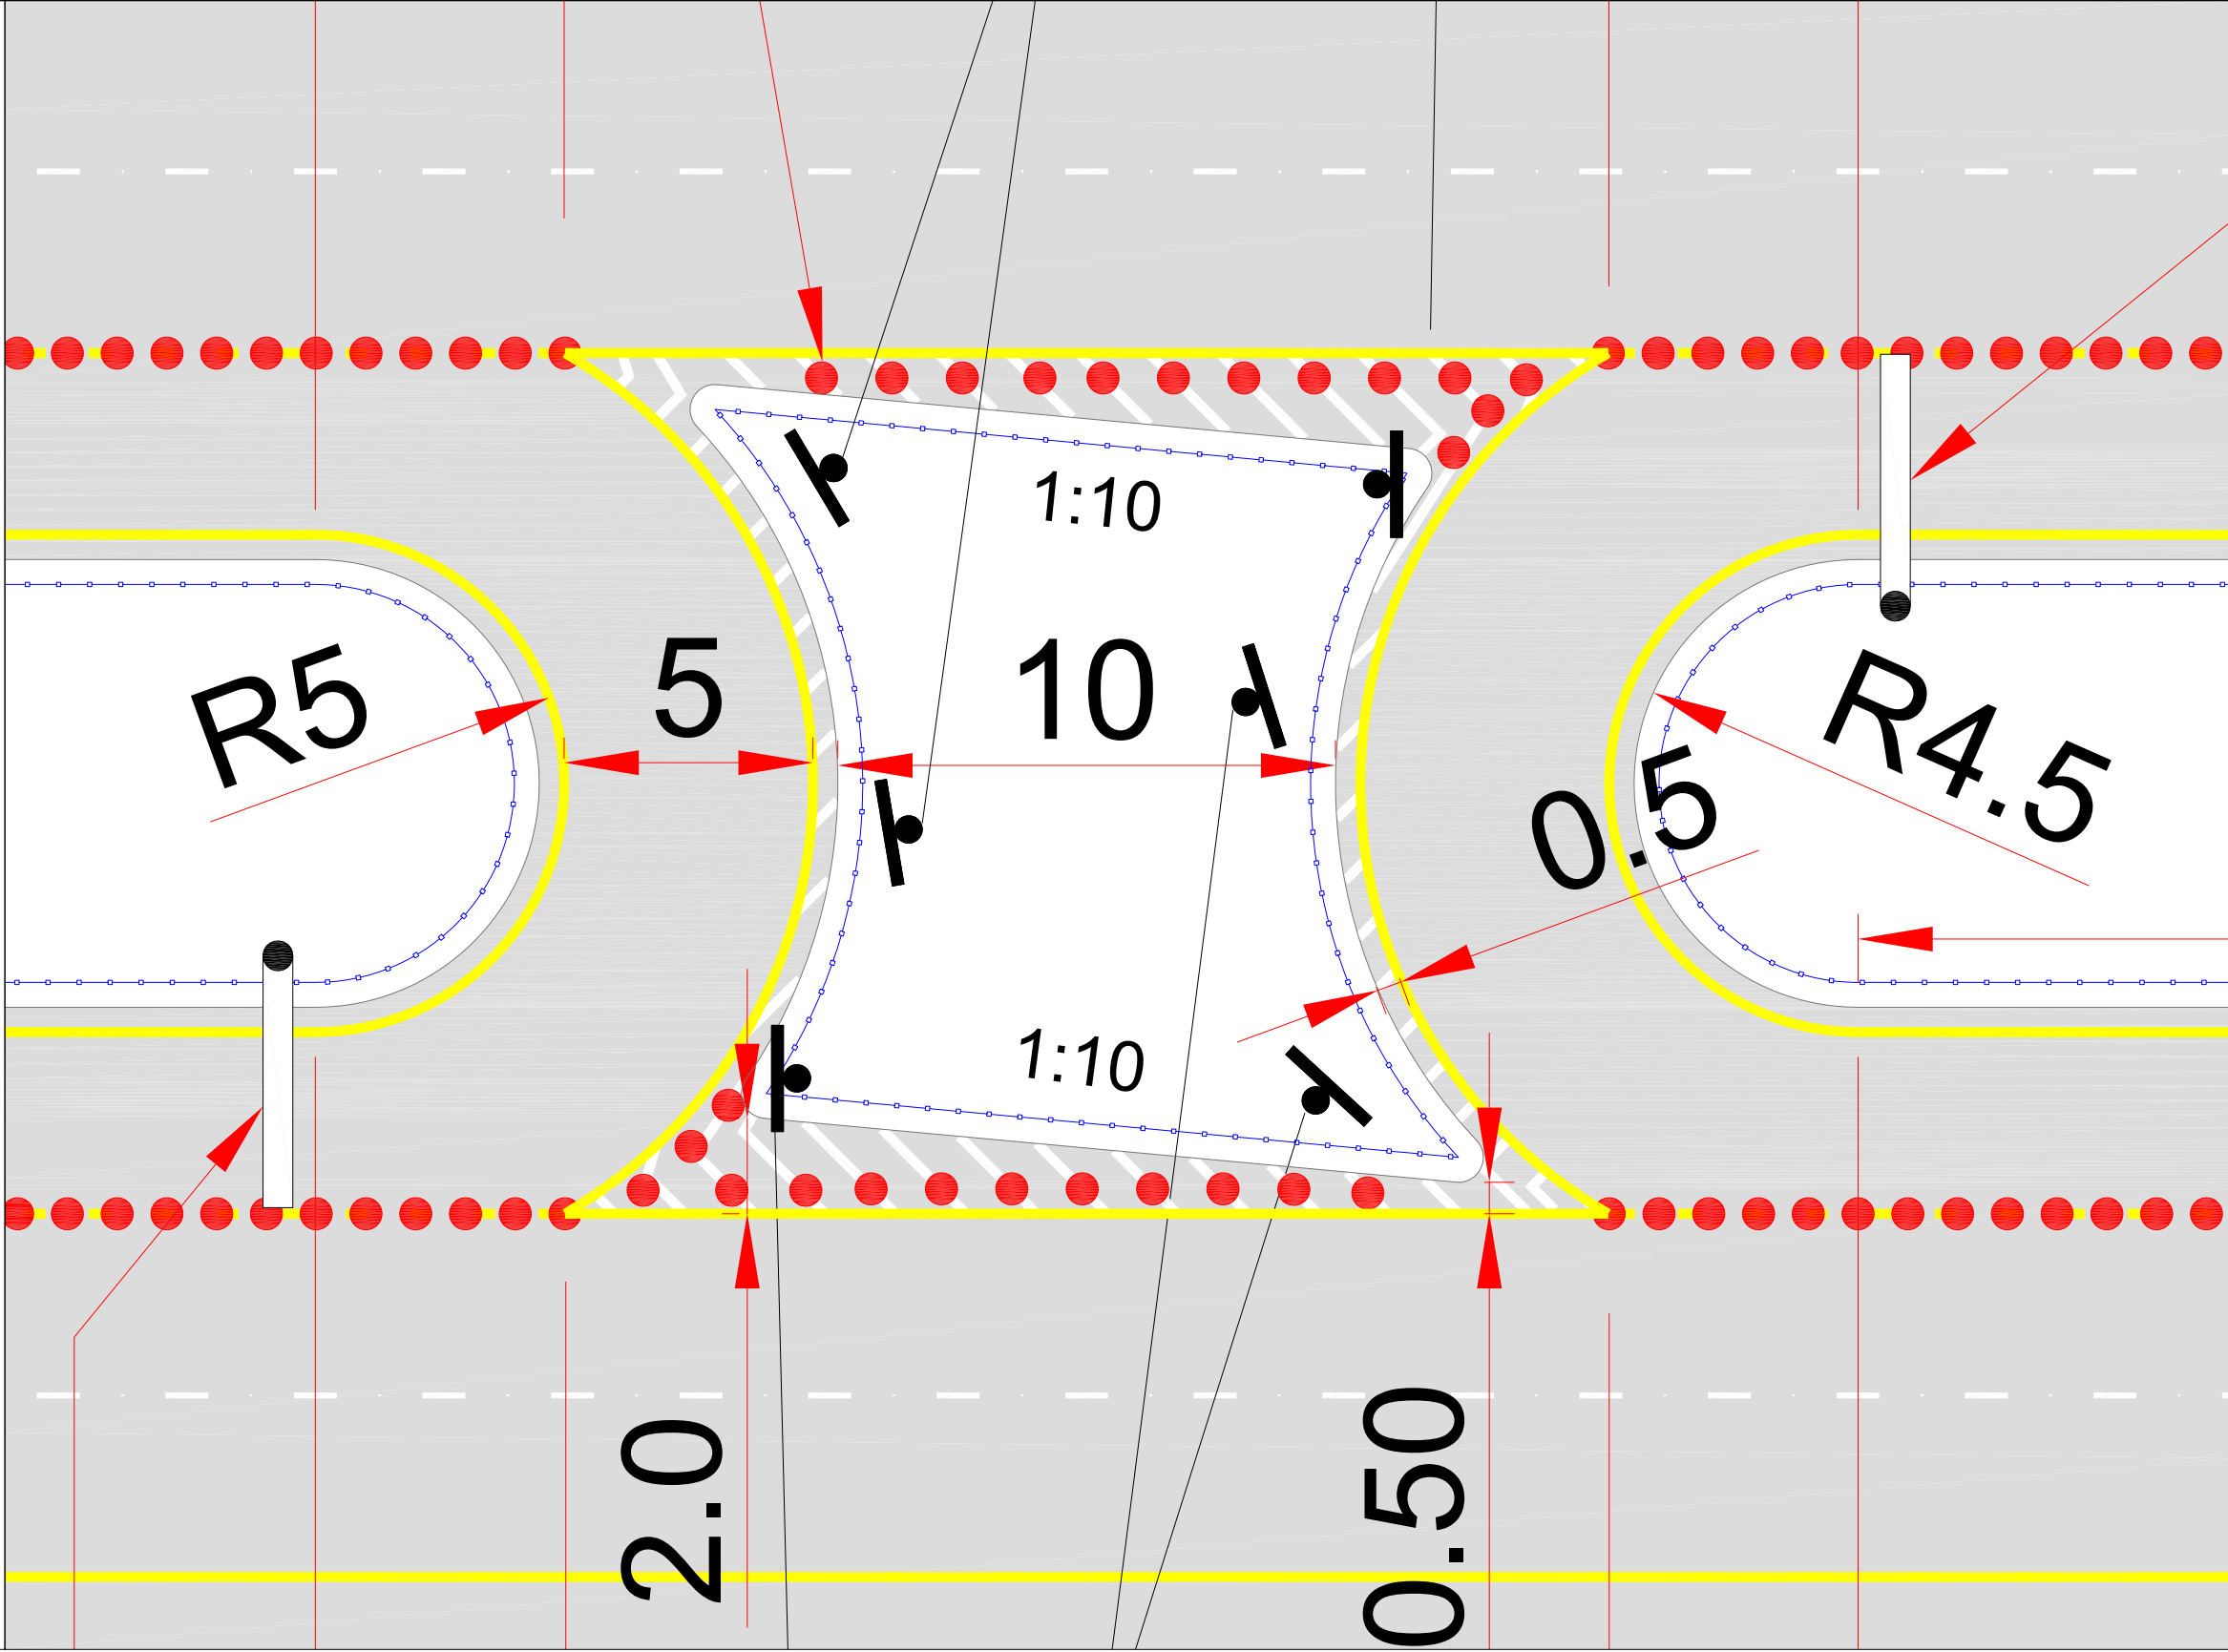

TITLE : مخطط لفحة دوران للخلف لمركبات الصغيرة على طريق سريع ذو جزيرة وسطية ضيقة (حالة خاصة لموقع معين فقط) U-TURN DETAIL FOR PASSENGER CAR AT NARROW-MEDIAN HIGHWAYS (SPECIAL CASE AT SPECIFIC LOCATION ONLY)	
DRAWING NUMBER	DATE : JANUARY 2020
DRAFT, NTS	SHEET SIZE: A1