

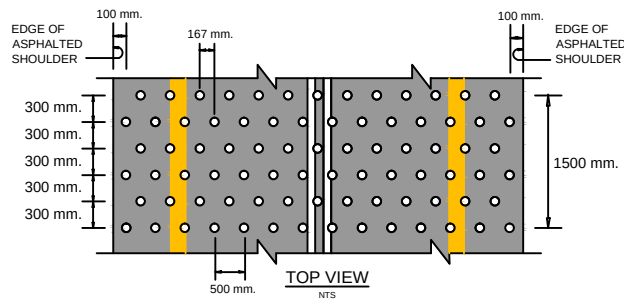
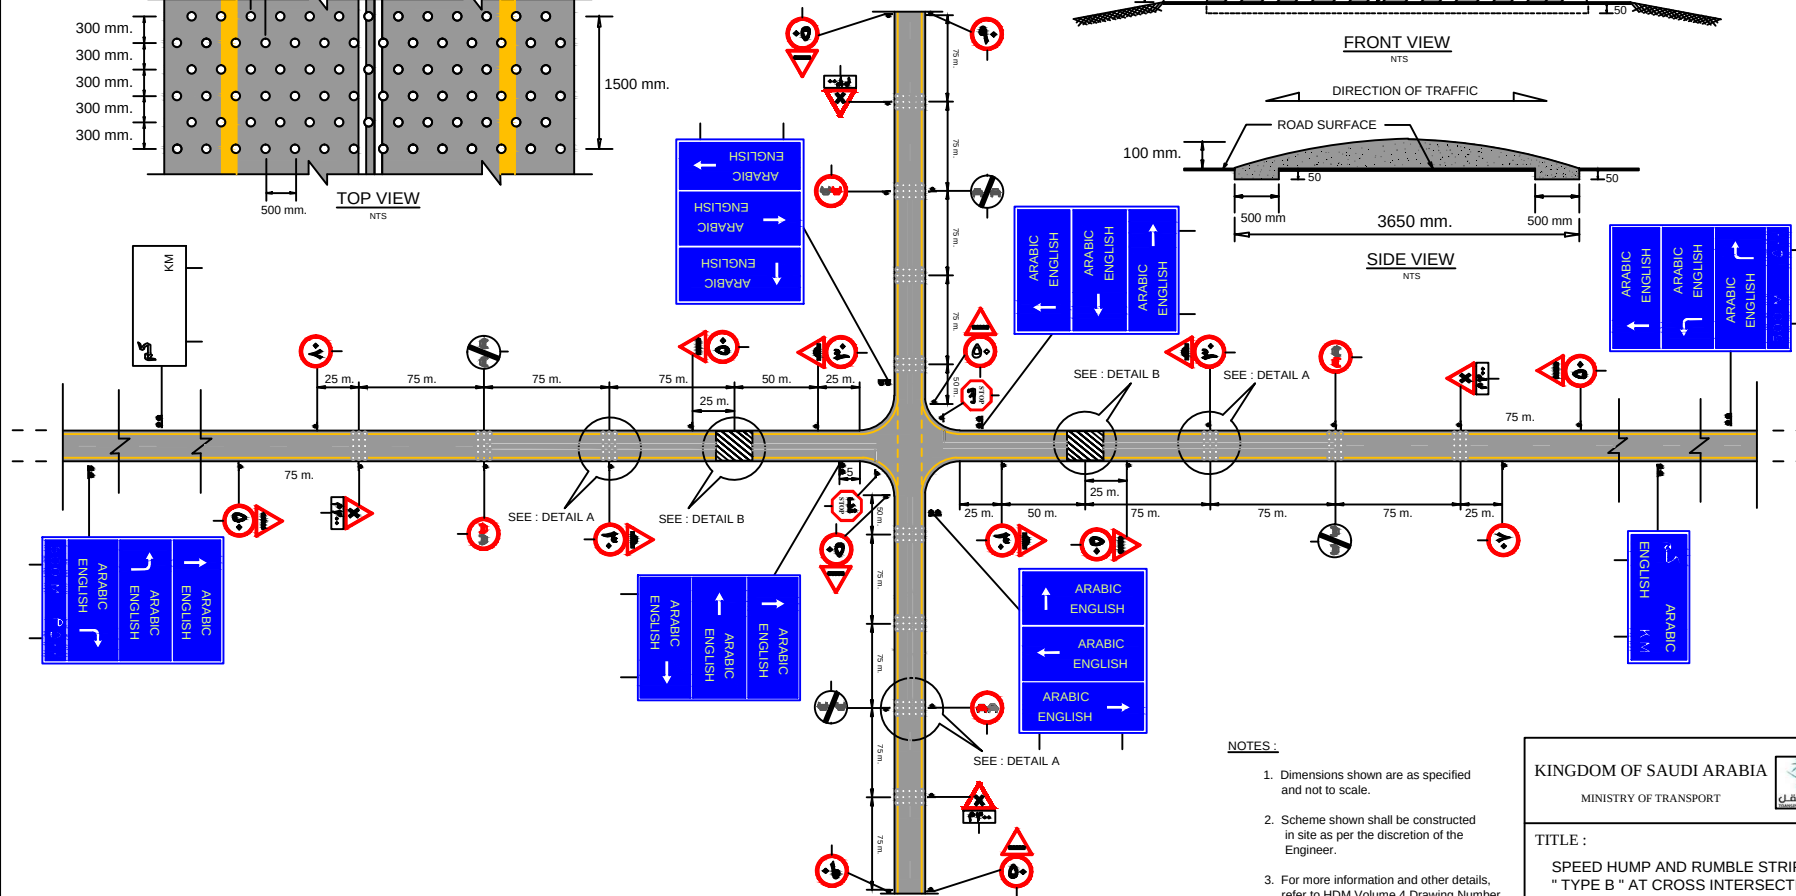


NTS

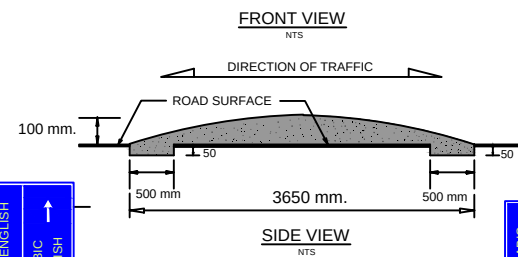

NTS

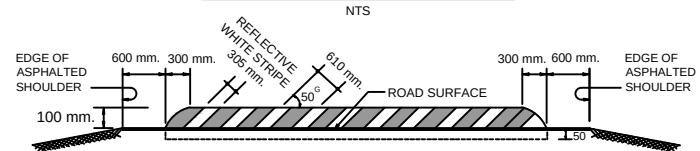

NOTES :

1. Dimensions shown are as specified and not to scale.
2. Scheme shown shall be constructed in site as per the discretion of the Engineer.
3. For more information and other details, refer to HDM Volume 4 Drawing Number TCD - 2 , page 128.

KINGDOM OF SAUDI ARABIA

MINISTRY OF TRANSPORT



TITLE :
SPEED HUMP AND RUMBLE STRIPS
" TYPE B " AT CROSS INTERSECTION

Drawing Number :

Date :

SH/RS - 1

Dhu Al - Hijjah 1437

16/11/2016