
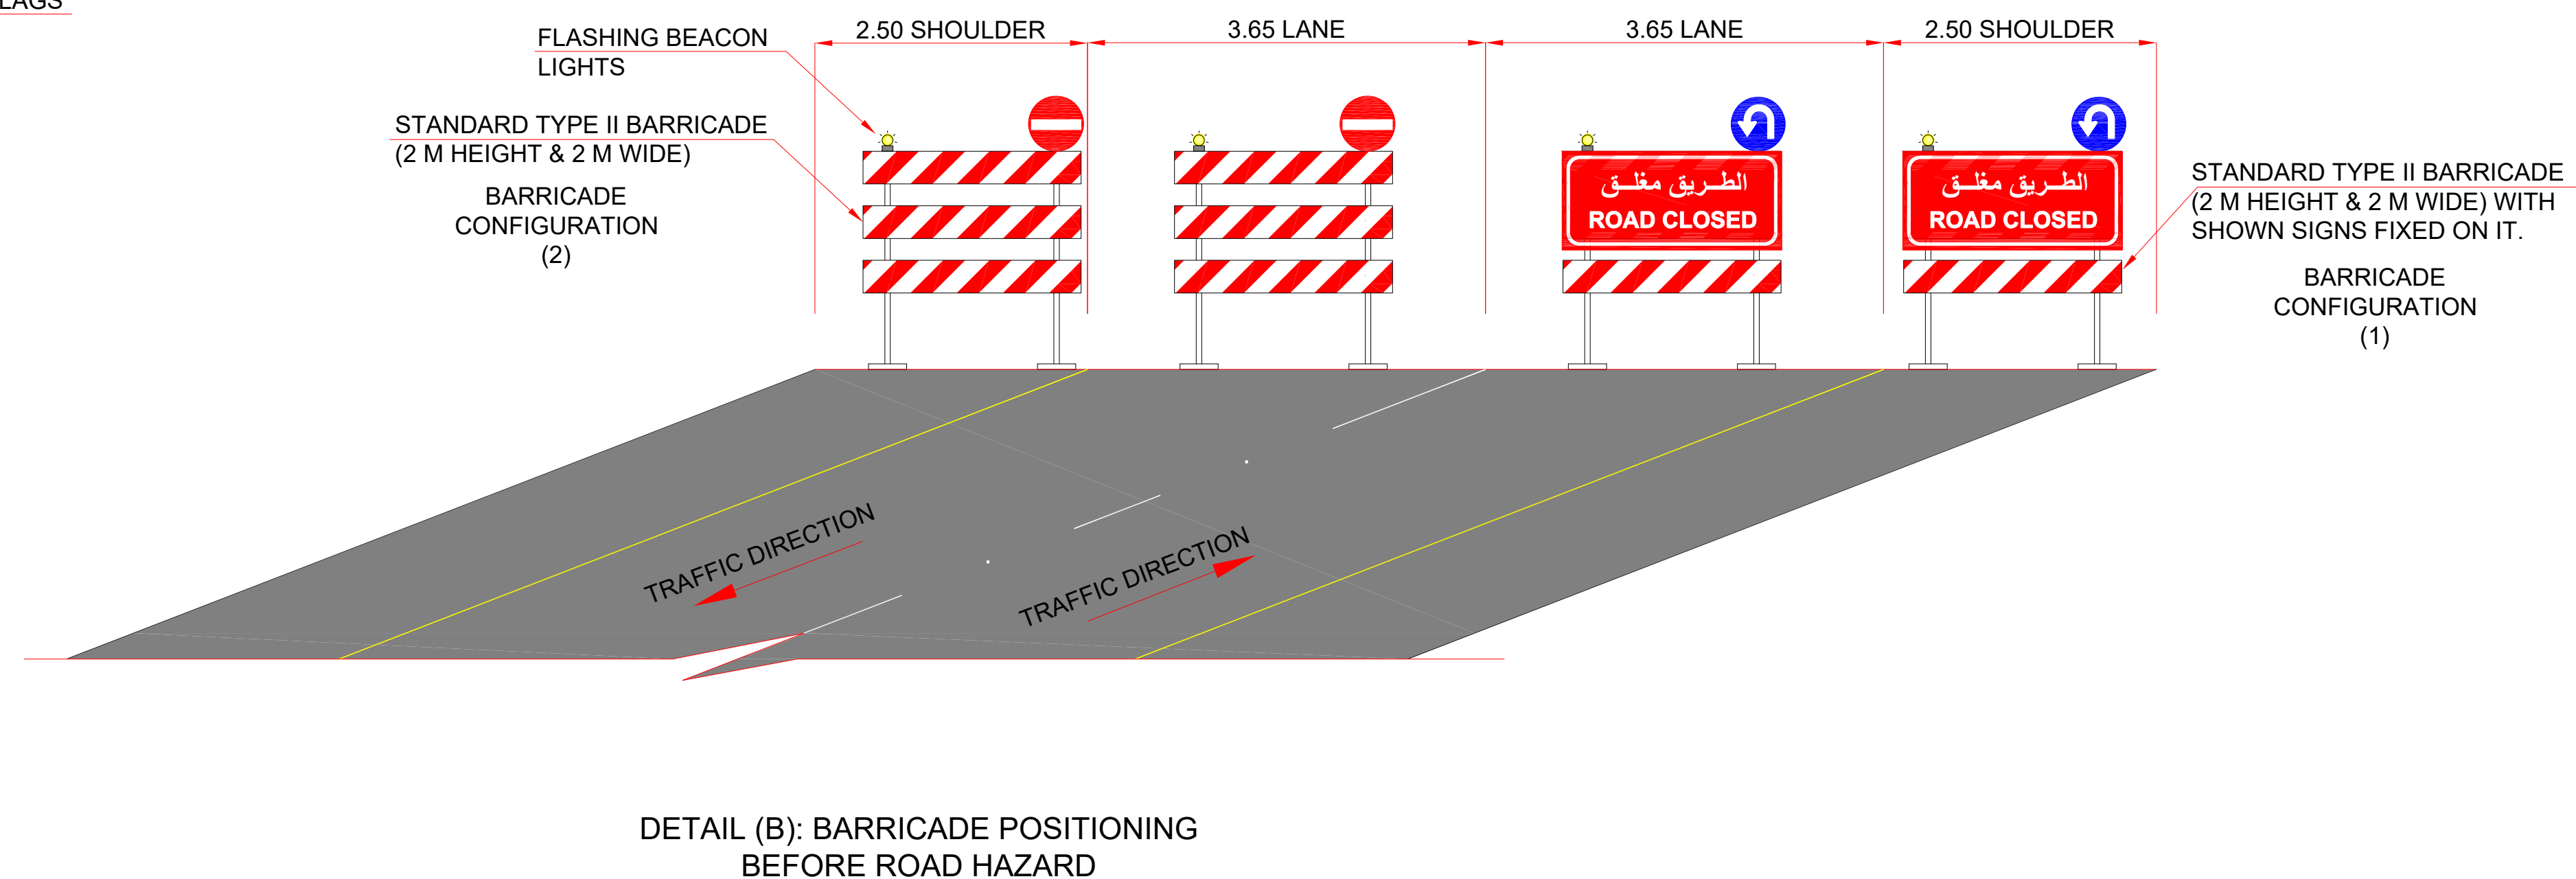
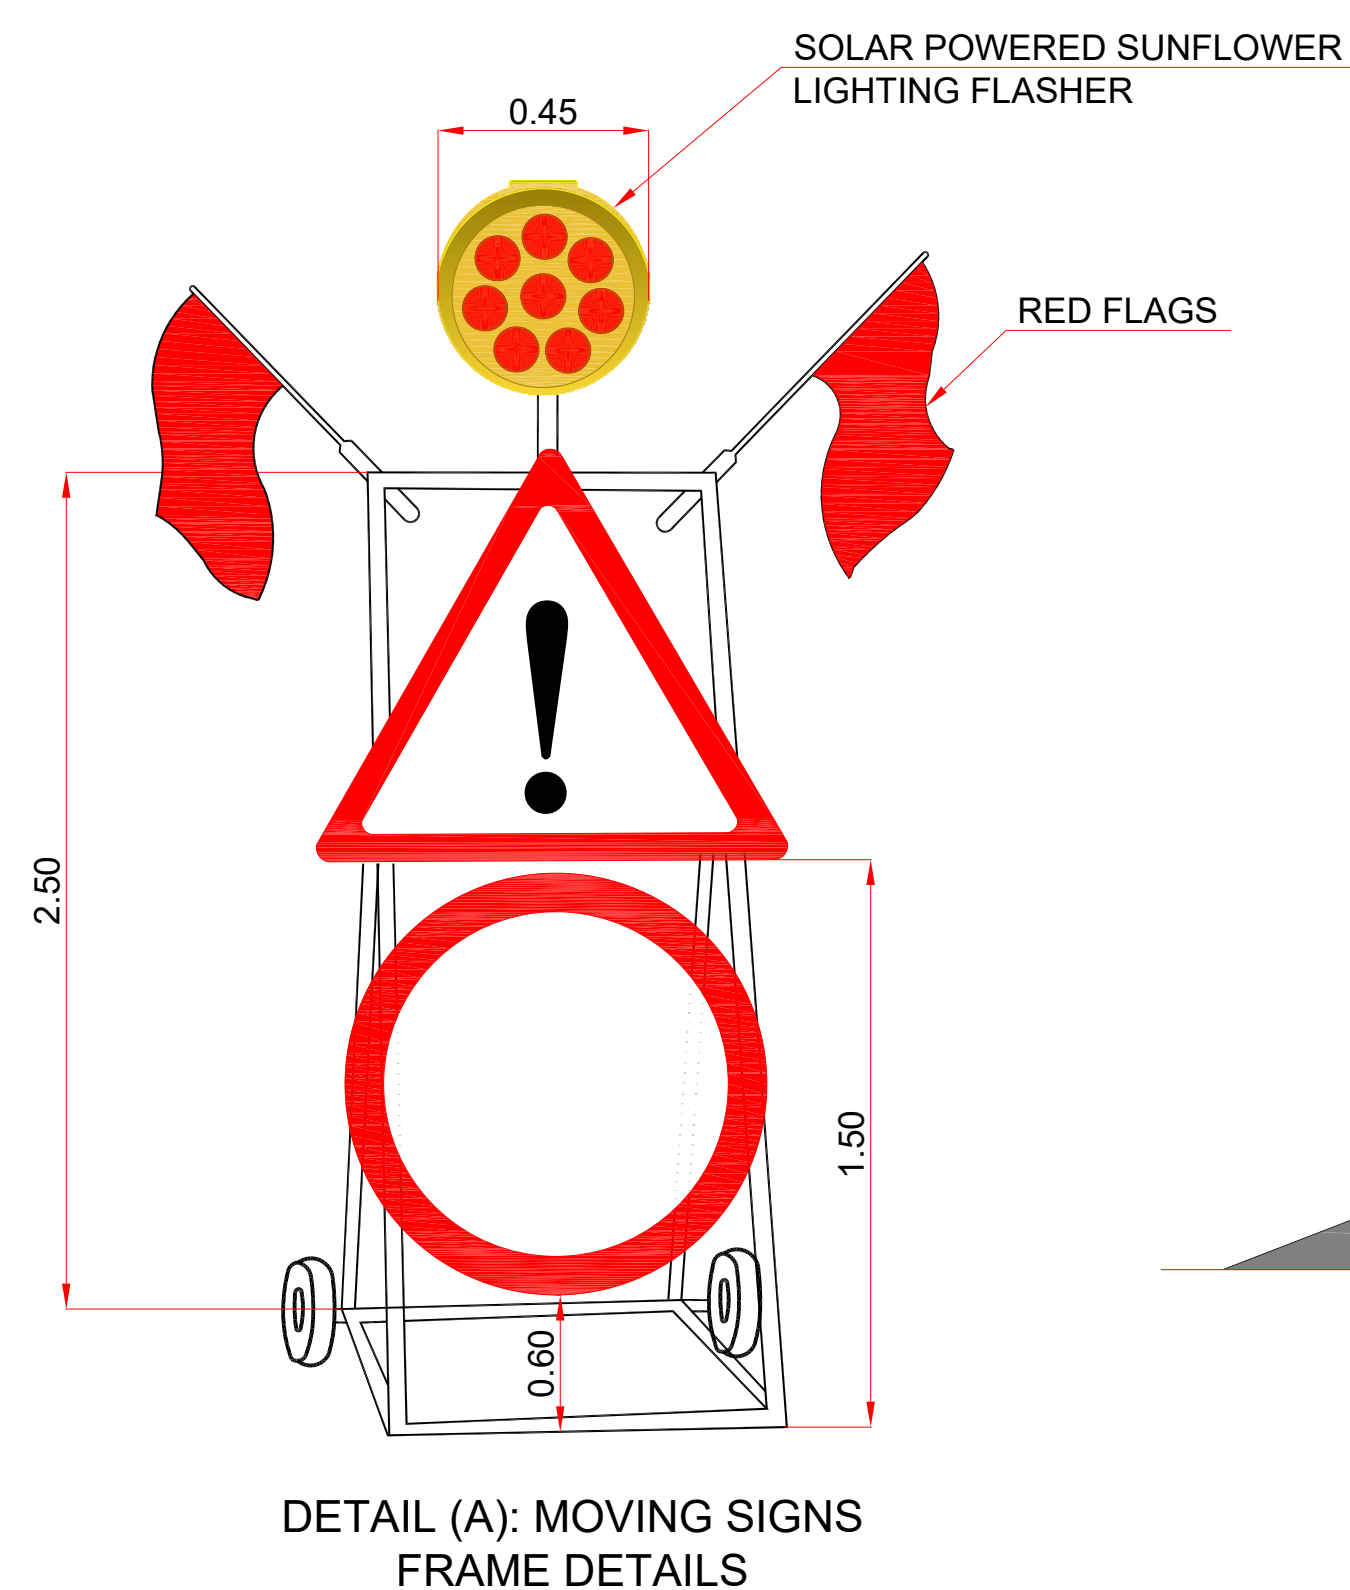
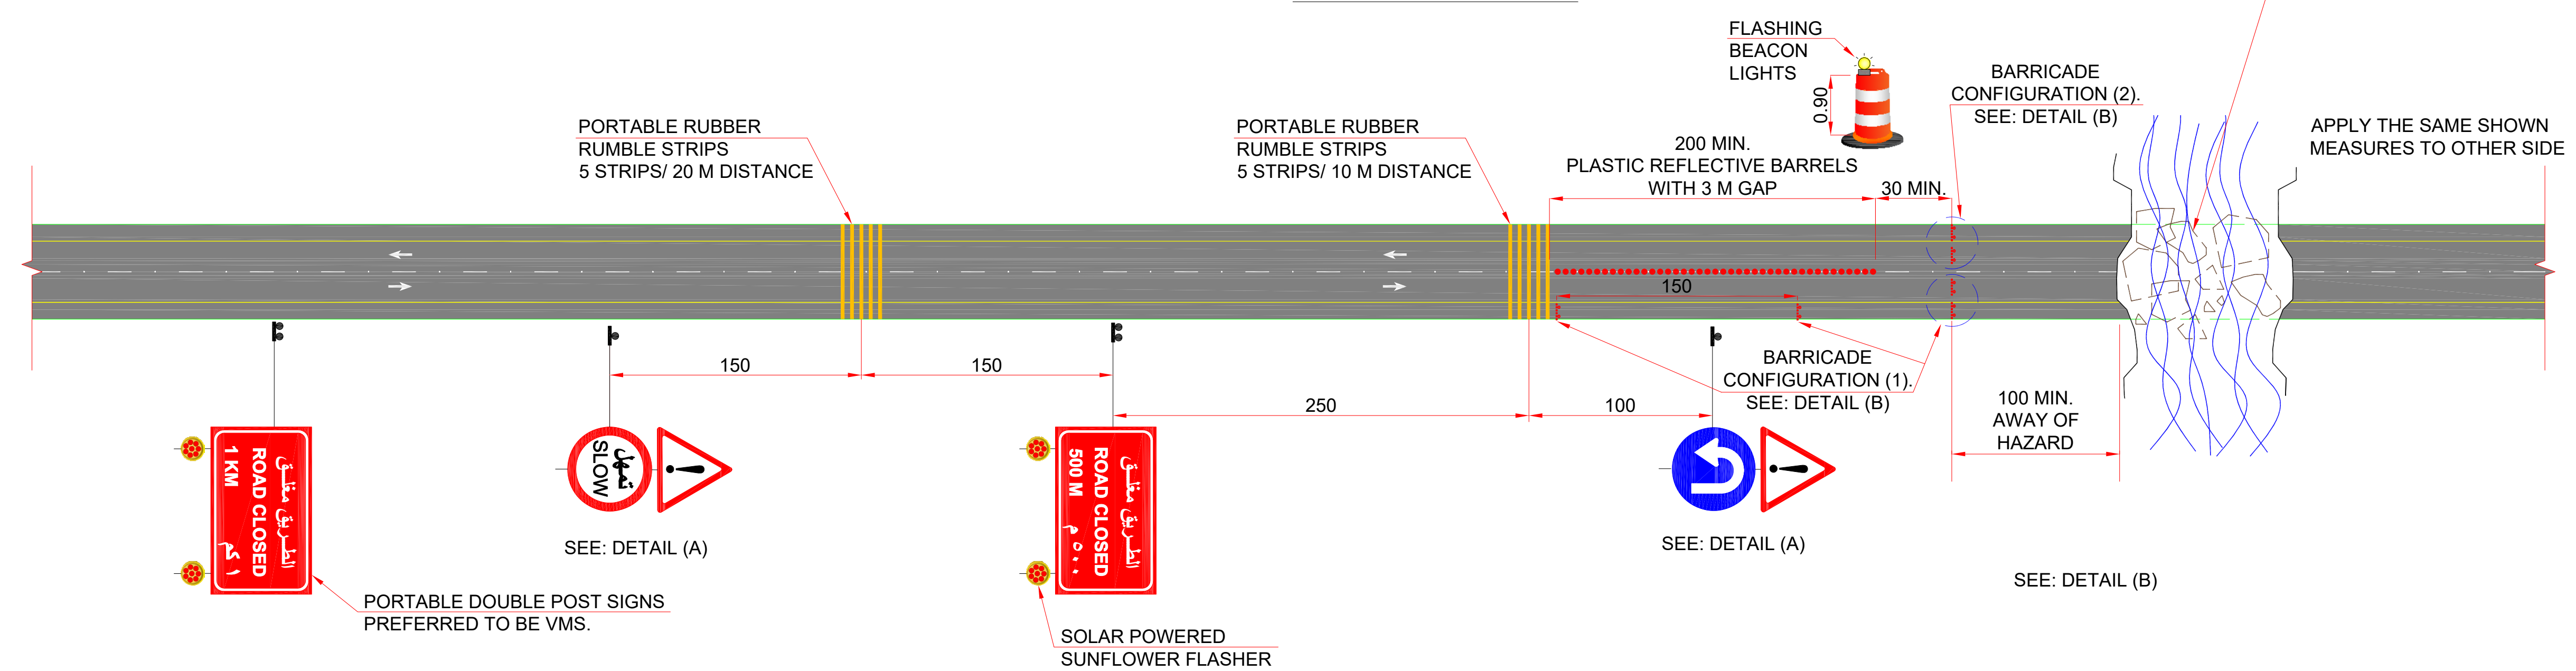


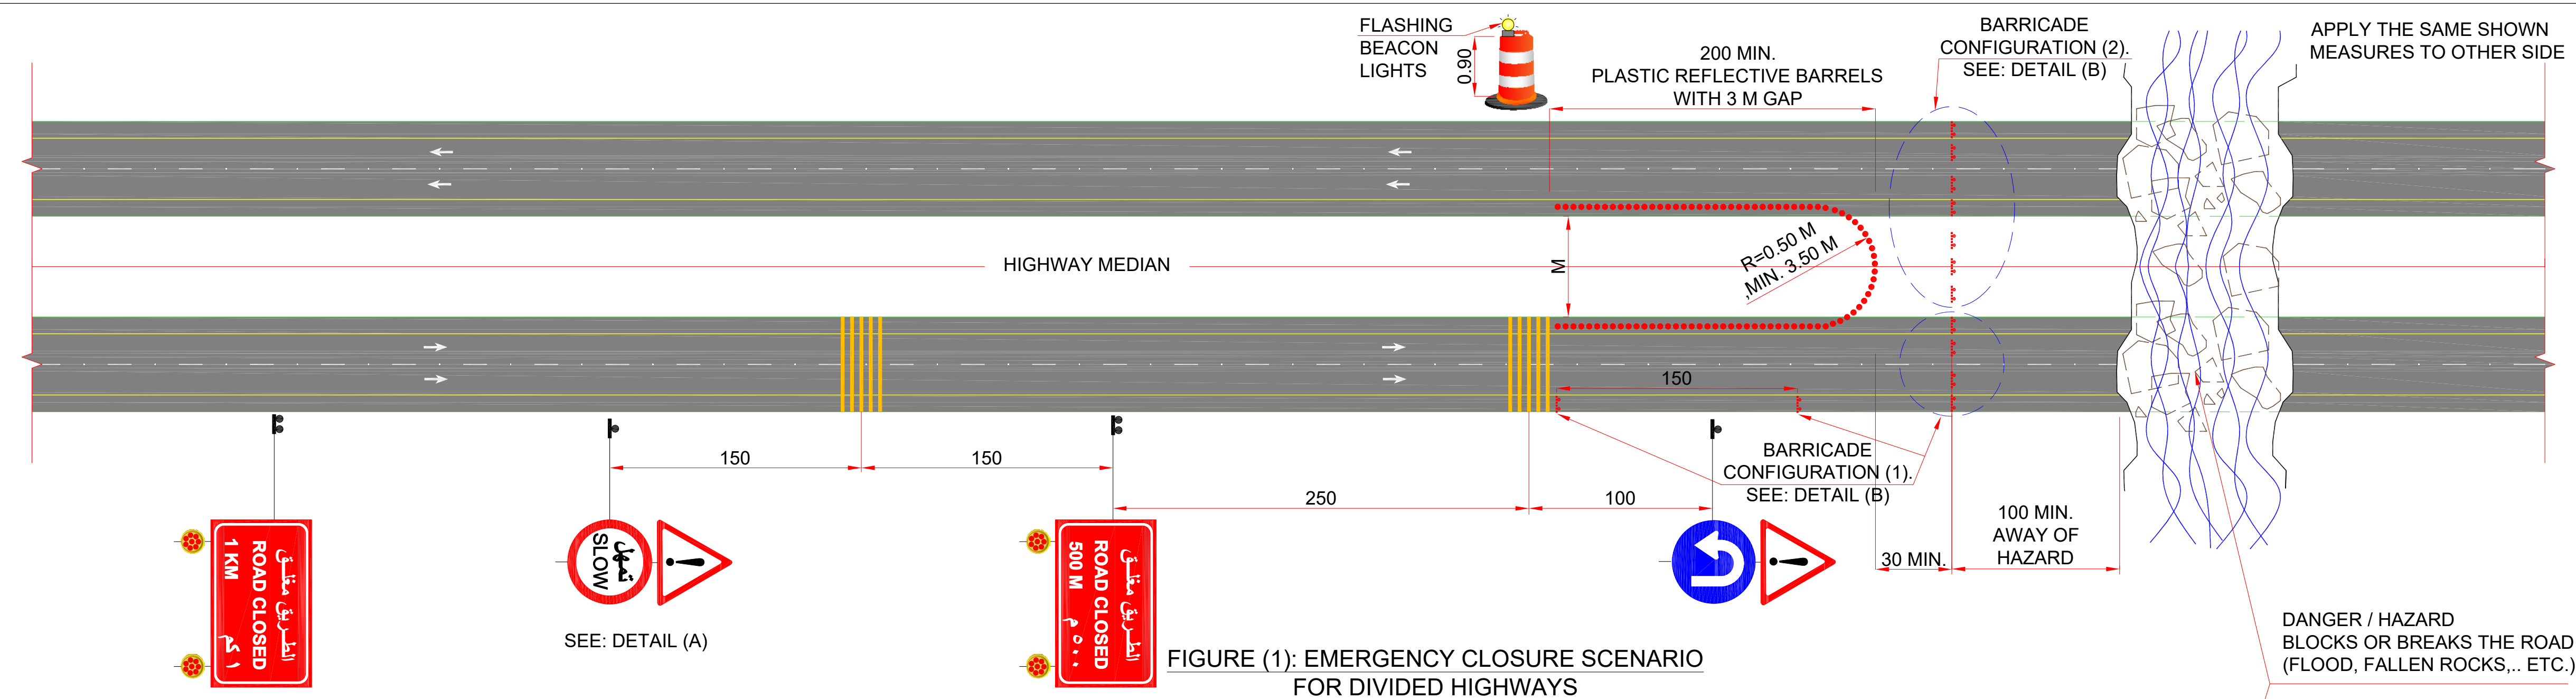

- NOTES:**
1. ALL SHOWN DIMENSIONS ARE IN METERS.
 2. IN CASE OF MOVING HAZARD OR EXPANSION, THE CONTRACTOR SHOULD OBSERVE AND TAKE ALL NECESSARY ACTIONS TO ASSURE SAFETY FOR ROAD USERS, WORK STAFF AND DEVICES.
 3. ALL BARRICADES AND CHANNELING DEVICES SHOULD BE PROVIDED WITH FLASHING LIGHTS AS SHOWN.
 4. PORTABLE SIGNS ARE PREFERRED TO BE VMS SPECIALLY FOR NIGHT OPERATION.
 5. FLAG HOLDERS SHOULD BE POSITIONED IN SITE BEHIND BARRICADES.
 6. IN CASE OF SINGLE HIGHWAY CLOSURE, THE CONTRACTOR SHOULD PREPARE PROVIDE THE MAXIMUM USABLE EARTH SHOULDERS FOR TRAFFIC U-TURN MOVEMENT AS PER SITE CONDITIONS.
 7. IN CASE OF STRONG WINDS, PORTABLE SIGN FRAMES COULD BE STABILIZED USING HEAVY SAND SACS.