
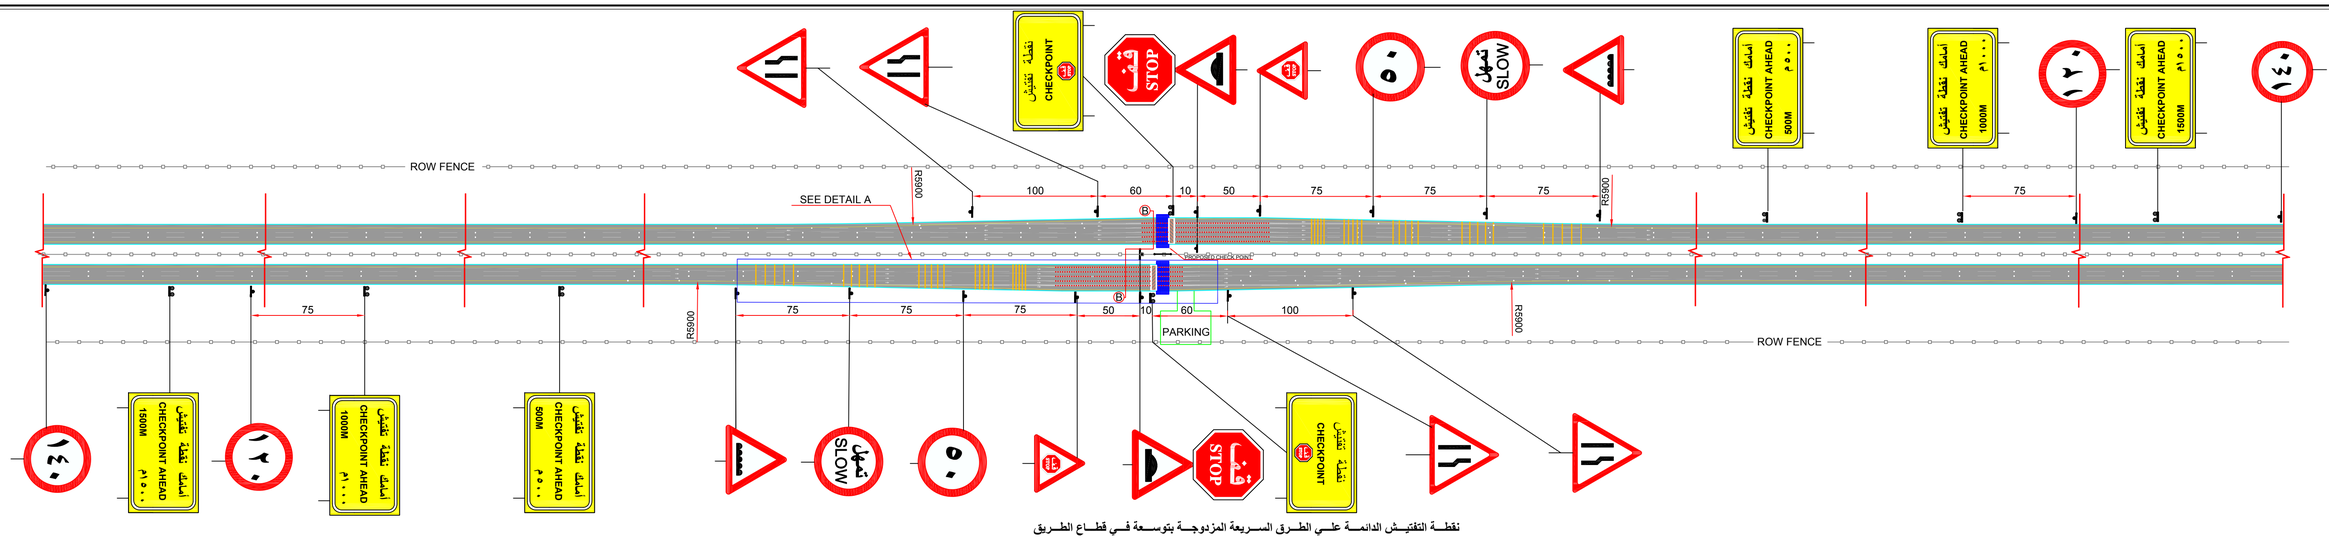


نقطة التفتيش الدائمة على الطرق السريعة المزدوجة في قطاع الطريق


PERMANENT CHECK POINT AT DIVIDED HIGHWAY WITH WIDENING TYPE (B)

N.T.S

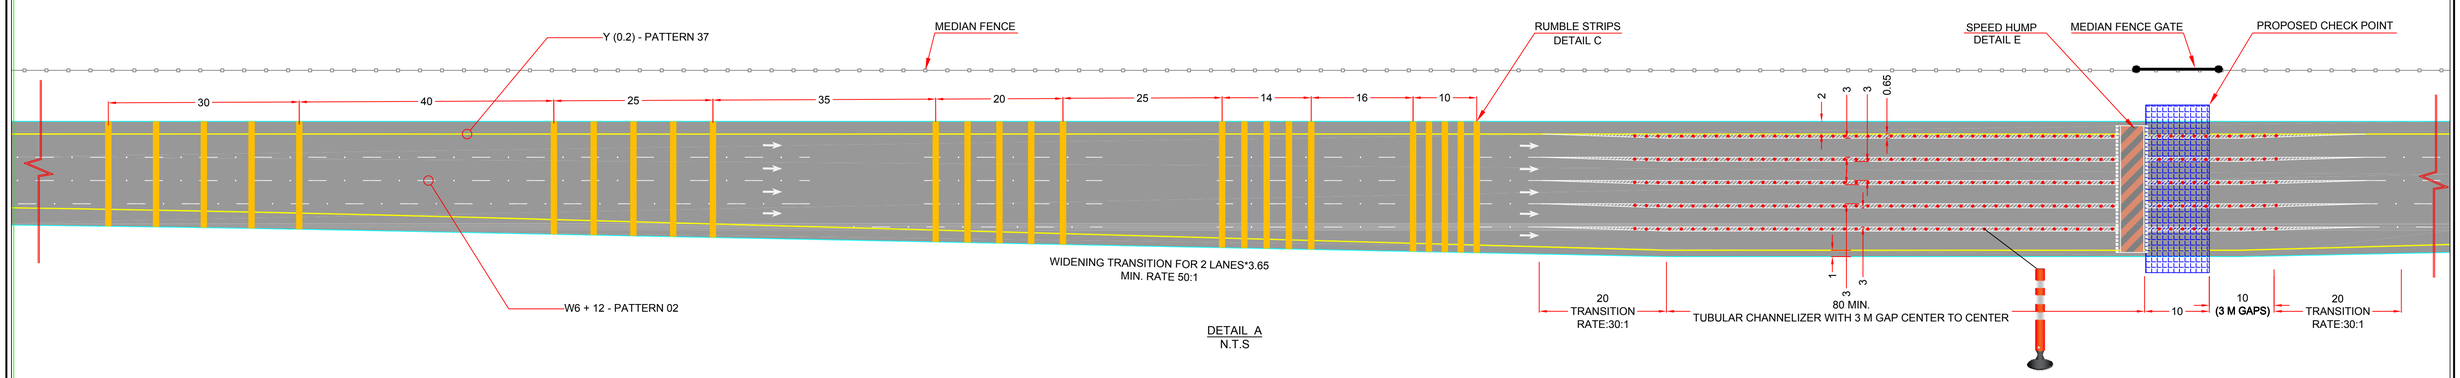


DETAIL A

N.T.S

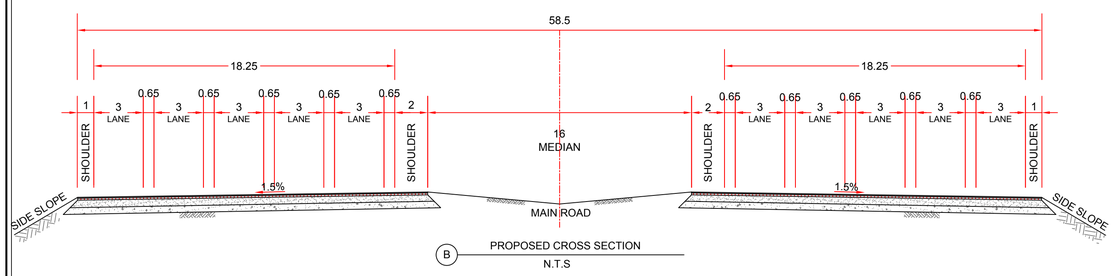

B PROPOSED CROSS SECTION


N.T.S

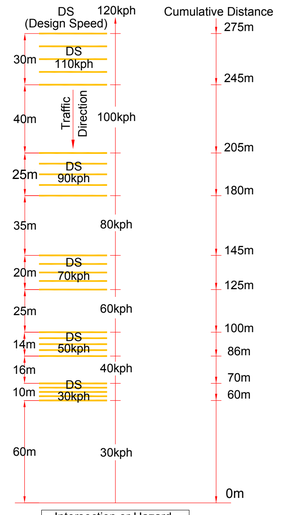


DETAIL C : RUMBLE STRIP

N.T.S


DS (kph)	Y (m)	Y/4 (m)
110	30	7.50
90	25	6.25
70	20	5.00
50	14	3.50
30	10	2.50

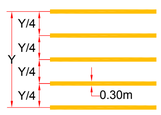

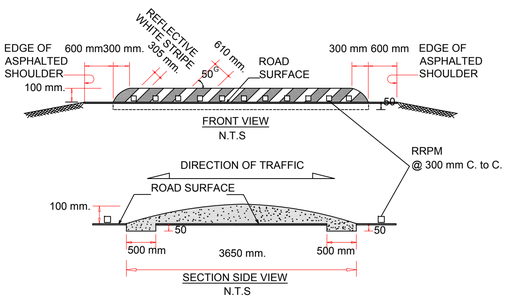

DETAIL E : SPEED HUMP W/ RRPM

N.T.S

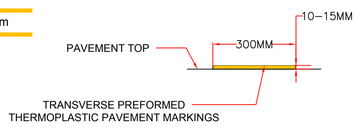

DETAIL D : THERMOPLASTIC MARKING DETAIL

N.T.S

NOTES

1. ALL DIMENSIONS ARE IN METRIC UNITS, UNLESS OTHERWISE MENTIONED.
2. RRPM (REFLECTIVE RAISED PAVEMENT MARKER) WITH SOLAR CELLS.
3. THIS TYPICAL DETAIL IS VALID FOR DIVIDED HIGHWAYS AND TO BE ADJUSTED AS PER ACTUAL OPERATIONAL SPEED AND RESUBMITTED FOR APPROVAL.
4. CHECKPOINT AREA MUST BE FURNISHED WITH STREET LIGHTING AS PER MOT STANDARDS (IF NO ELECTRICAL POWER IS AVAILABLE, SOLAR POWERED LIGHTS SHOULD BE PROVIDED.)
5. THE SHOWN DETAILS IS FOR PERMANENT OPERATION MODE USING STANDARD SIGNS.
6. THE SHOWN DETAILS ARE VALID FOR OPERATION SPEED OF 120 KPH.
7. THE CONTRACTOR SHOULD ACKNOWLEDGE TO MOT ALL OTHER REQUIRED PRECAUTIONS SHOULD BE TAKEN ON-SITE, PREPARING THE NECESSARY PROPOSALS FOR MOT APPROVAL.

KINGDOM OF SAUDI ARABIA

MINISTRY OF TRANSPORT

وزارة النقل
TRANSPORT MINISTRY

TITLE :

المخطط النموذجي -(ب) لنقطة التفتيش الدائمة على الطرق السريعة المزدوجة بتوسعة في قطاع الطريق

TYPICAL SAFETY DEVICES AT APPROACHES TO PERMANENT CHECKPOINT AT DIVIDED HIGHWAY WITH WIDENING -TYPE (B)

DRAWING NUMBER	DATE : DECEMBER 2018
RD1-MOT-RSD-DWG-1812-002	SHEET SIZE: A1